ELEVATION FINISHES	
CODE	DESCRIPTION
300	ALUMINUM COMPOSITE PANELS
301	VERTICAL METAL CLADDING
302	EIFS
303	ACRYLIC STUCCO
304	PREFINISHED METAL FLASHING
305	SCUPPER
306	PRECAST CONCRETE PANELS

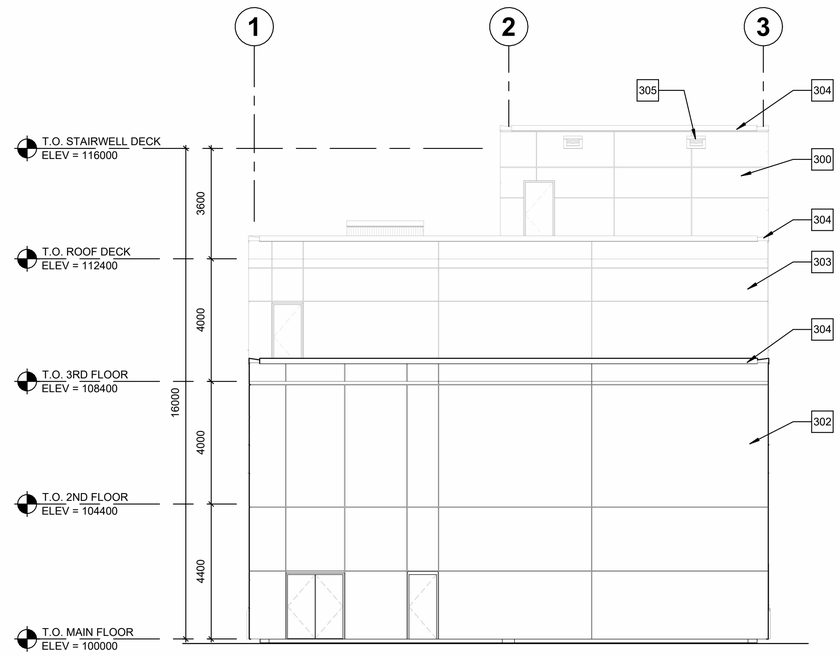

2 A2.1 **WEST ELEVATION**
SCALE = 1 : 100

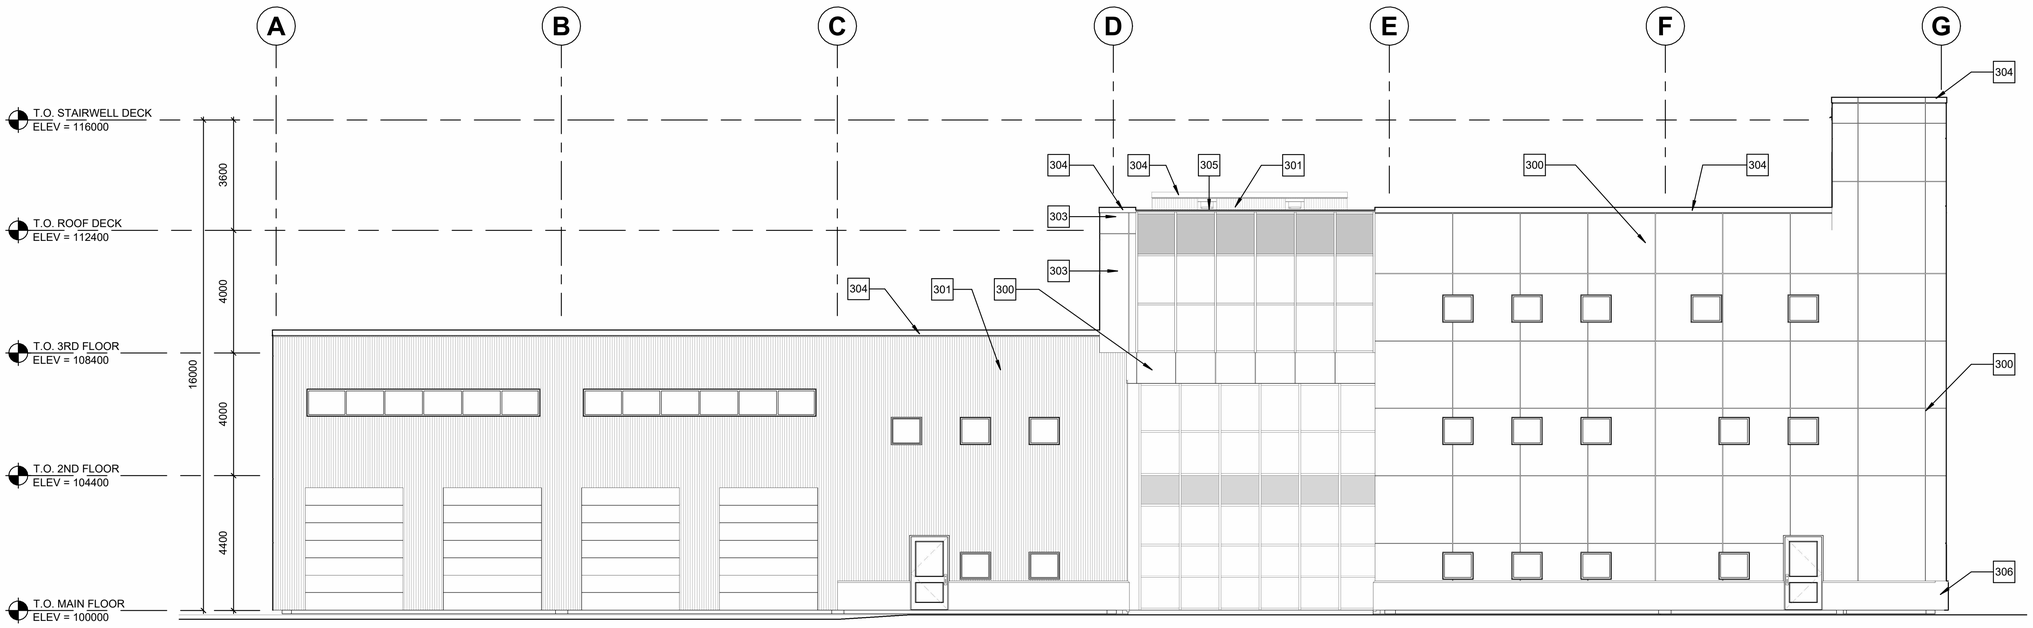

1 A2.1 **SOUTH ELEVATION**
SCALE = 1 : 100

SCHOOL OF CONSTRUCTION AND APPLIED BUILDING SCIENCE
ARCHITECTURAL TECHNOLOGY

No.	Description	Date

NAIT AMBULANCE HEADQUATERS

SOUTH & WEST ELEVATIONS

Class Number	A03
Date	23/03/2026
Drawn by	CHIDERA UZO
Instructor	ANDRE LUCENA

A3.1

Scale 1 : 100

C:\SCHOOL\PORTFOLIO\PORTFOLIO AMBULANCE STATION.rvt