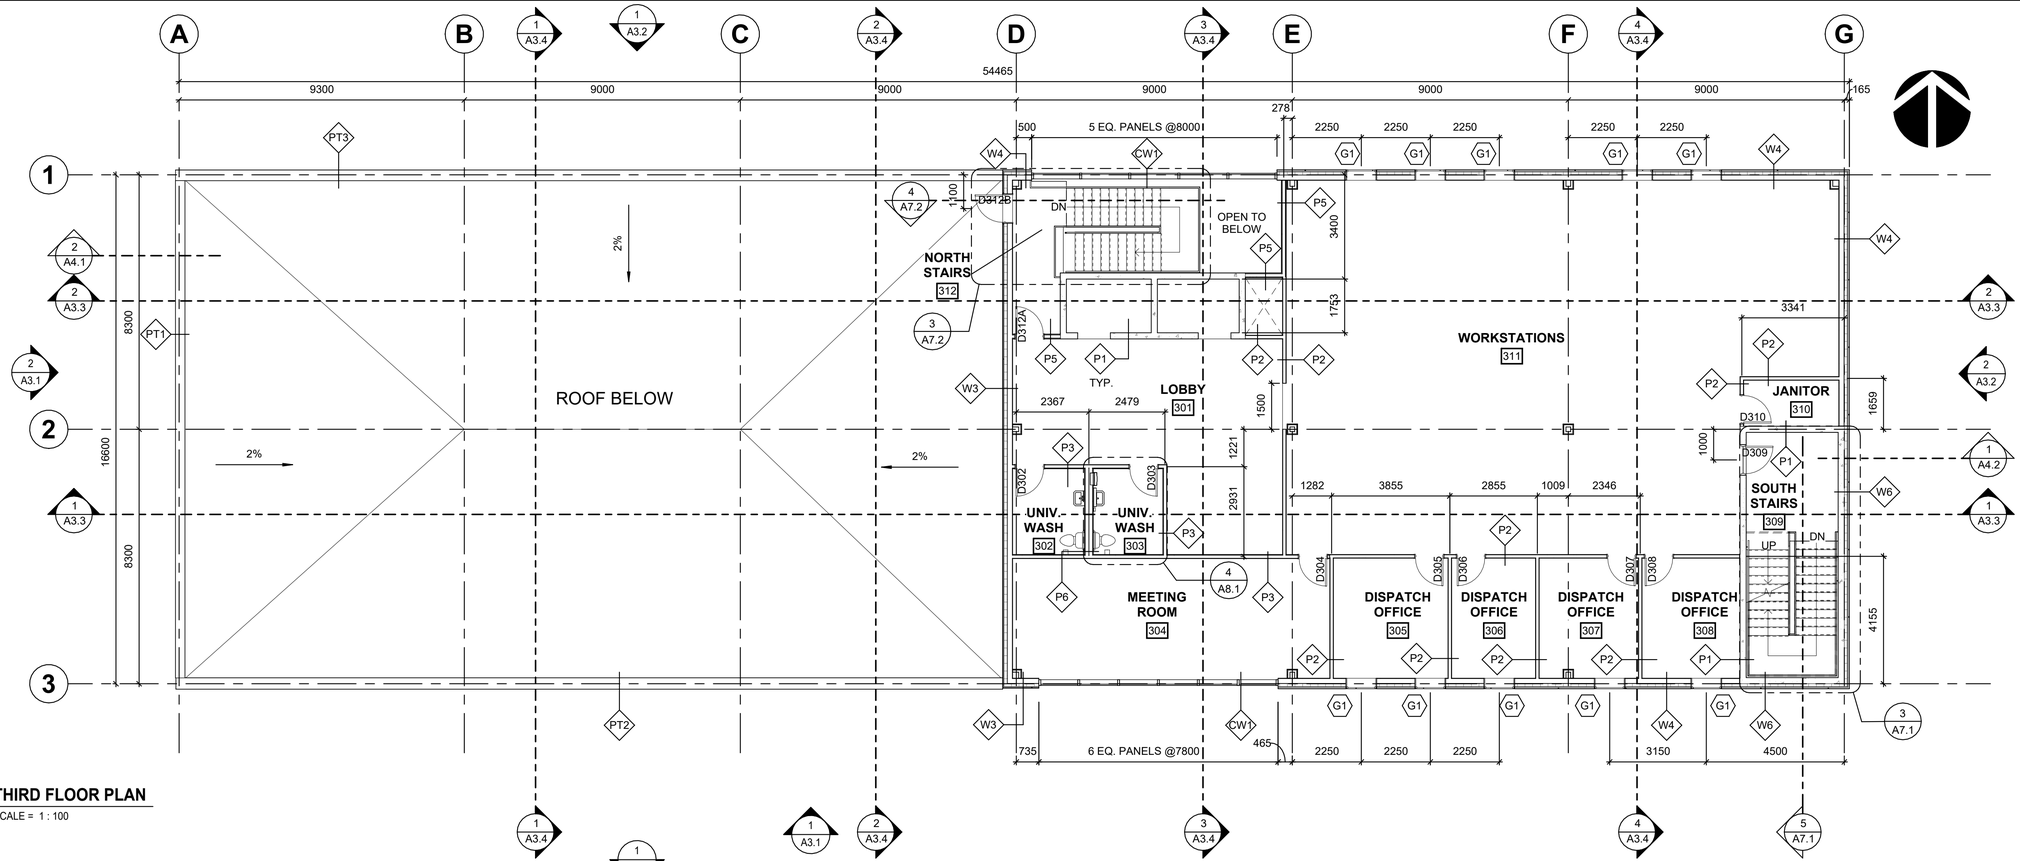

1 A2.3 **THIRD FLOOR PLAN**
SCALE = 1 : 100

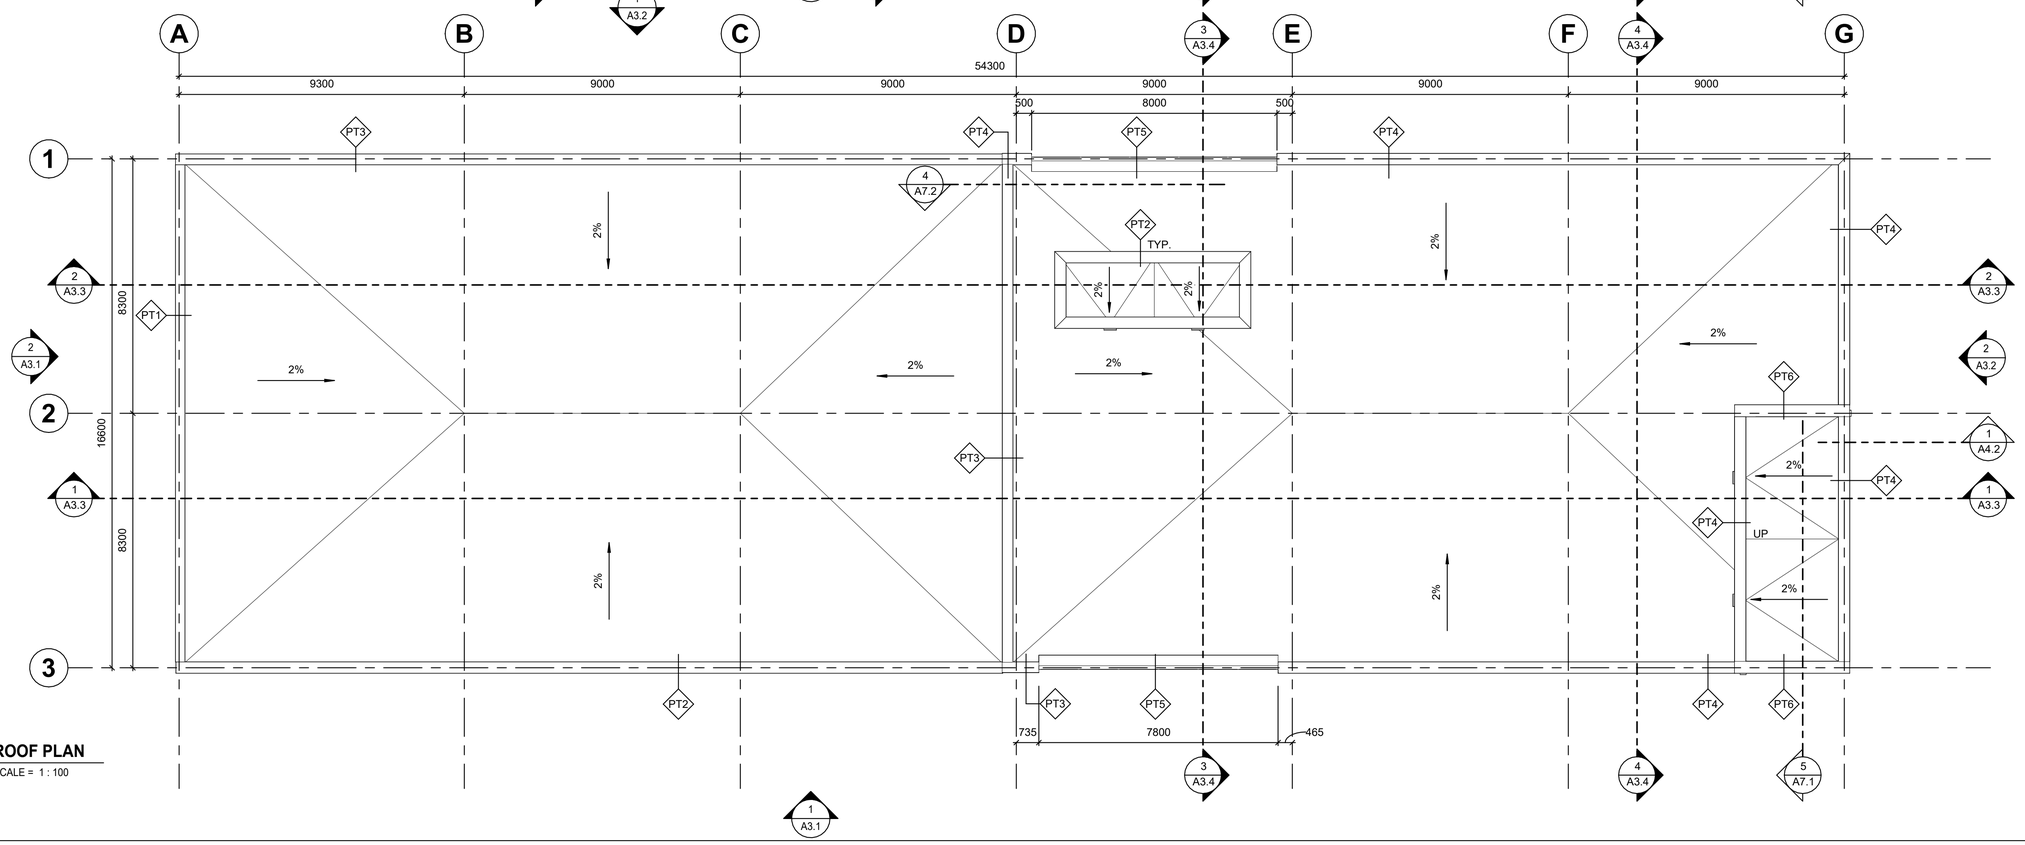

2 A2.3 **ROOF PLAN**
SCALE = 1 : 100

NAIT

SCHOOL OF CONSTRUCTION AND APPLIED BUILDING SCIENCE

ARCHITECTURAL TECHNOLOGY

No.	Description	Date

NAIT AMBULANCE HEADQUARTERS

THIRD FLOOR & ROOF PLAN

Class Number	A03
Date	23/03/2026
Drawn by	CHIDERA UZO
Instructor	ANDRE LUCENA
	A2.3
Scale	1 : 100

C:\SCHOOL\PORTFOLIO\PORTFOLIO AMBULANCE STATION (2).rvt