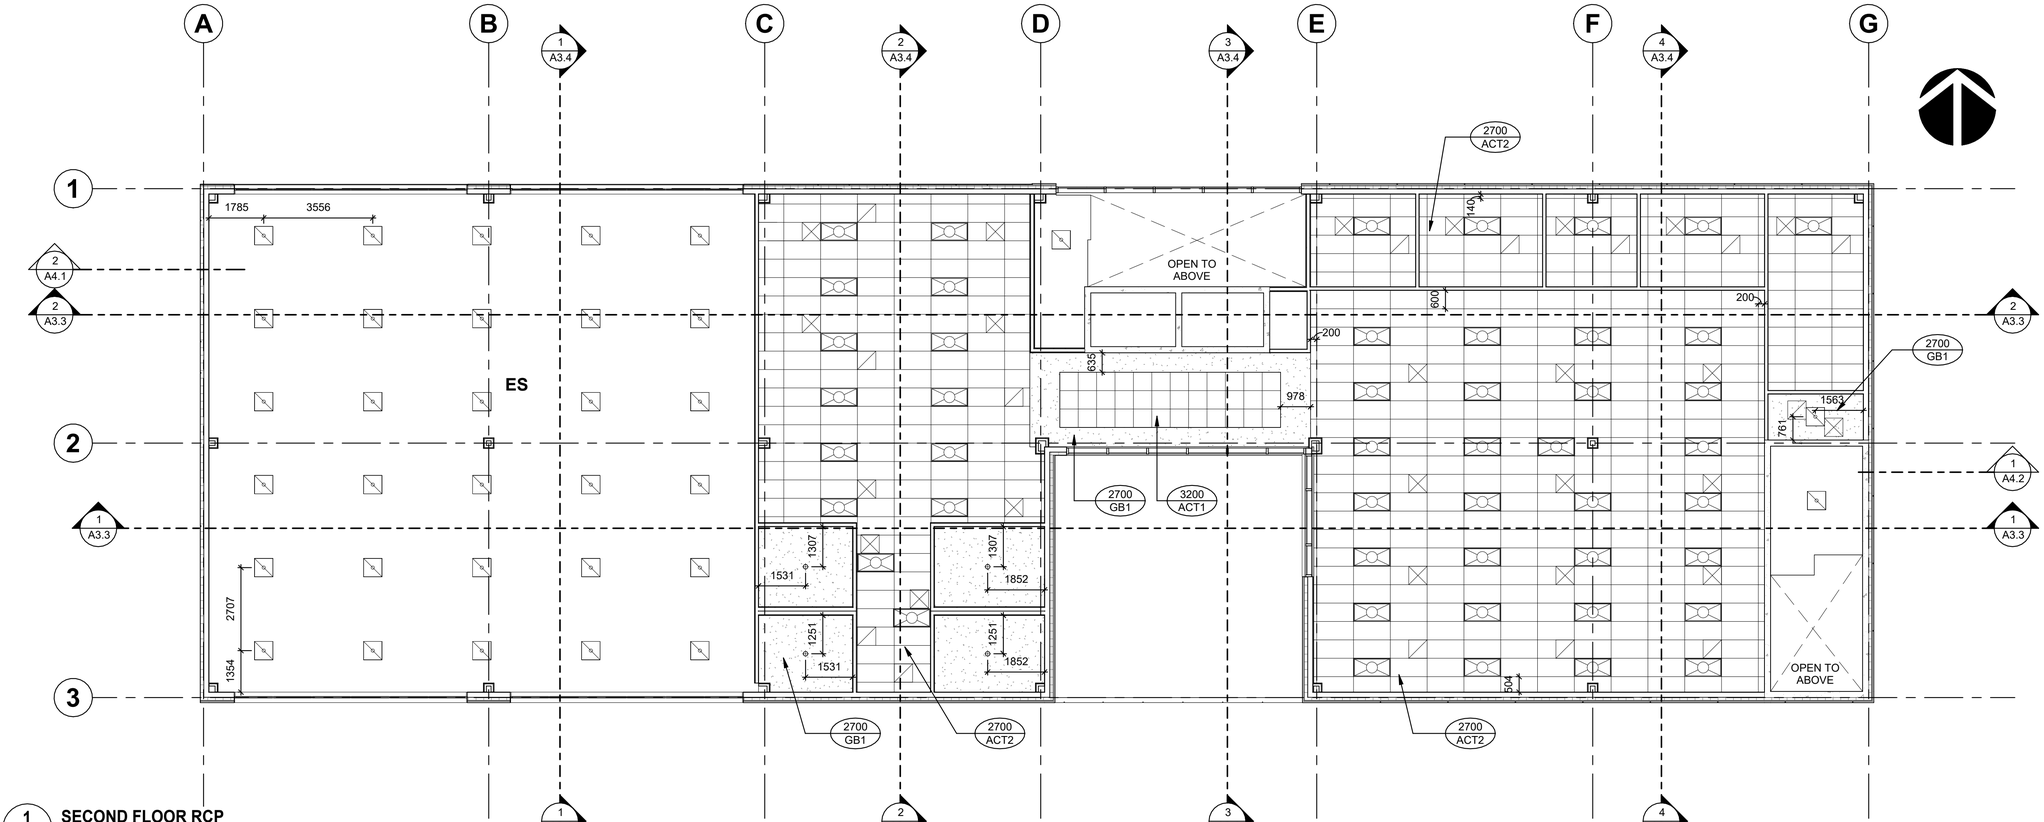

1 A2.5 **SECOND FLOOR RCP**
SCALE = 1 : 100

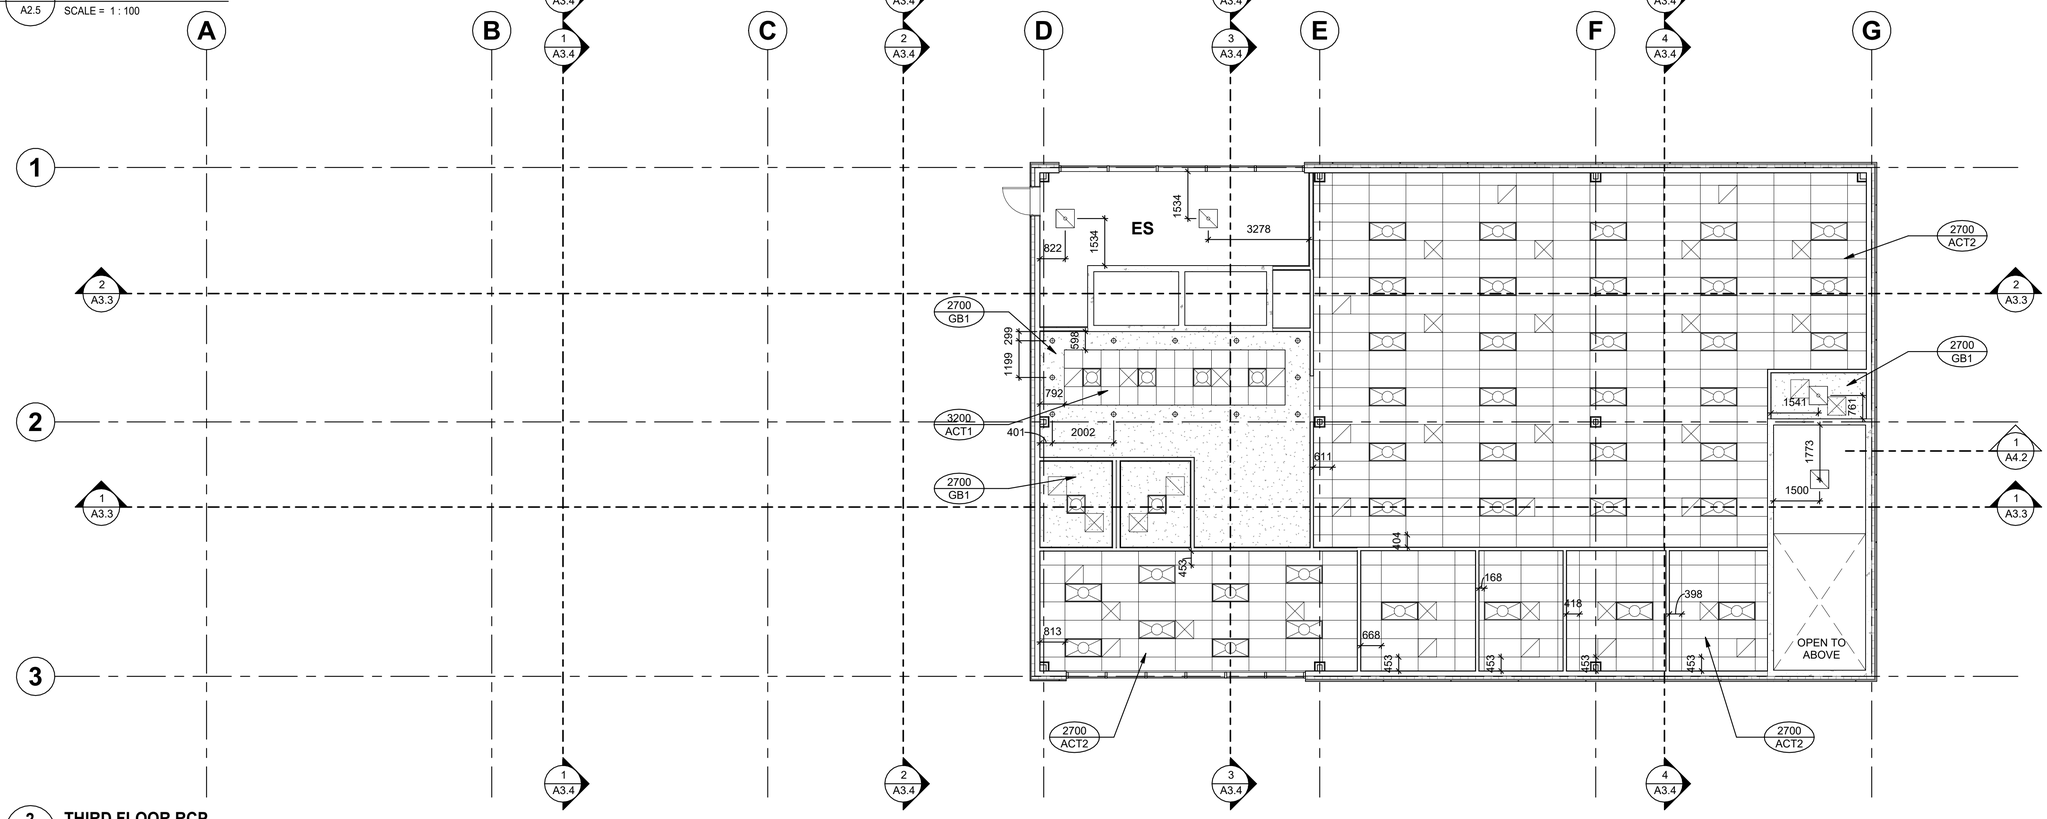

2 A2.5 **THIRD FLOOR RCP**
SCALE = 1 : 100

C:\SCHOOL\PORTFOLIO\PORTFOLIO AMBULANCE STATION (2).rvt

NAIT

SCHOOL OF CONSTRUCTION AND APPLIED BUILDING SCIENCE

ARCHITECTURAL TECHNOLOGY

CEILINGS AND EQUIPMENTS

- 1200 x 600 ACOUSTIC LAY-IN TILE SUSPENDED CEILING SYSTEM
- 600 x 600 ACOUSTIC LAY-IN TILE SUSPENDED CEILING SYSTEM
- GYPSUM BOARD SUSPENDED CEILING SYSTEM
- 1200 x 600 TROFFER PARABOLIC (2-LAMP) 120V LIGHT FIXTURE
- 600 x 600 TROFFER PARABOLIC (2-LAMP) 120V LIGHT FIXTURE
- 600 x 600 LFX PENDANT FB 120V LIGHT FIXTURE
- 152mm LFX DOWNLIGHT RECESSED CAN LED 120V
- 600 x 600 AIR DIFFUSER UH SUPPLY AIR
- 600 x 600 AIR DIFFUSER UH RETURN AIR
- **ES** EXPOSED STRUCTURE

No.	Description	Date

NAIT AMBULANCE HEADQUARTERS

SECOND & THIRD FLOOR REFLECTED CEILING PLAN

Class Number	A03
Date	23/03/2026
Drawn by	CHIDERA UZO
Instructor	ANDRE LUCENA
	A2.5
Scale	1 : 100