[illegible]

BLUE PARROT RESTAURANT

WALL SECTIONS

Class Number **COMP2330 A03**


Date FEB 2025

Drawn by **CHIDERA UZO**


Instructor **BOBBY HARRIS**

A4.1


Scale 1 : 25

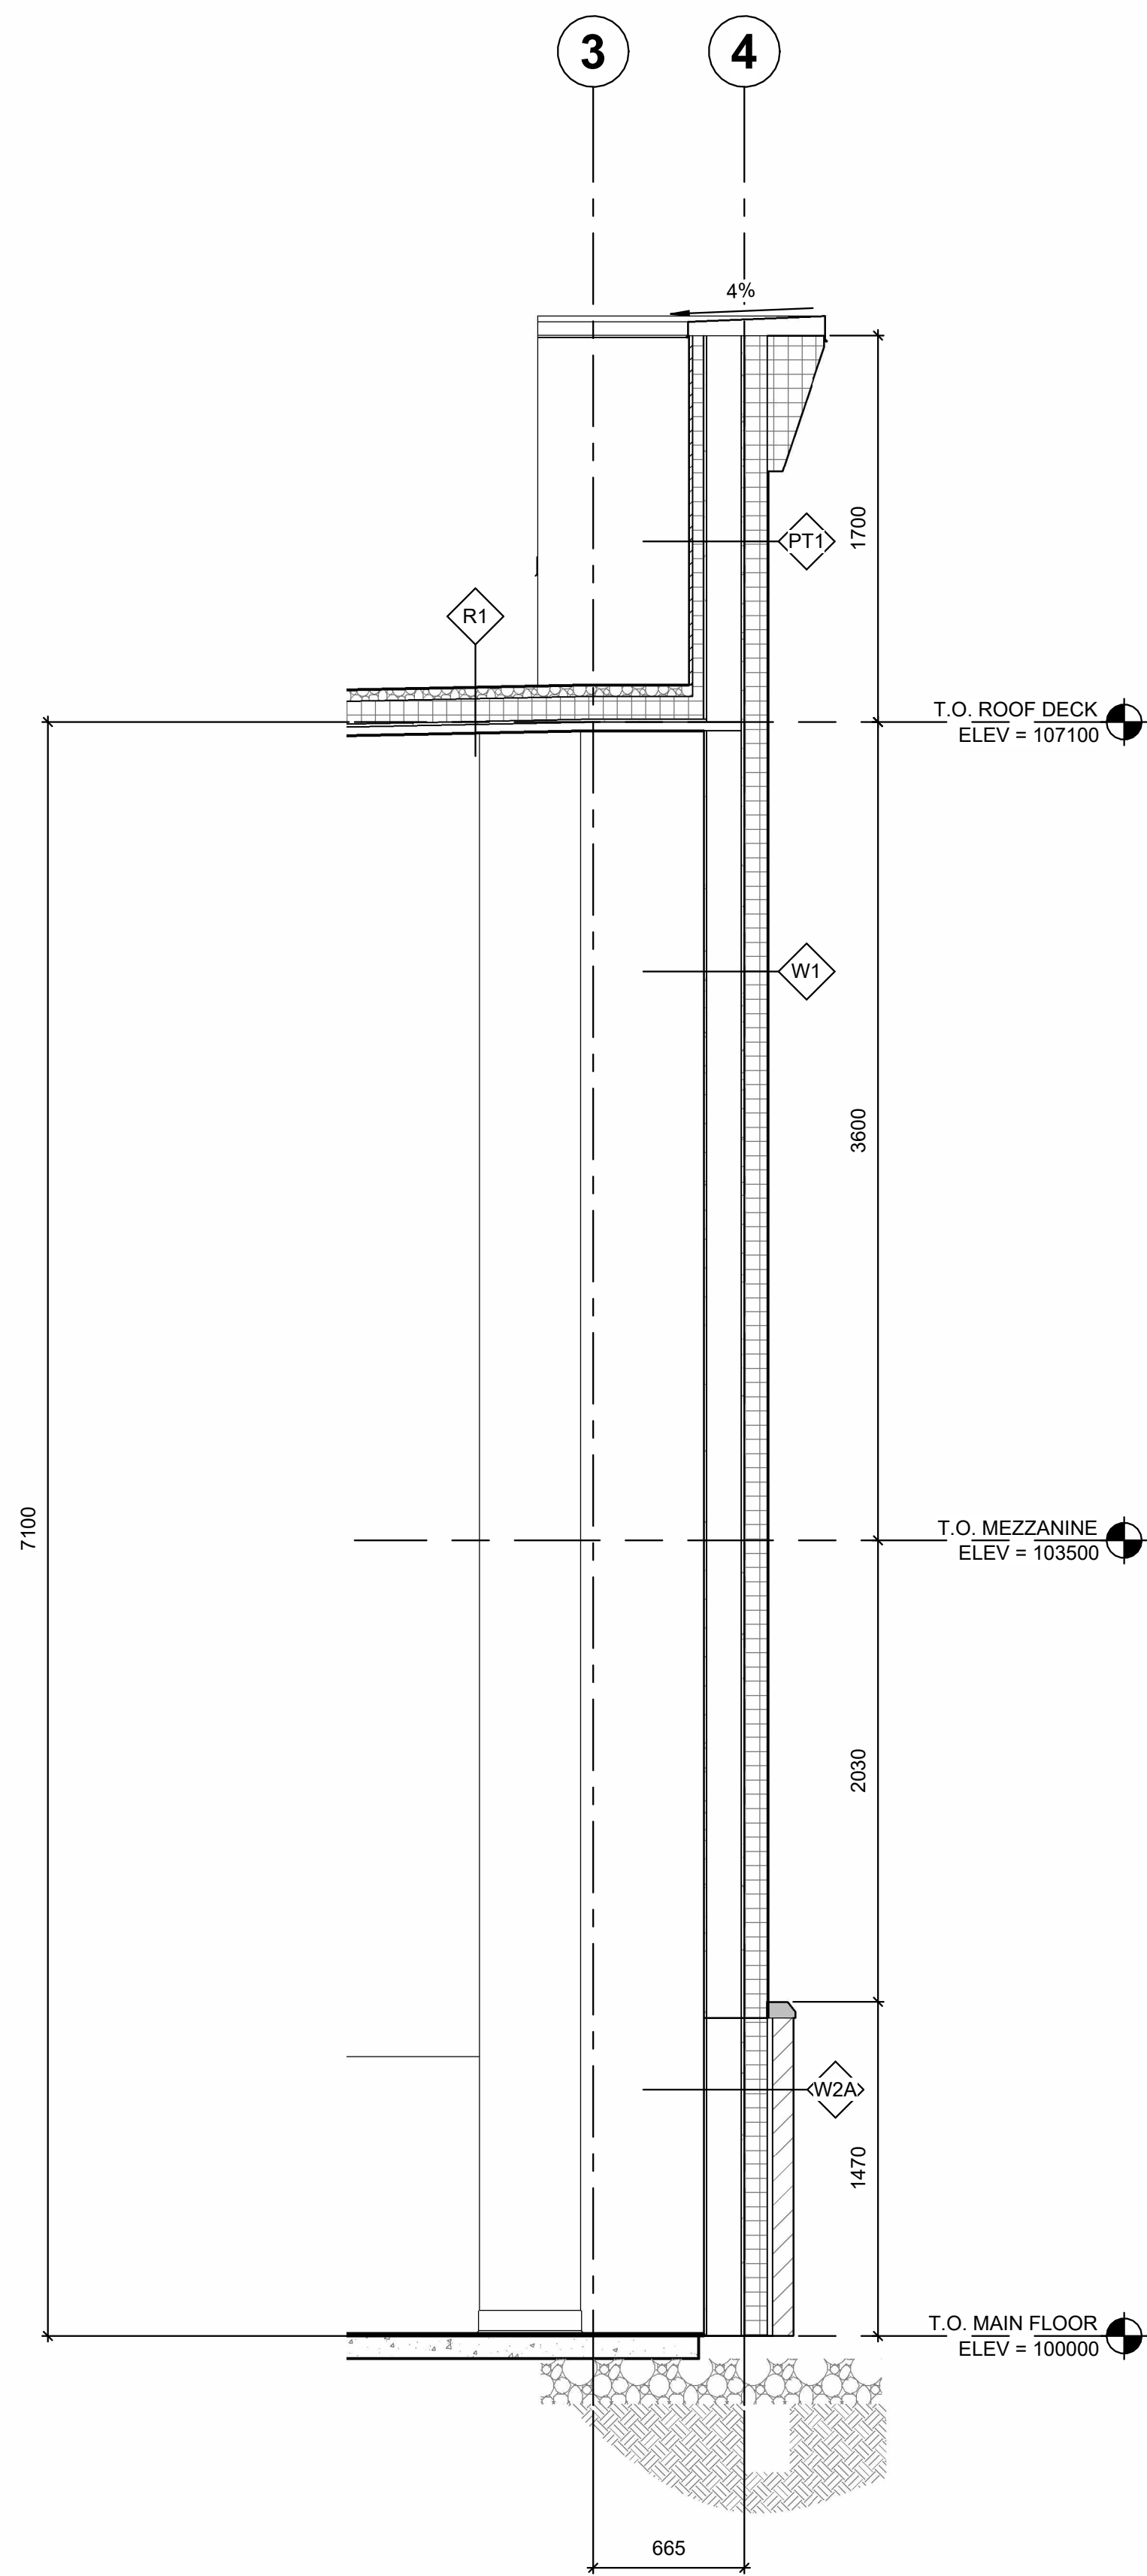

1 WALL SECTION

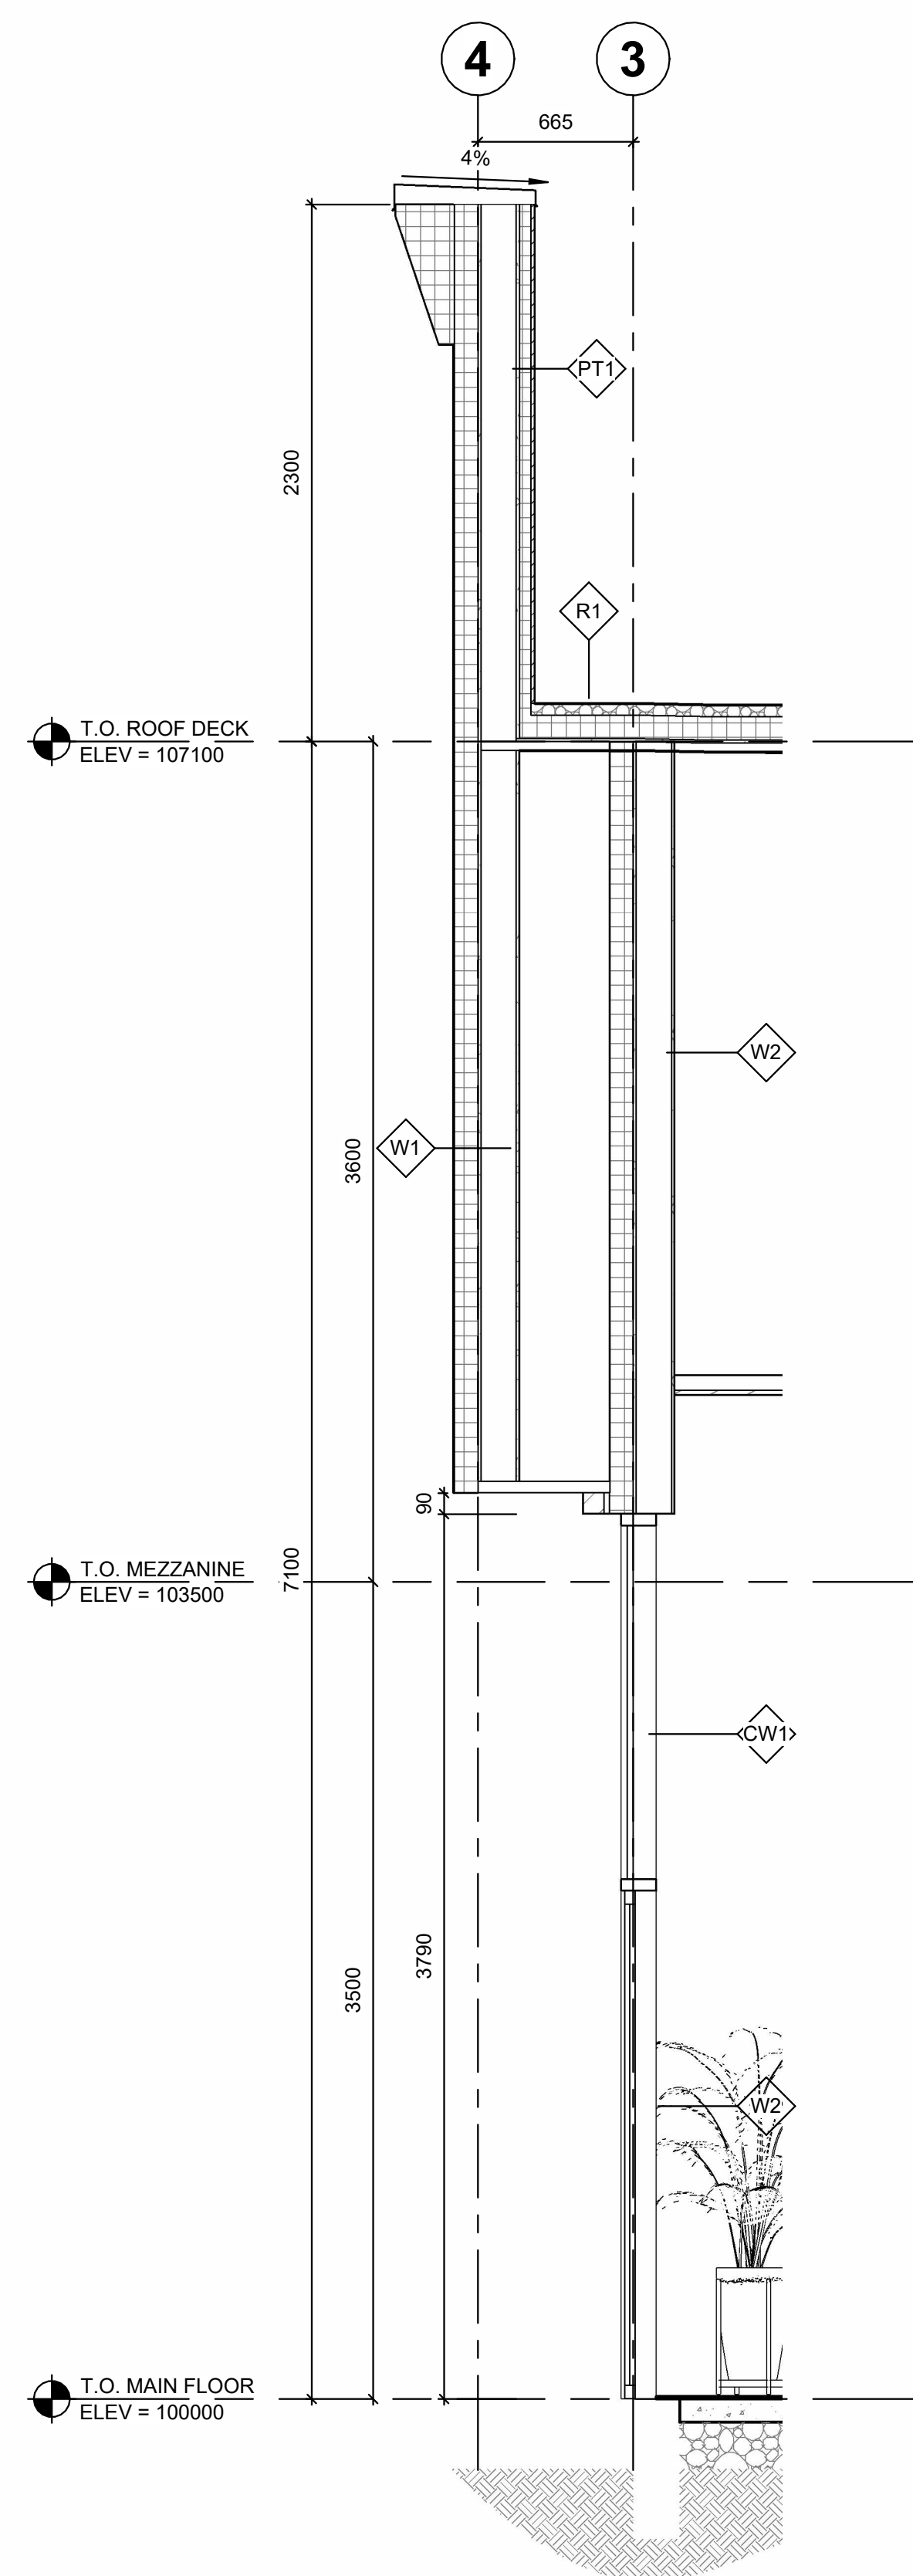

2 WALL SECTION
A4.1 SCALE = 1 : 25

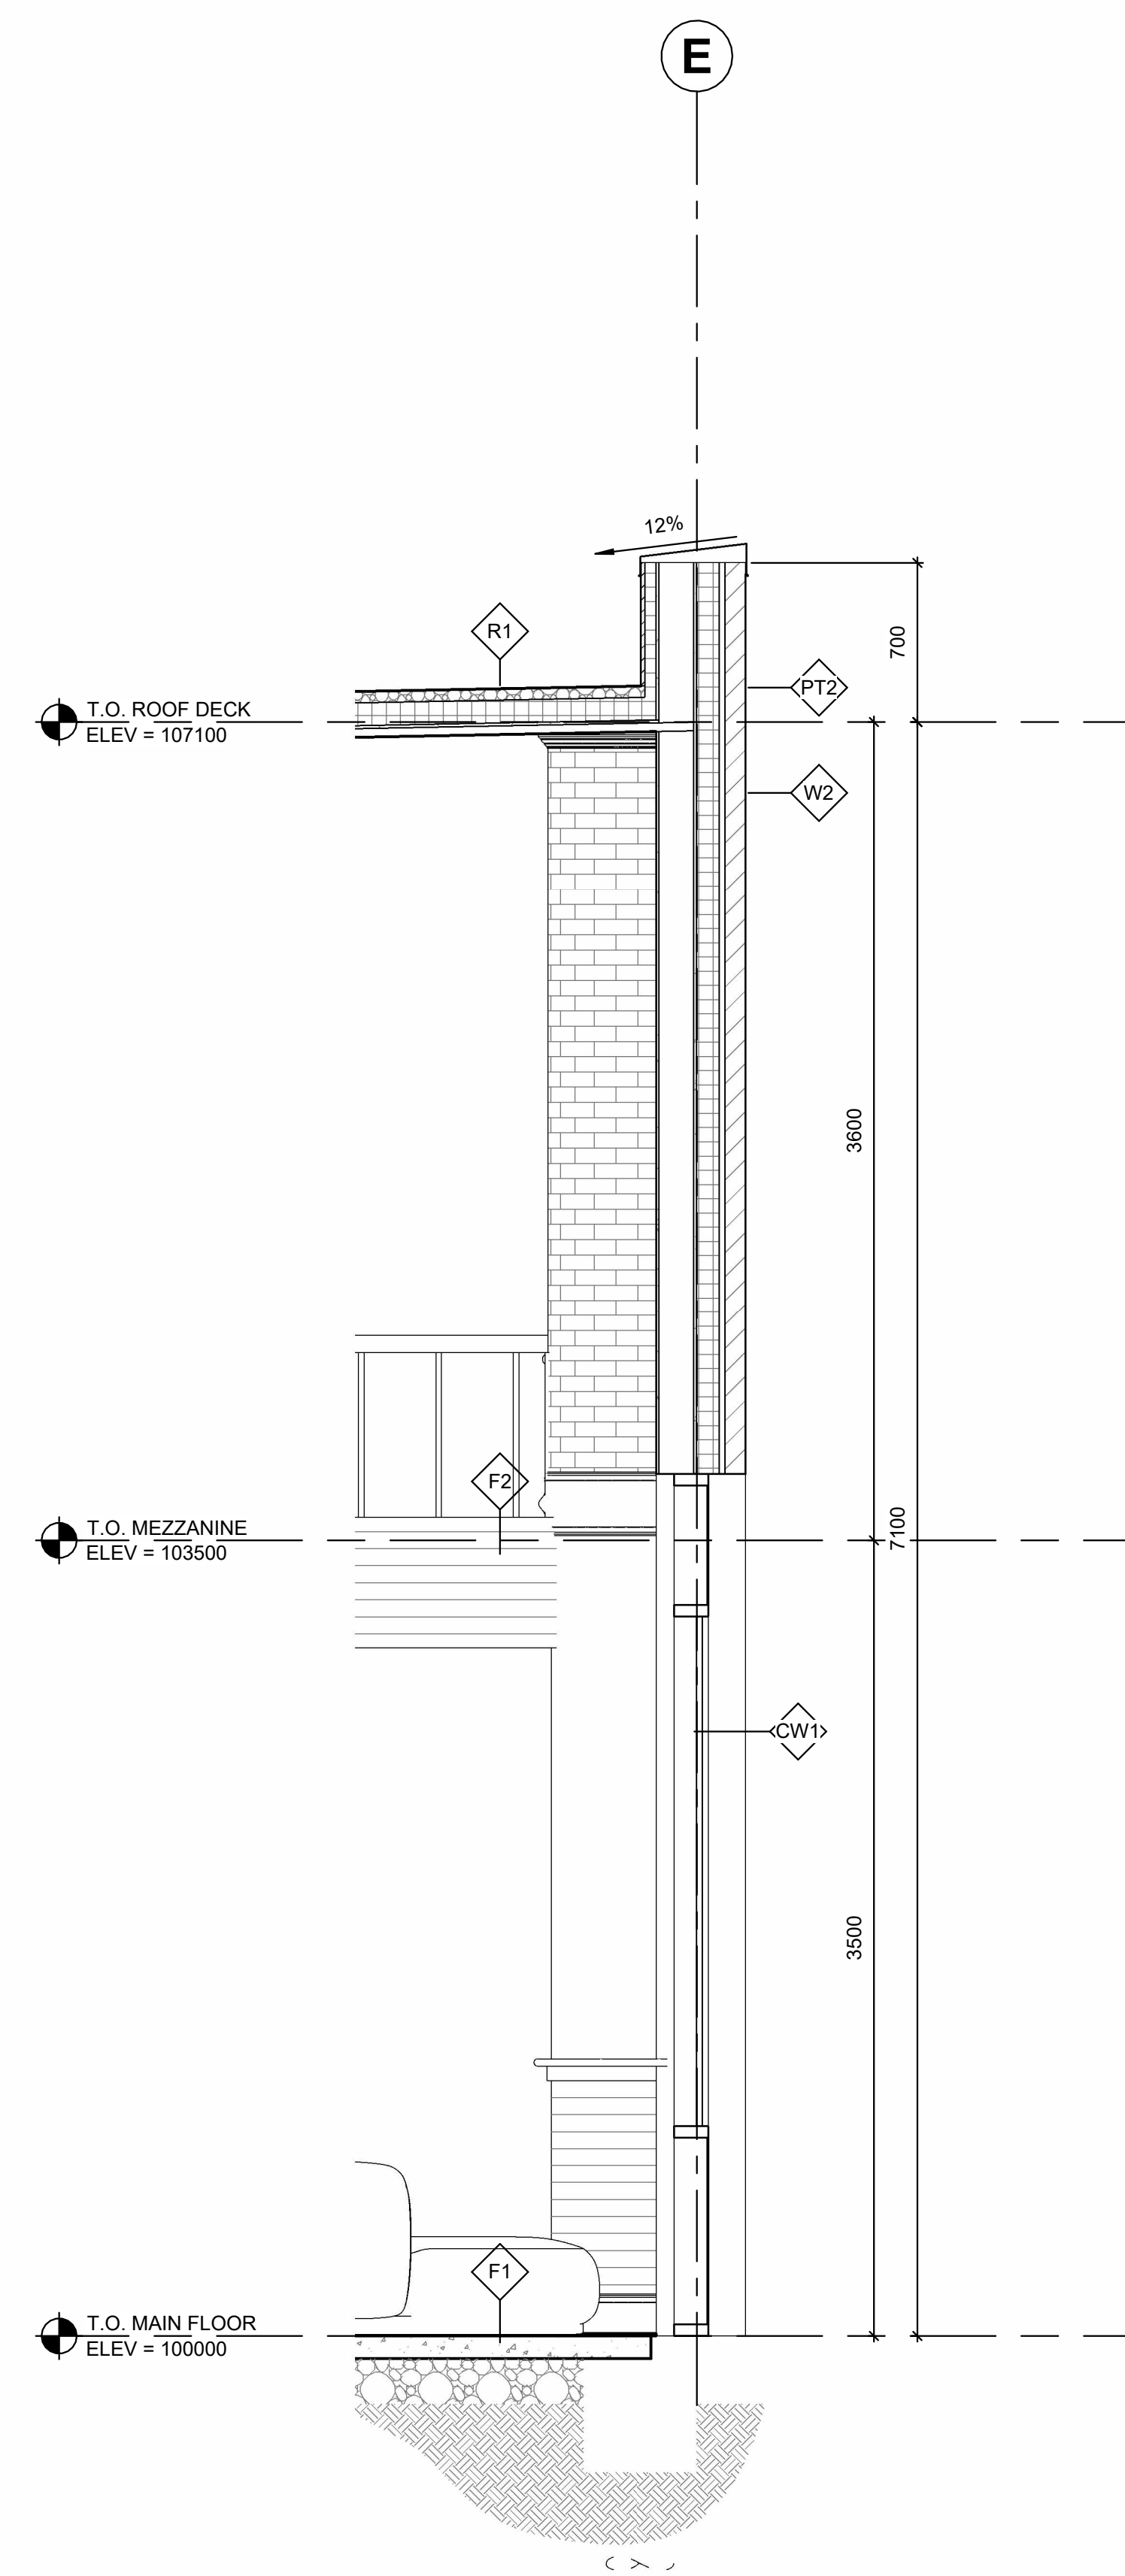

3 WALL SECTION