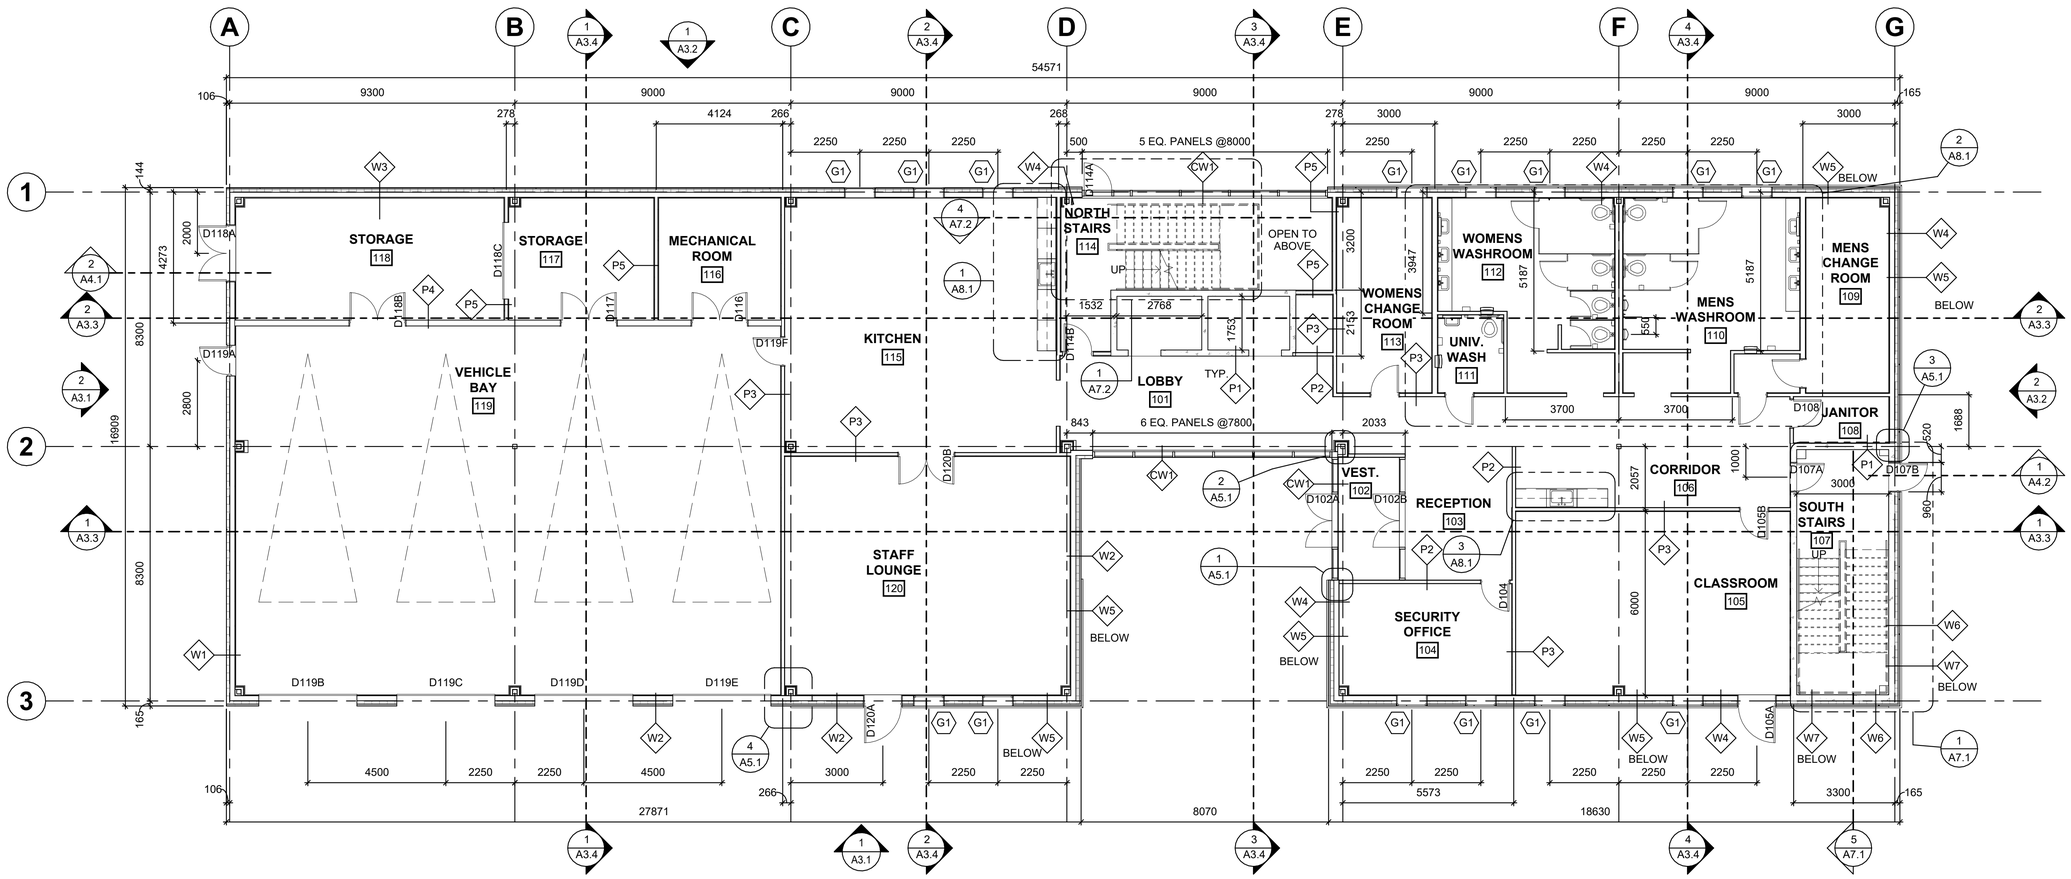

1 A2.1 **MAIN FLOOR PLAN**
SCALE = 1 : 100

NAIT

SCHOOL OF CONSTRUCTION AND APPLIED BUILDING SCIENCE

ARCHITECTURAL TECHNOLOGY

No.	Description	Date

NAIT AMBULANCE HEADQUATERS

MAIN FLOOR PLAN

Class Number	A03
Date	23/03/2026
Drawn by	CHIDERA UZO
Instructor	ANDRE LUCENA
	A2.1
Scale	1 : 100

C:\SCHOOL\CDOC 2600 - Architectural Construction Documents\UZO-2600 CDOC AMBULANCE STATION.rvt