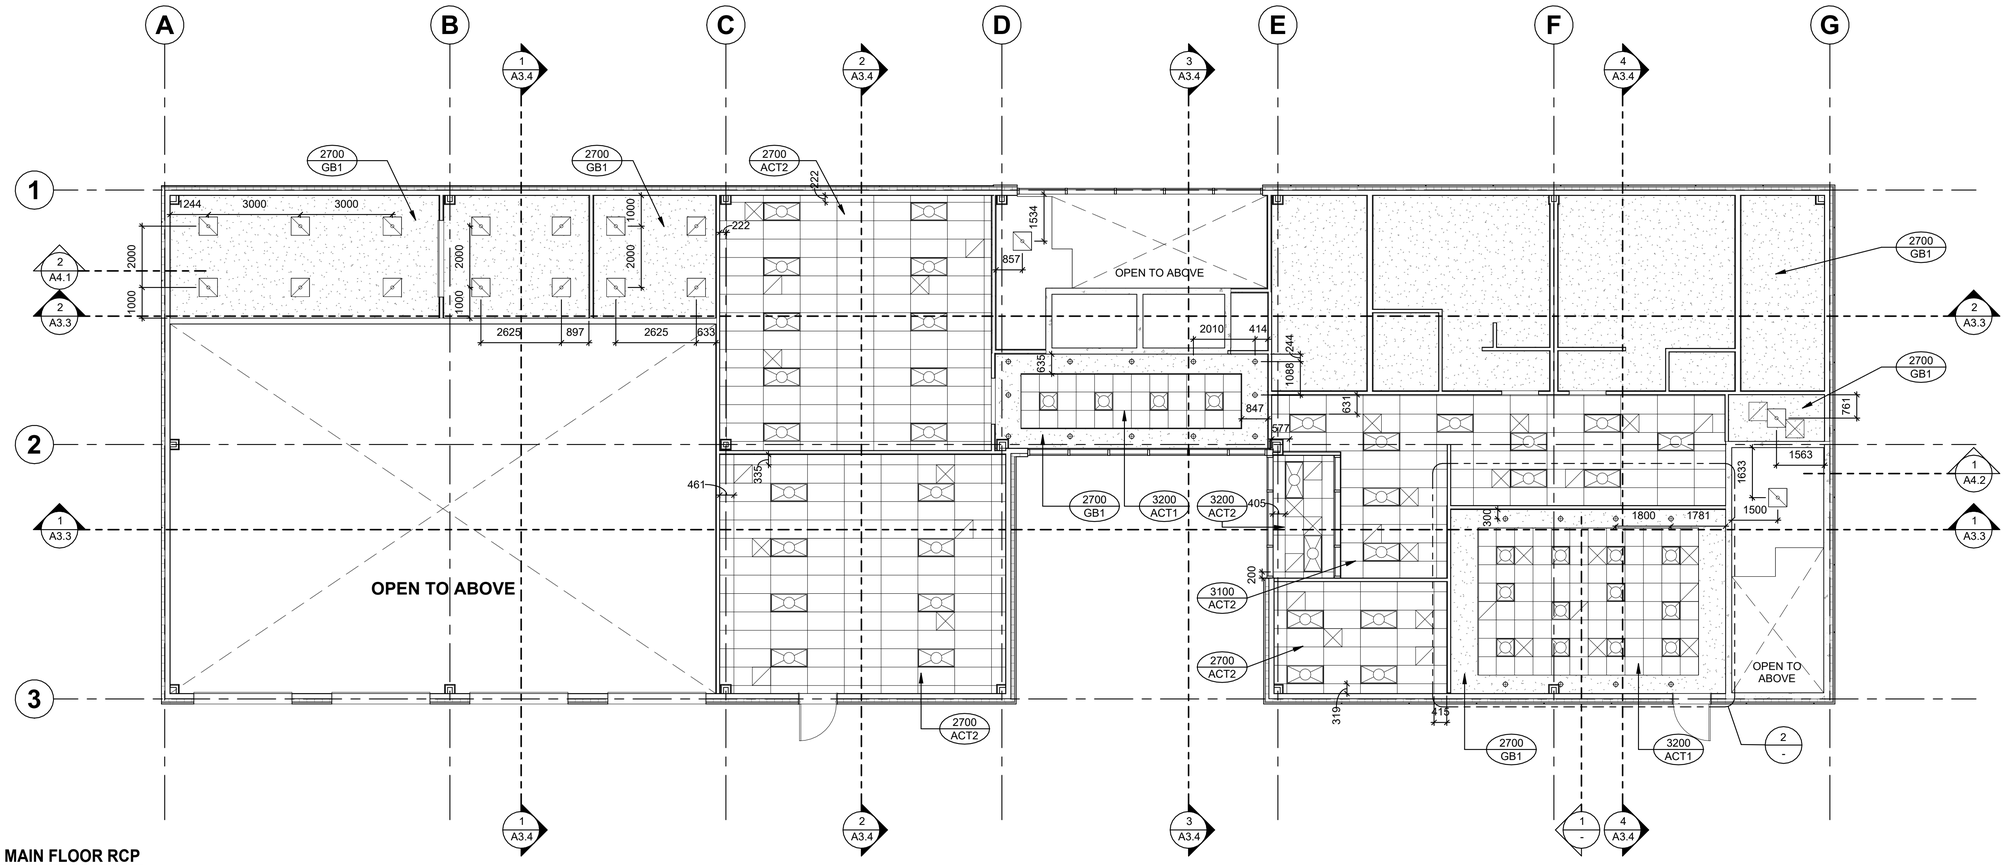


1 A2.4 **MAIN FLOOR RCP**

SCALE = 1 : 100

SCHOOL OF CONSTRUCTION AND APPLIED BUILDING SCIENCE

ARCHITECTURAL TECHNOLOGY

## CEILINGS AND EQUIPMENTS

- 1200 x 600 ACOUSTIC LAY-IN TILE SUSPENDED CEILING SYSTEM
- 600 x 600 ACOUSTIC LAY-IN TILE SUSPENDED CEILING SYSTEM
- GYPSUM BOARD SUSPENDED CEILING SYSTEM
- 1200 x 600 TROFFER PARABOLIC (2-LAMP) 120V LIGHT FIXTURE
- 600 x 600 TROFFER PARABOLIC (2-LAMP) 120V LIGHT FIXTURE
- 600 x 600 LFX PENDANT FB 120V LIGHT FIXTURE
- 152mm LFX DOWNLIGHT RECESSED CAN LED 120V
- 600 x 600 AIR DIFFUSER UH SUPPLY AIR
- 600 x 600 AIR DIFFUSER UH RETURN AIR
- **ES** EXPOSED STRUCTURE

| No. | Description | Date |
|---|---|---|
| | | |

# NAIT AMBULANCE HEADQUATERS

## MAIN FLOOR REFLECTED CEILING PLAN

| | |
|---|---|
| Class Number | A03 |
| Date | 23/03/2026 |
| Drawn by | CHIDERA UZO |
| Instructor | ANDRE LUCENA |
| | A2.4 |
| Scale | 1 : 100 |

C:\SCHOOL\PORTFOLIO\PORTFOLIO AMBULANCE STATION.rvt