



SCHOOL OF APPLIED
SCIENCE AND TECHNOLOGY
ARCHITECTURAL TECHNOLOGY

CONSULTANTS

NOTES

REVISIONS

No.	DATE	DESCRIPTION
-----	------	-------------

PROJECT

FINAL DETAIL SHEET

DRAWING

CORRECTED DETAILS FOR
EXERCISES 2, 9 & 10

DESIGNED BY: NAIT

CHECKED BY: MELISSA PRICE

DRAWN BY: CHIDERA UZO

DATE: 23/04/2026

COURSE: CDOC 2611

CLASS: A03

INSTRUCTOR: MELISSA PRICE

SCALE: VARIES

SET: A7 / 5


PROJECT No:

PROJ. No.


CAD FILE:

SHEET No:

A7

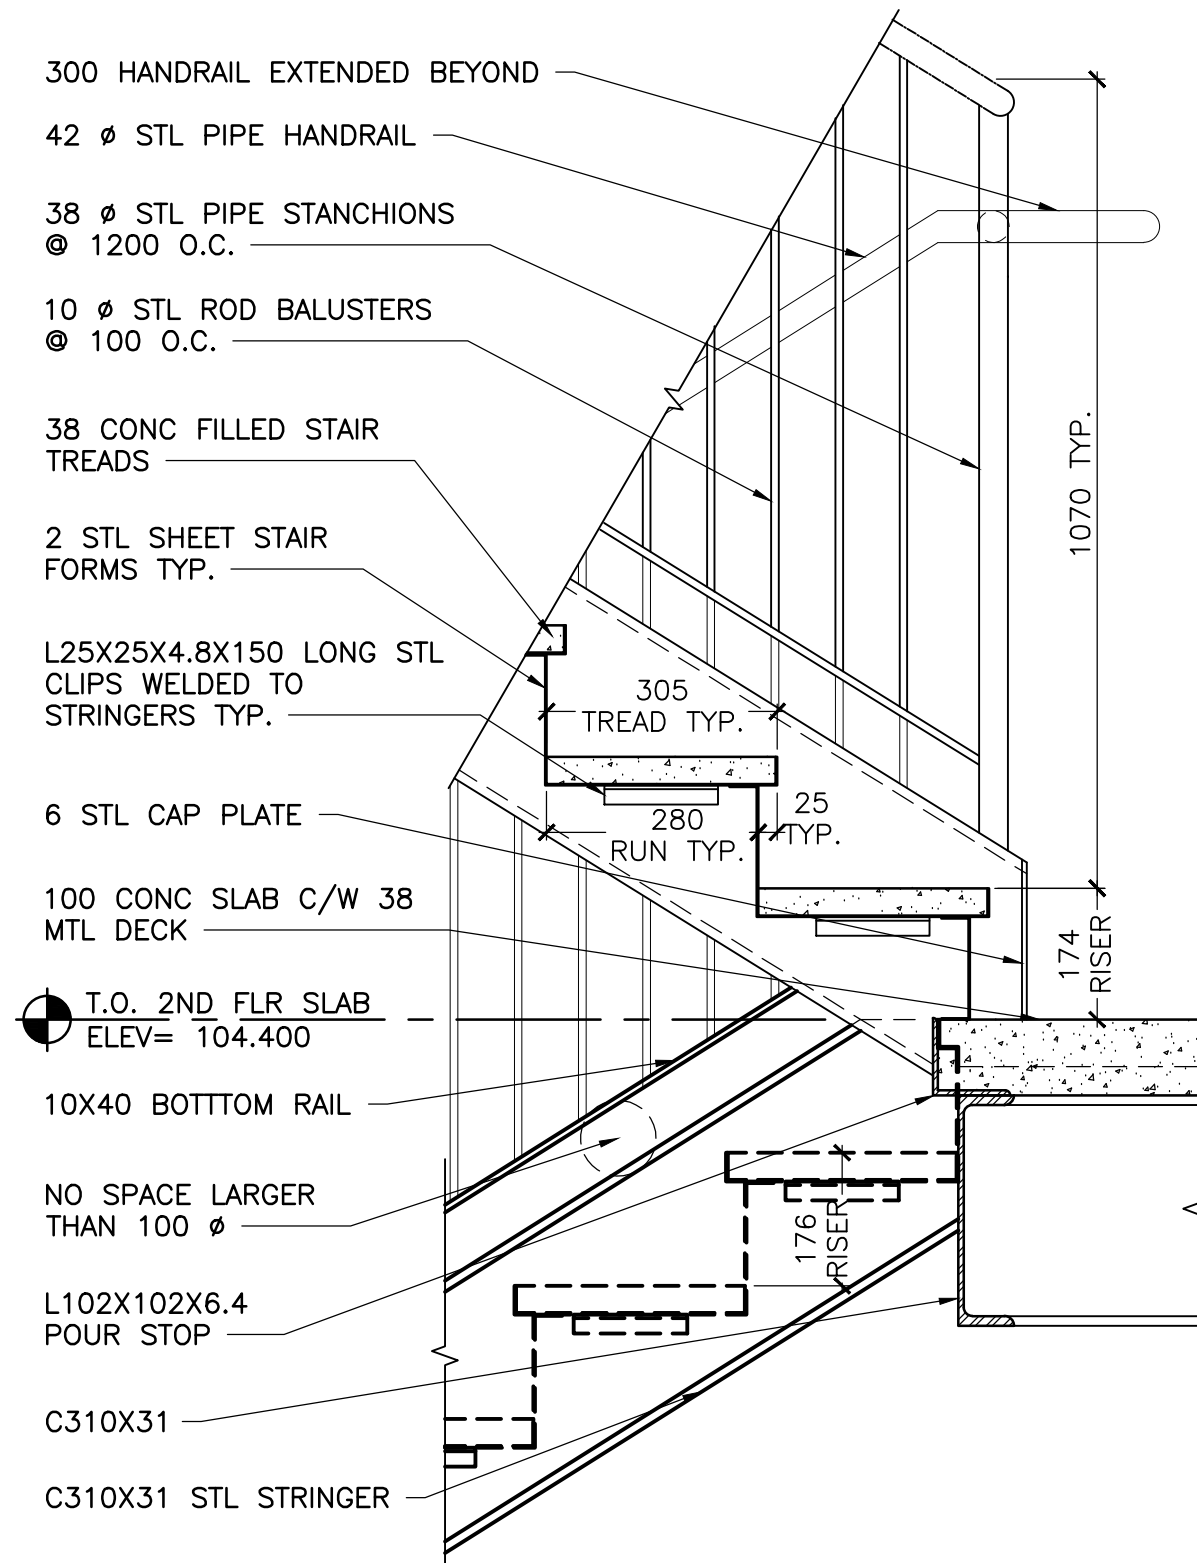


1 SECTION DETAIL
A7 SCALE = 1:10

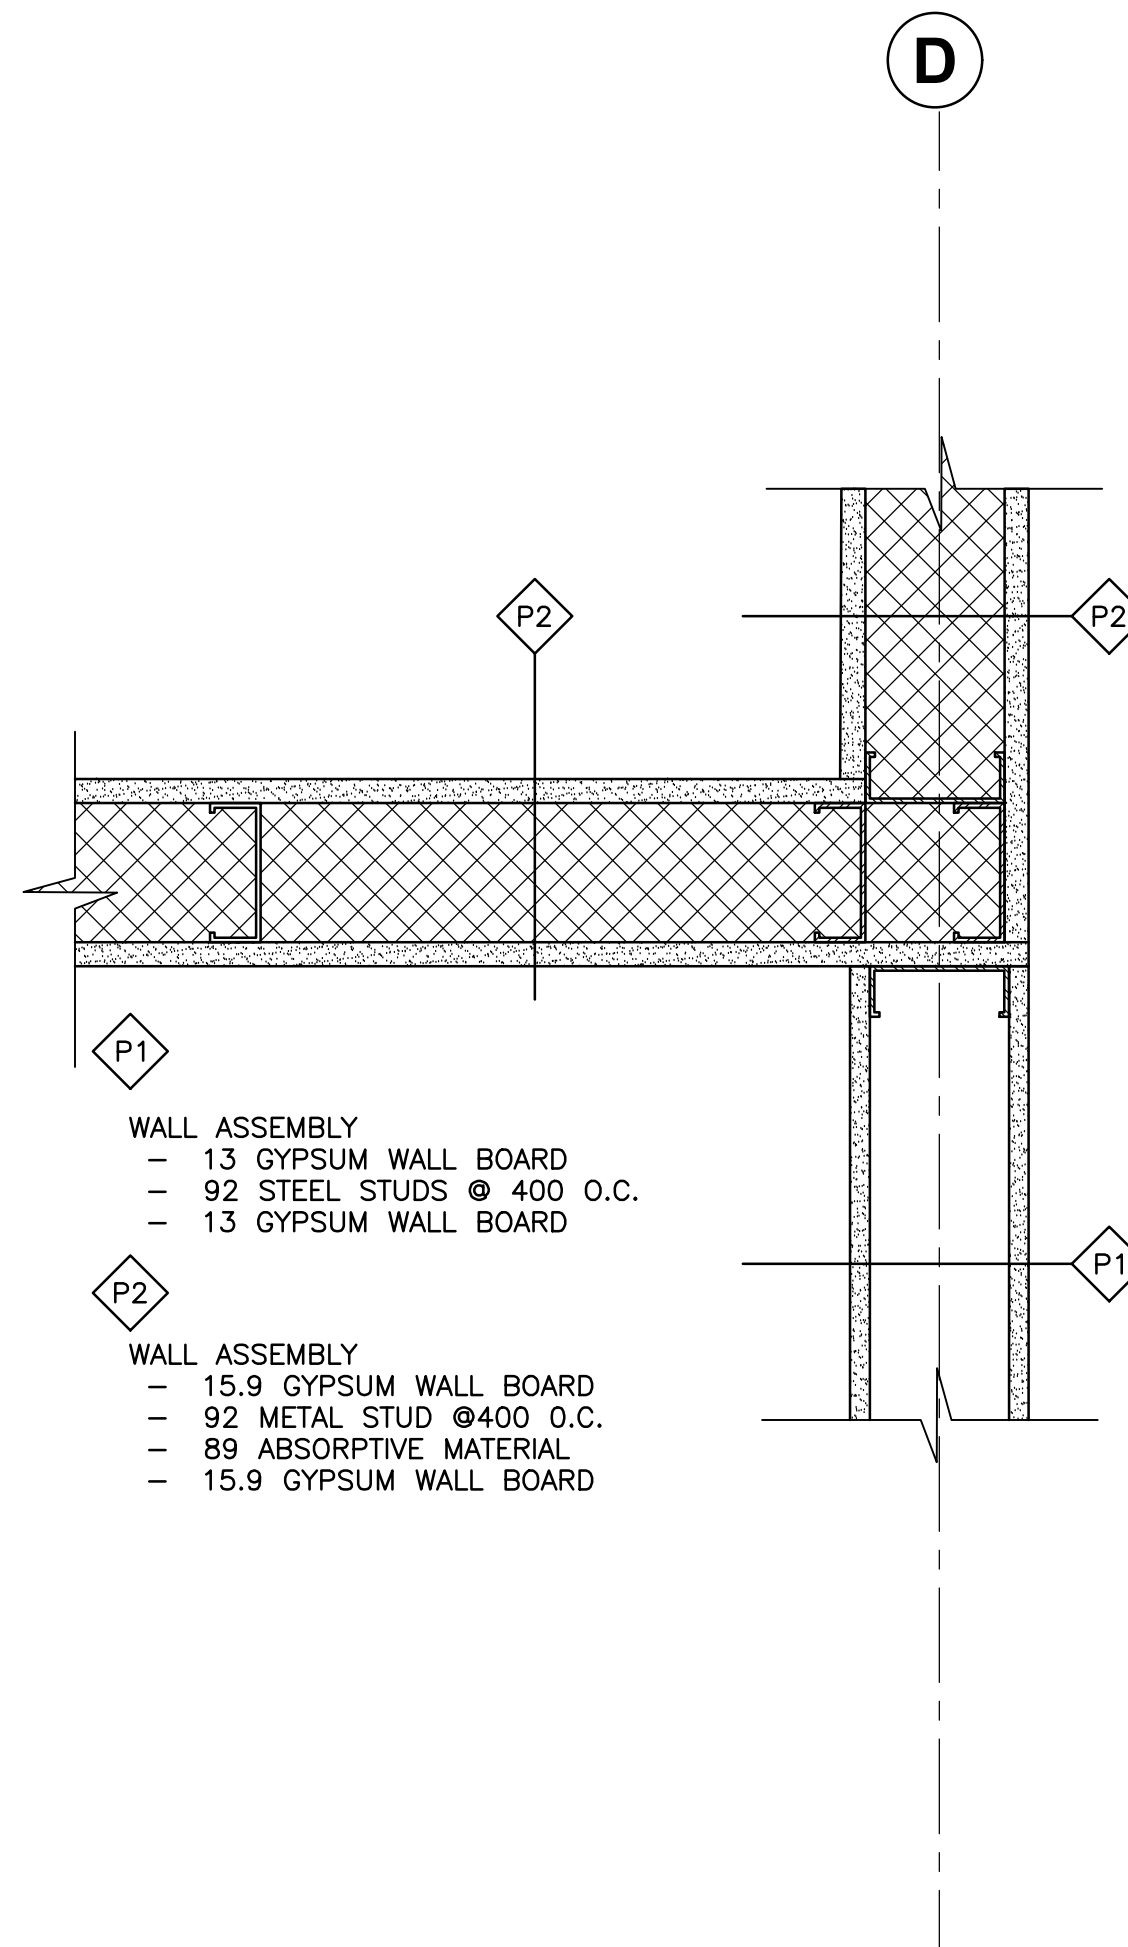


2 PLAN DETAIL 1
A7 SCALE = 1:5


M/D RATIO:
W250x39 BEAM
MASS: 39 KG/M
PERIMETER: 2*(0.147+0.262)= 0.818m
M/D = 39/0.818
=47.67
ACCORDING TO TABLE, 2-H
RATING WALL MIN. THICKNESS IS 41.3
= 3 LAYERS GYPSUM(2-12.7+ 15.9)

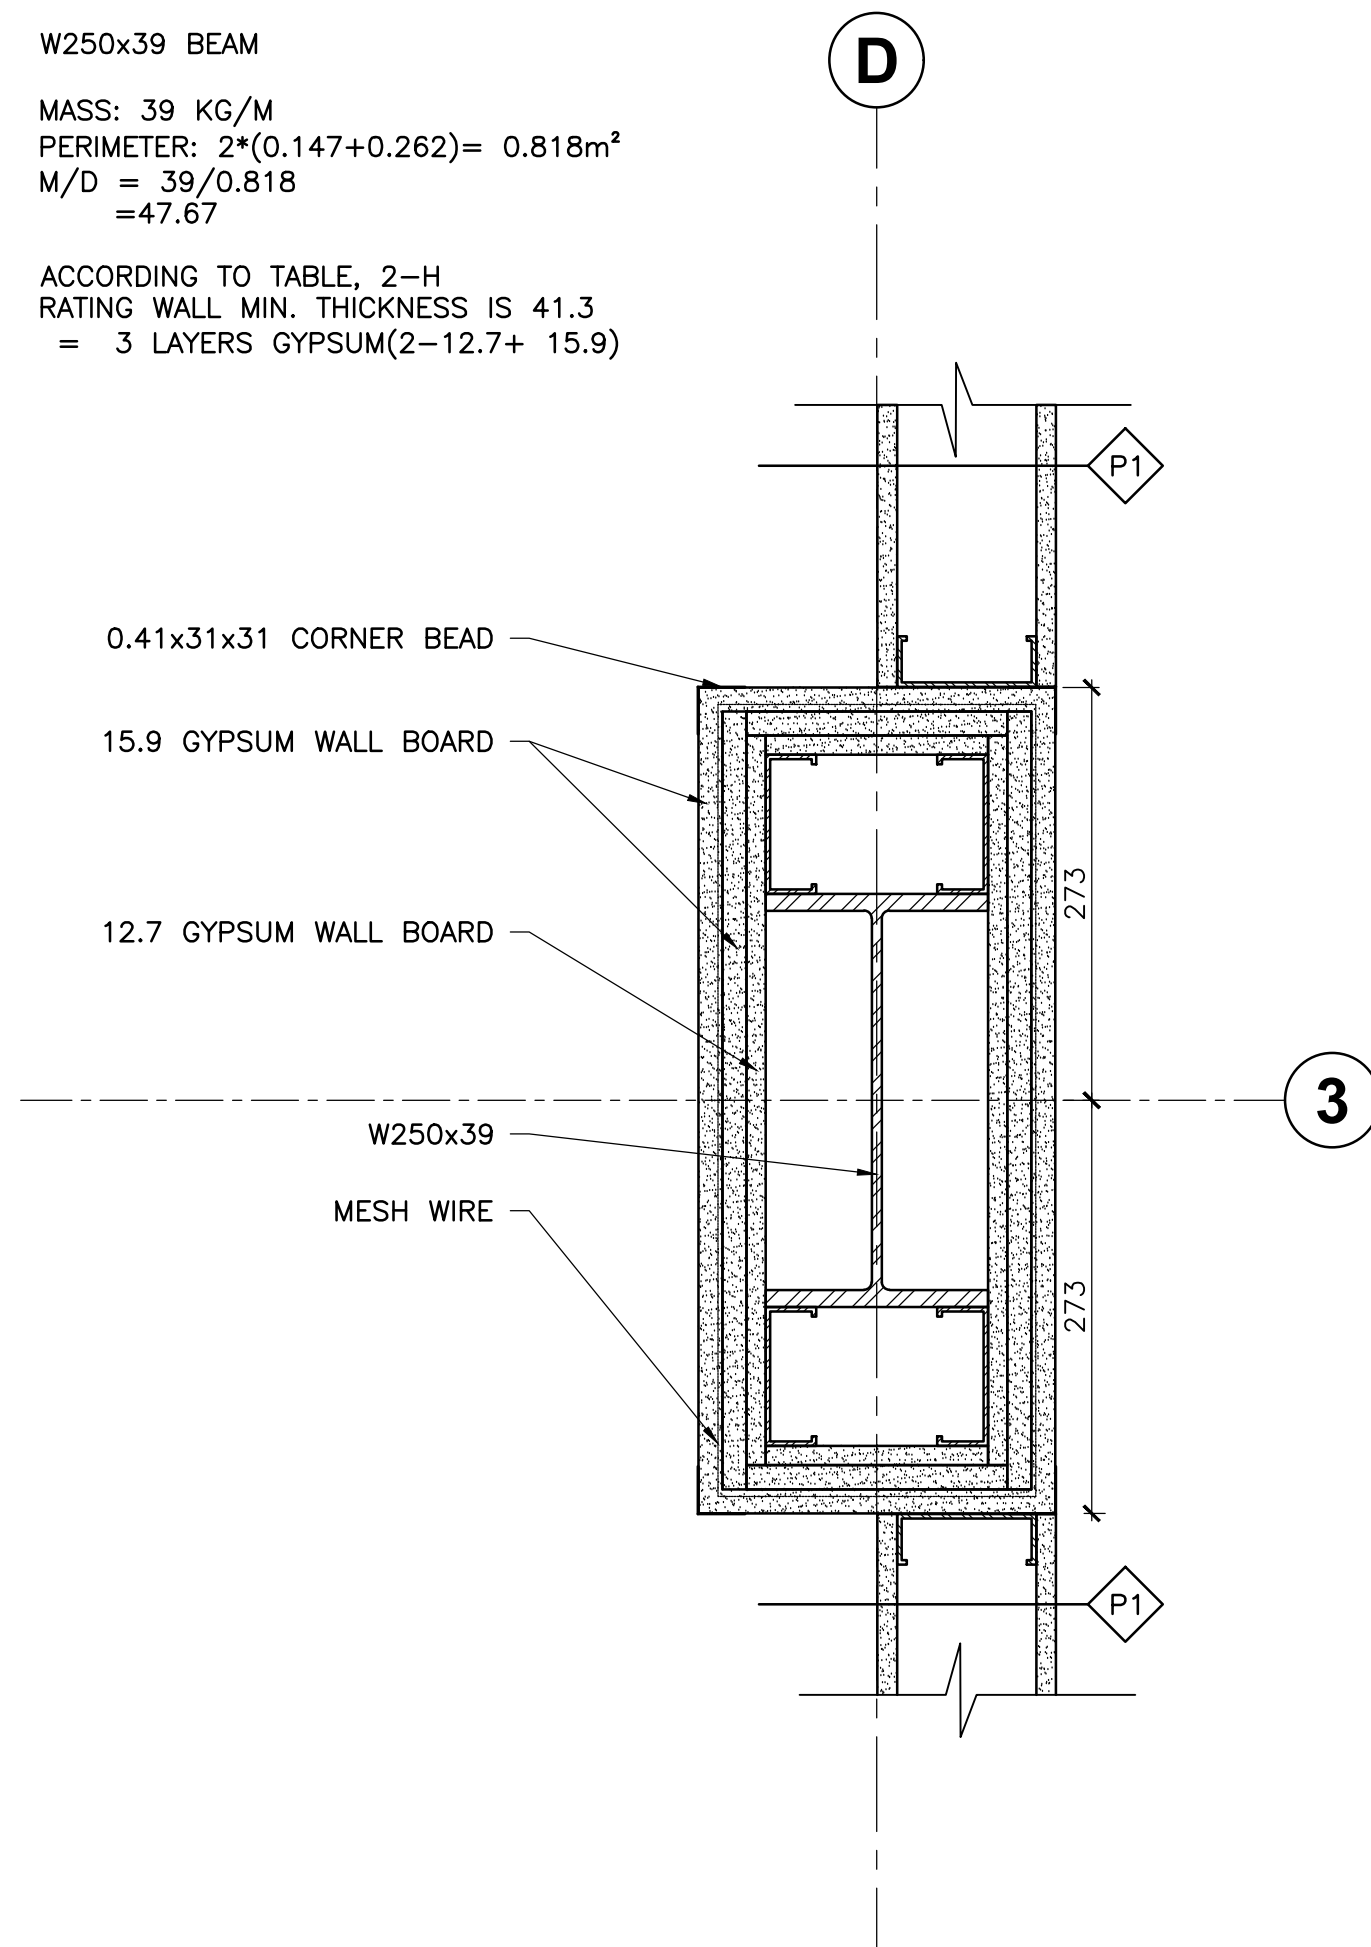

3 2-HR FIRE RATED COLUMN DETAIL
A7 SCALE = 1:5

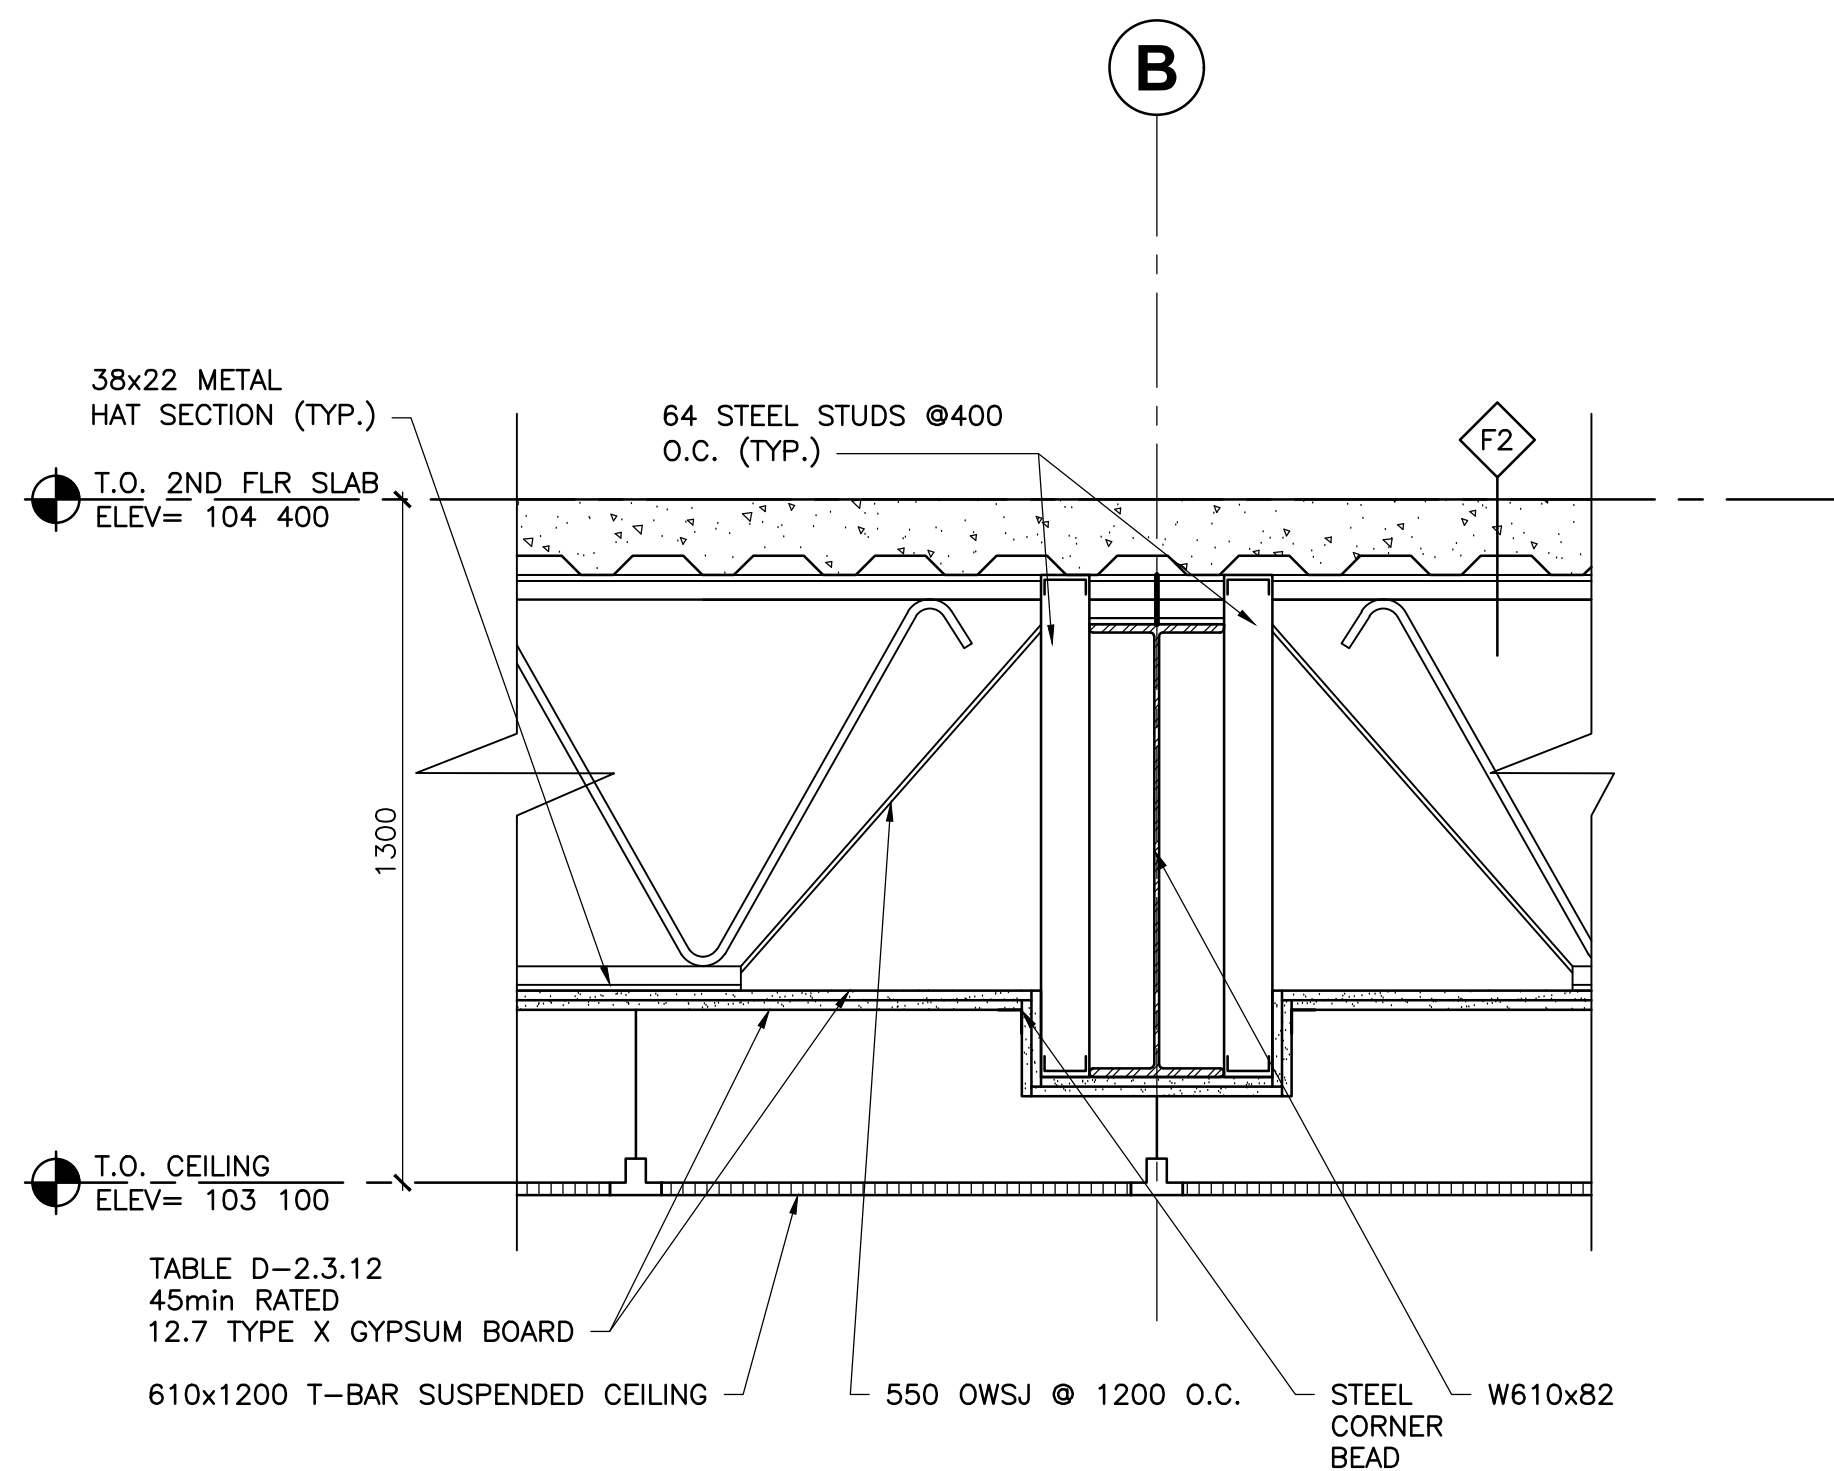

4 SECTION DETAIL @2ND FLOOR
A7 SCALE = 1:10

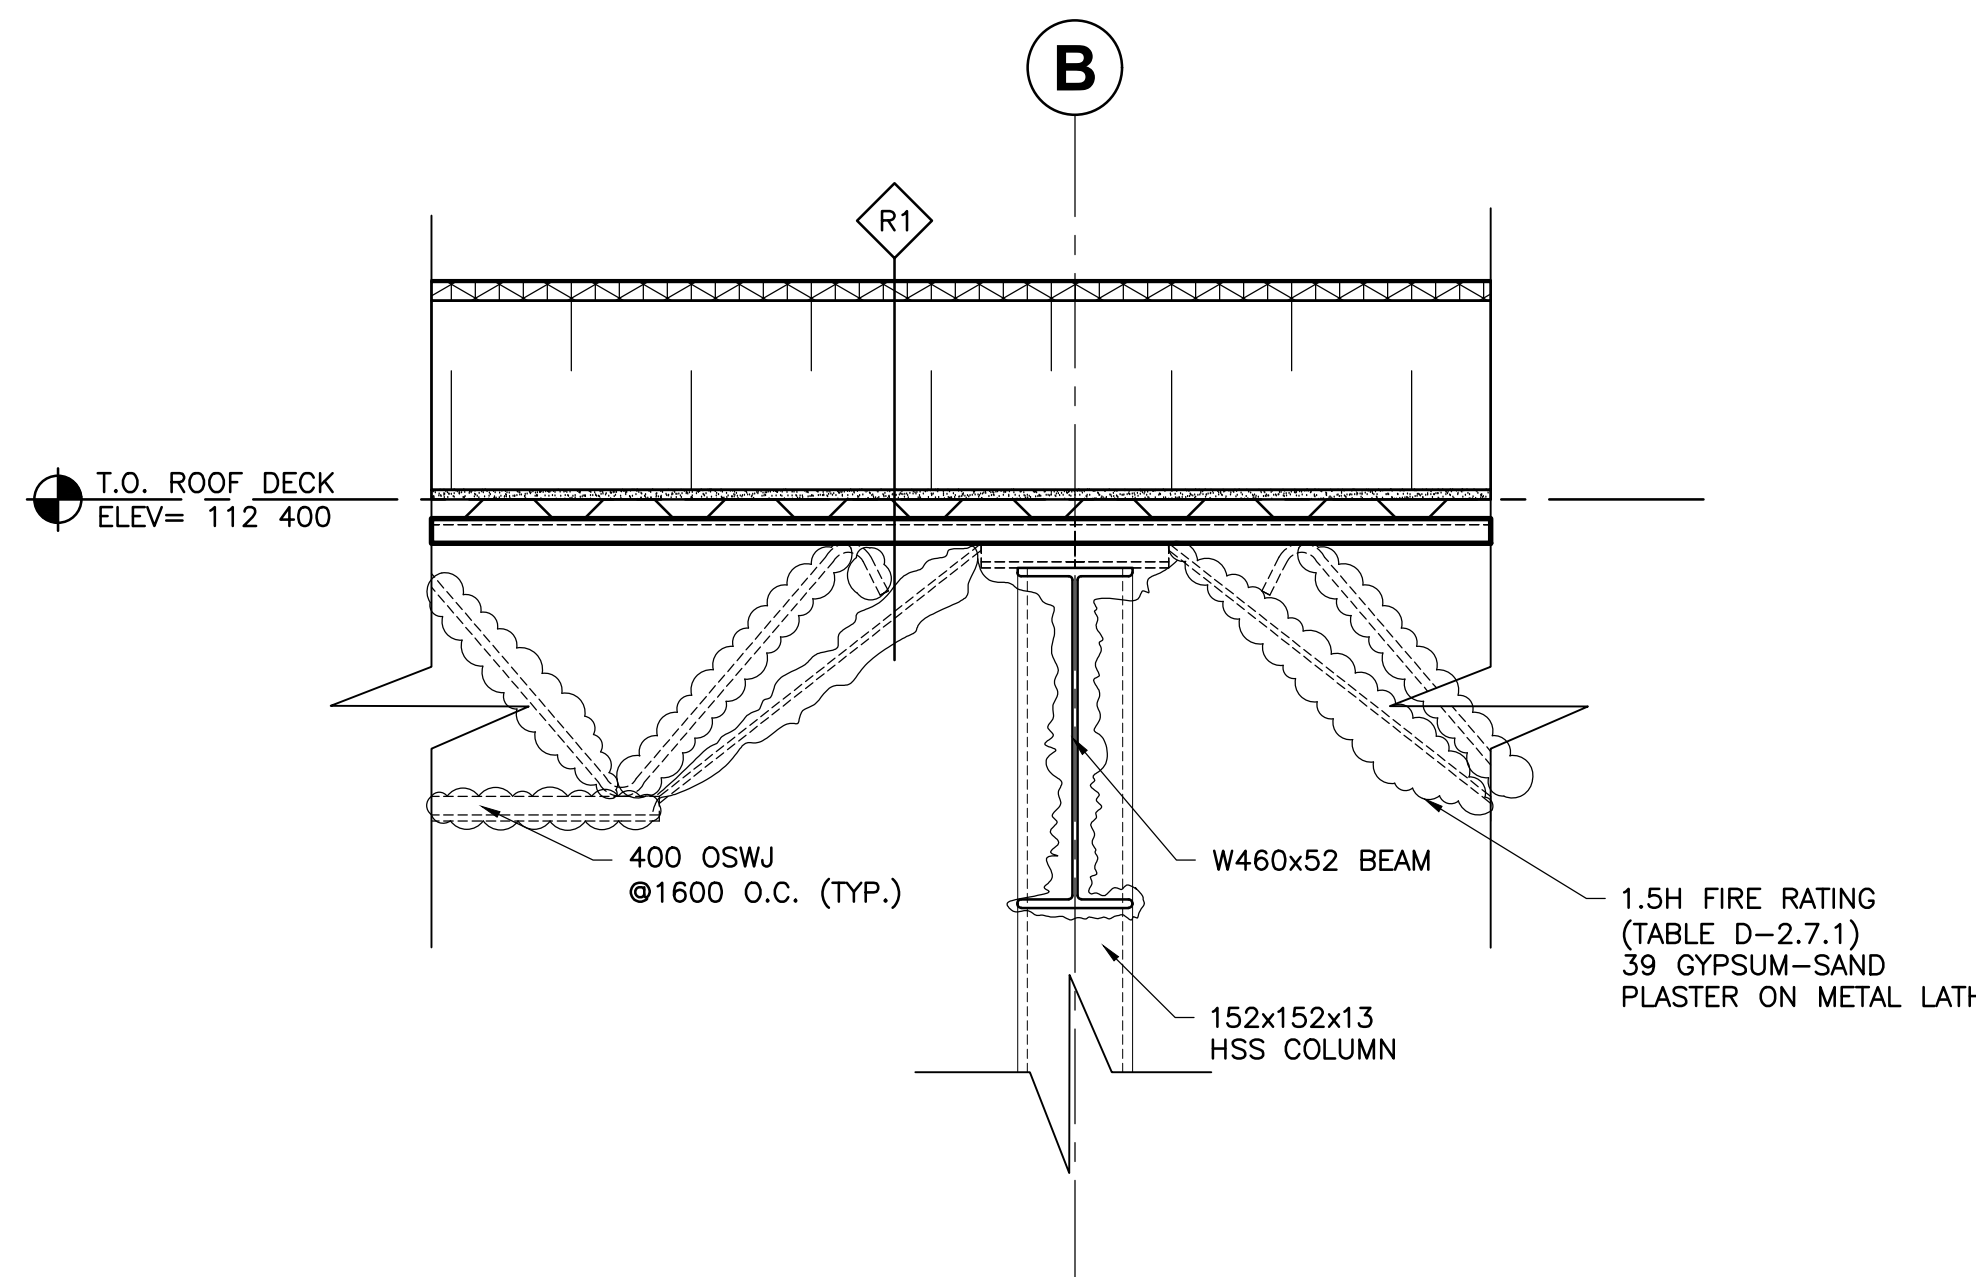

5 SECTION DETAIL @ROOF
A7 SCALE = 1:10