


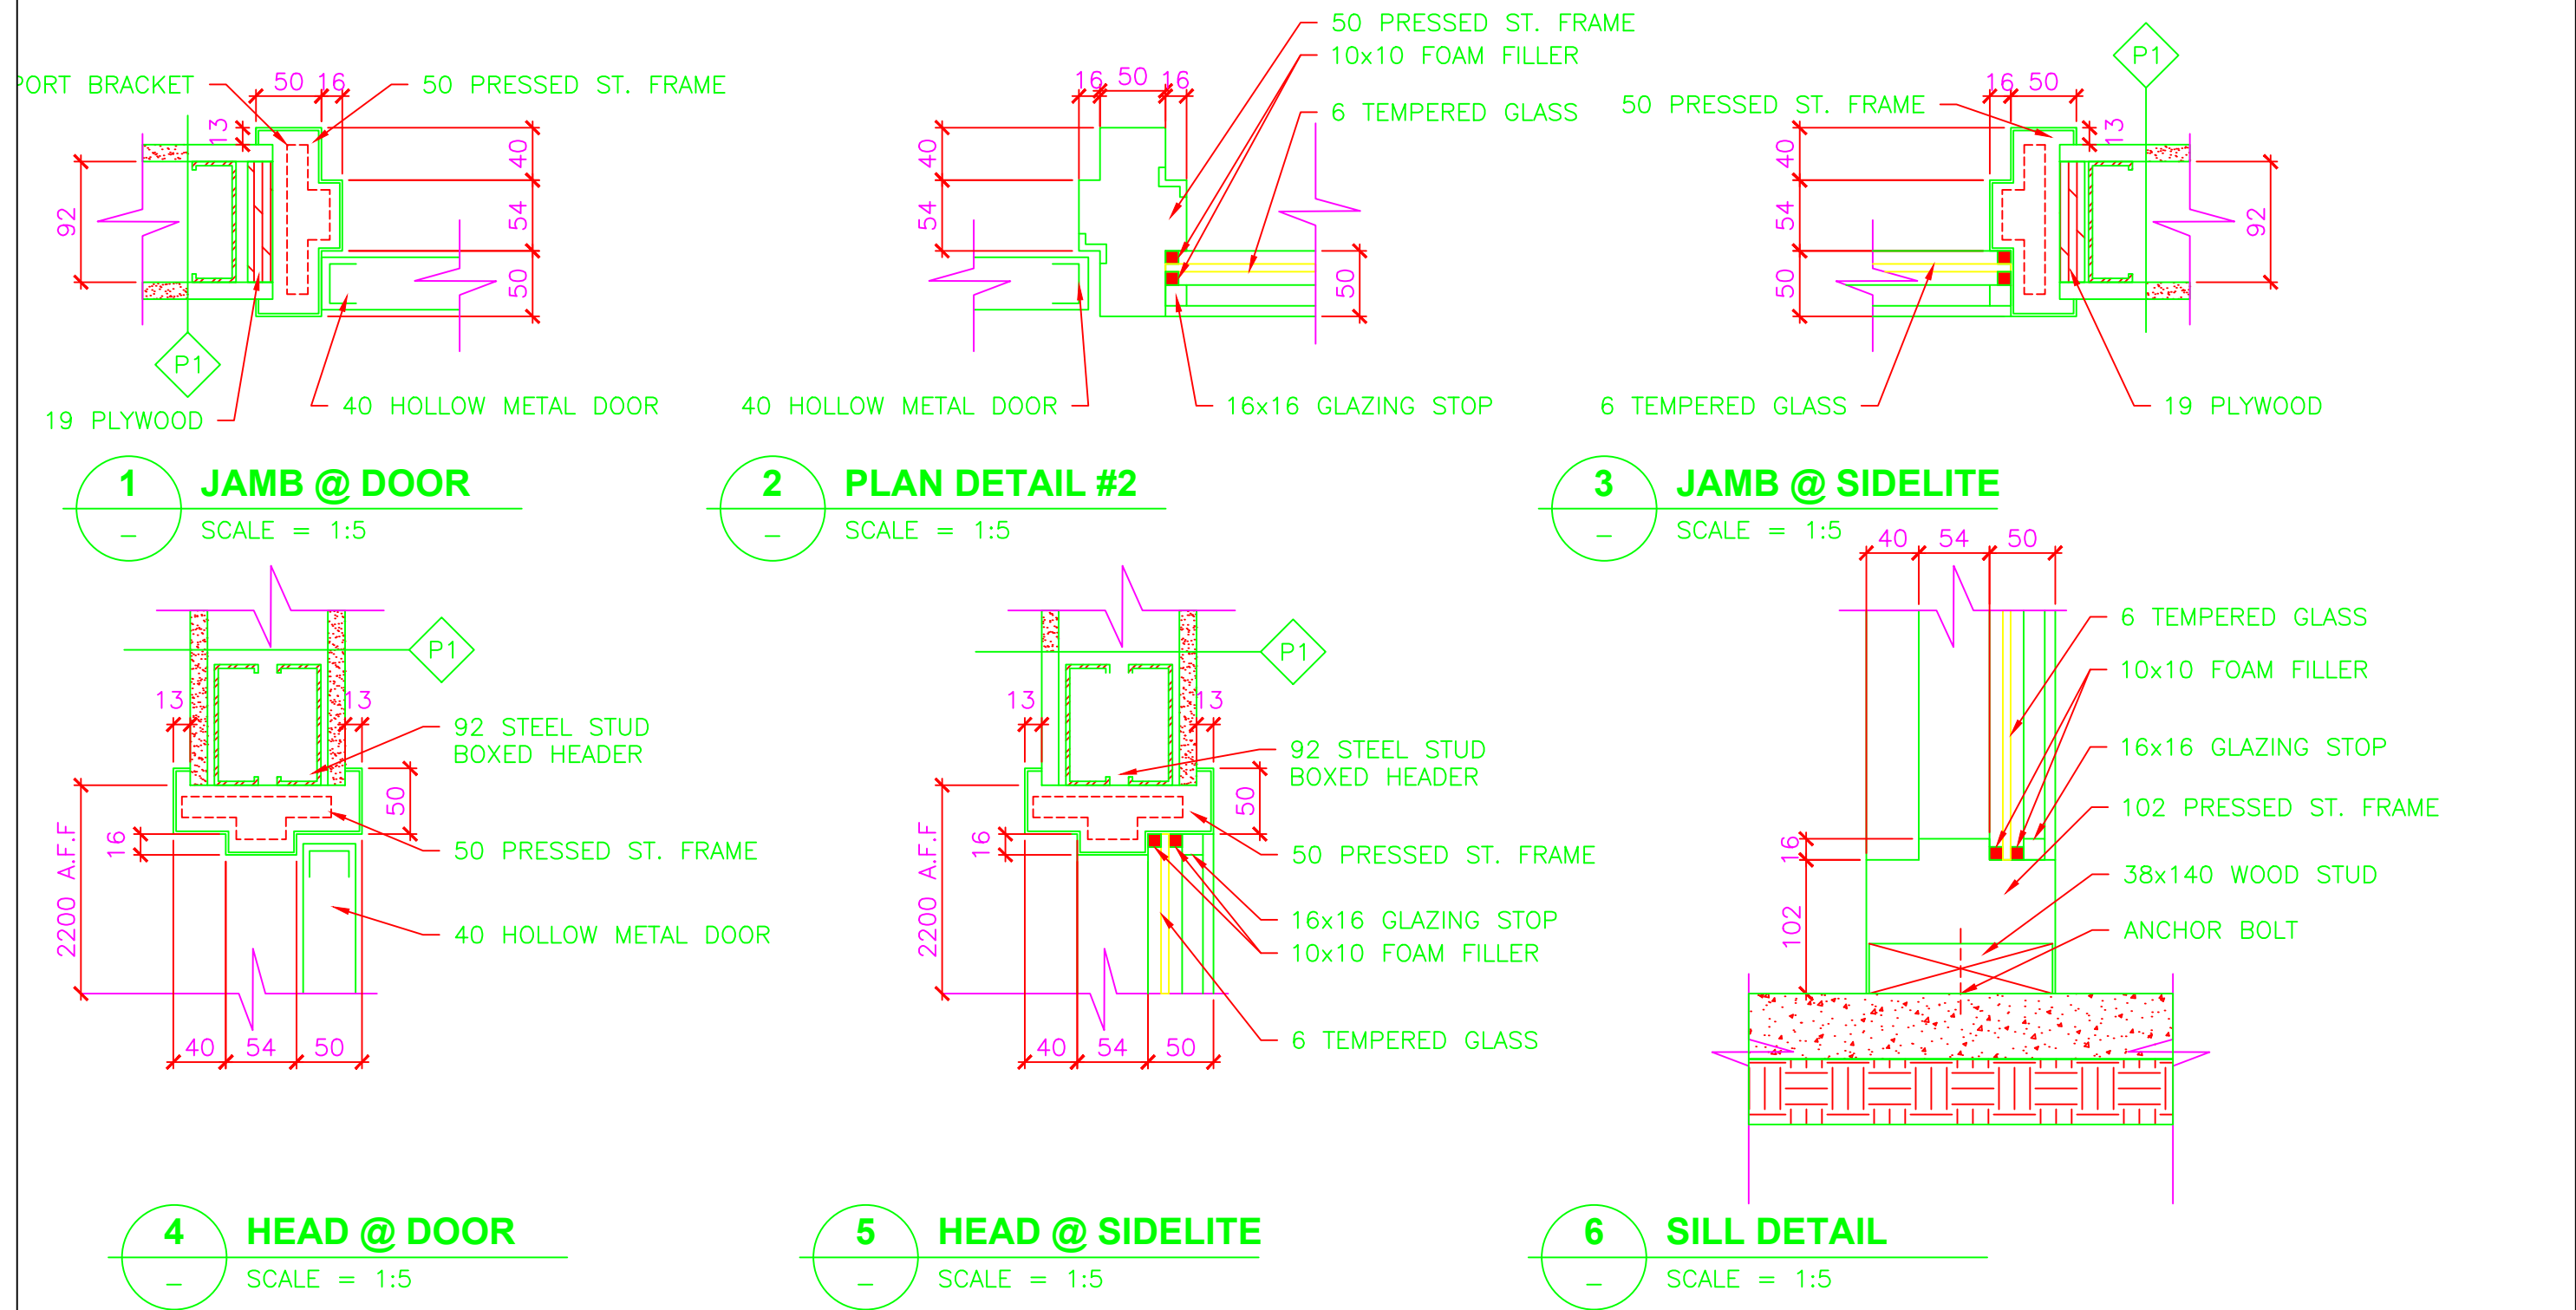

 SCHOOL OF CONSTRUCTION AND BUILDING SCIENCES ARCHITECTURAL TECHNOLOGY	PROJECT TITLE	DESIGNED BY:	NAIT	CLASS:	A03	NOTES:	CAD FILE
	EXERCISE 6	DRAWN BY:	CHIDERA UZO	INSTRUCTOR:	MELISSA PRICE		DRAWING No.
	DRAWING TITLE	DATE:	MARCH 2026	SCALE:	1:5		A1.1
	DOOR PLAN & SECTION DETAILS	COURSE:	ARCT 2611	SHEET:	1 of 1		