




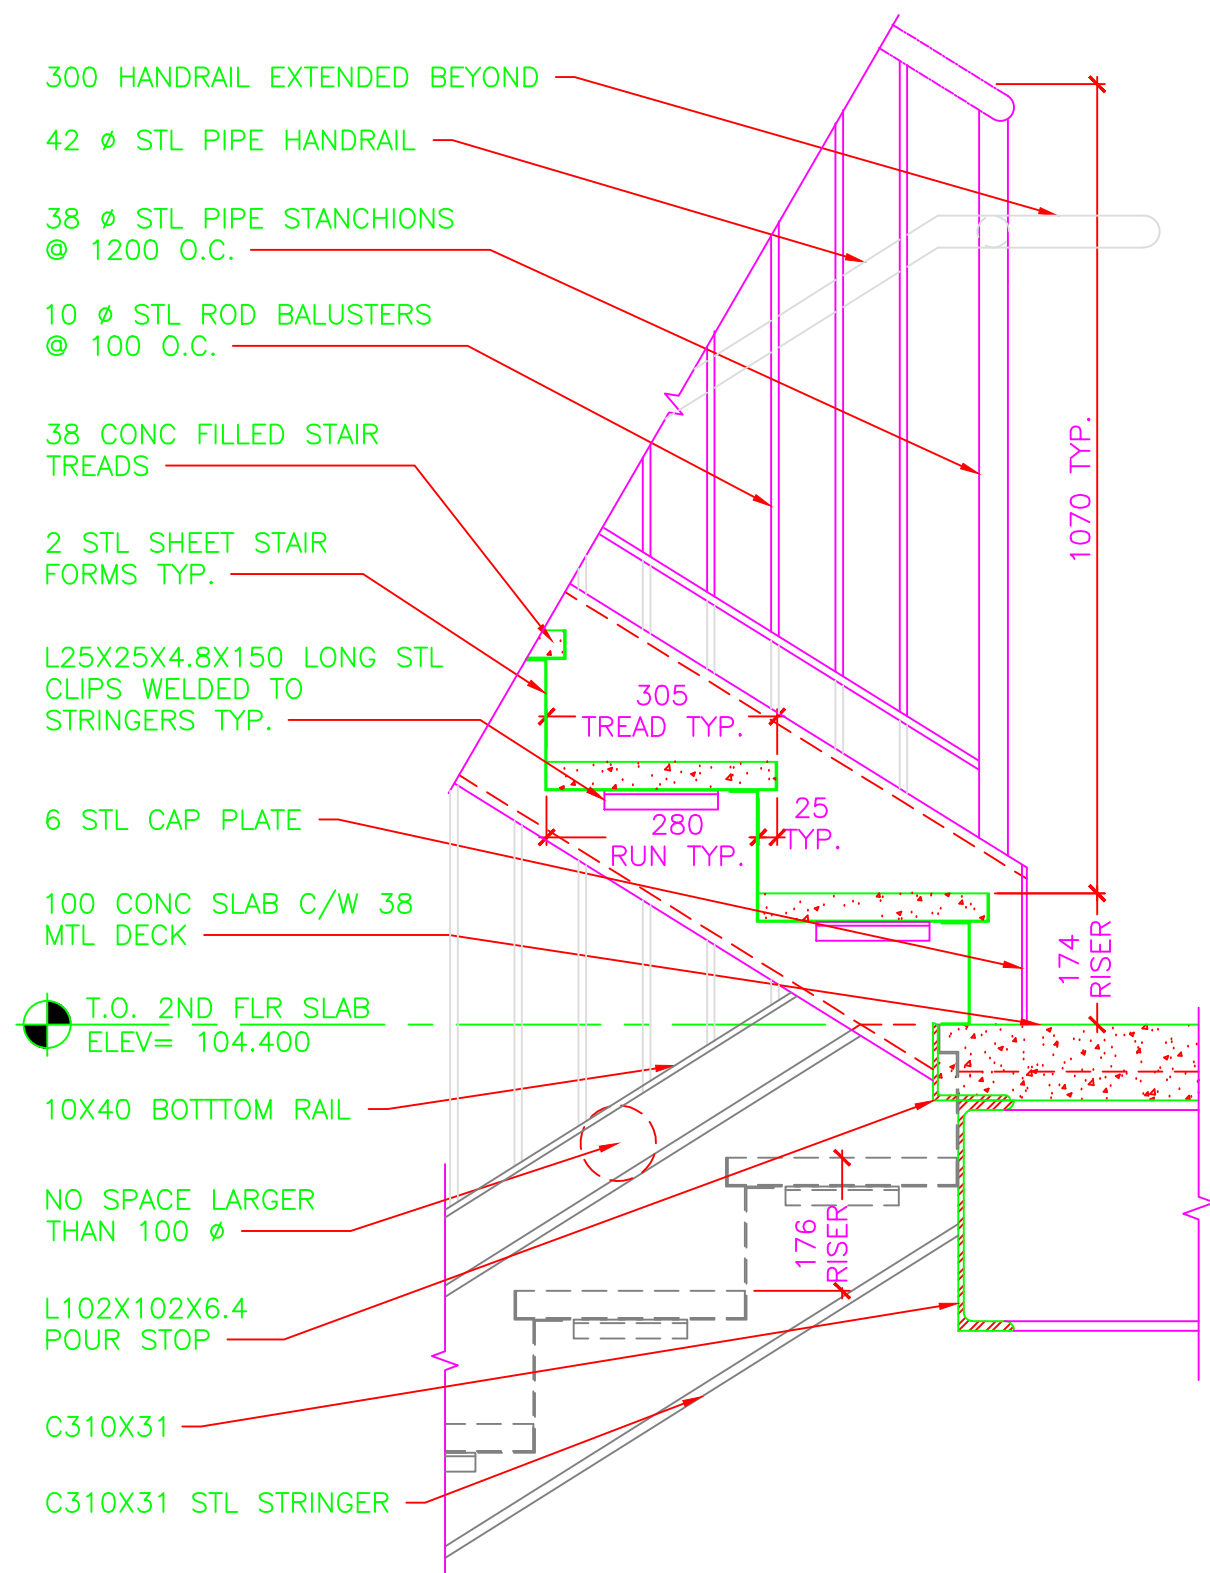


1 SECTION DETAIL
 A7 SCALE = 1:10

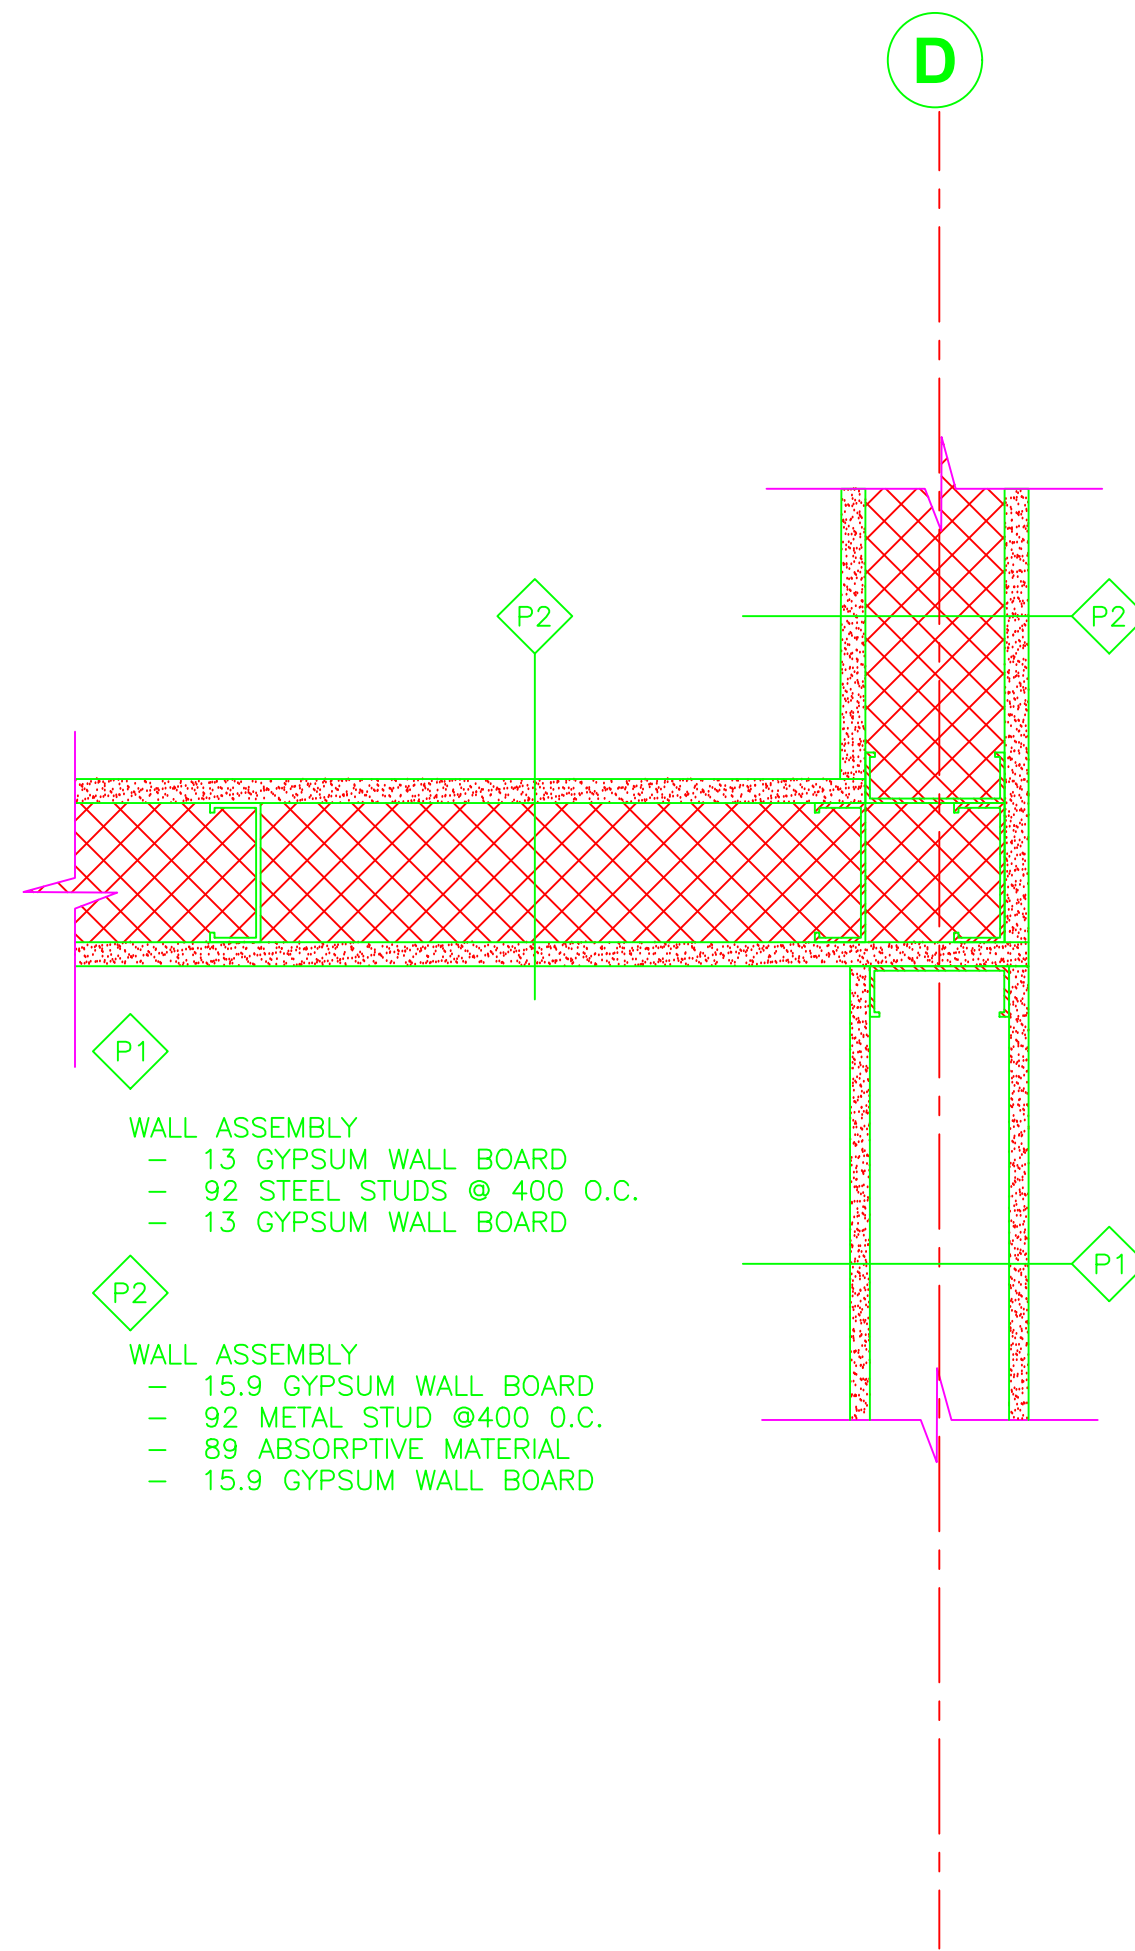


2 PLAN DETAIL 1
 A7 SCALE = 1:5

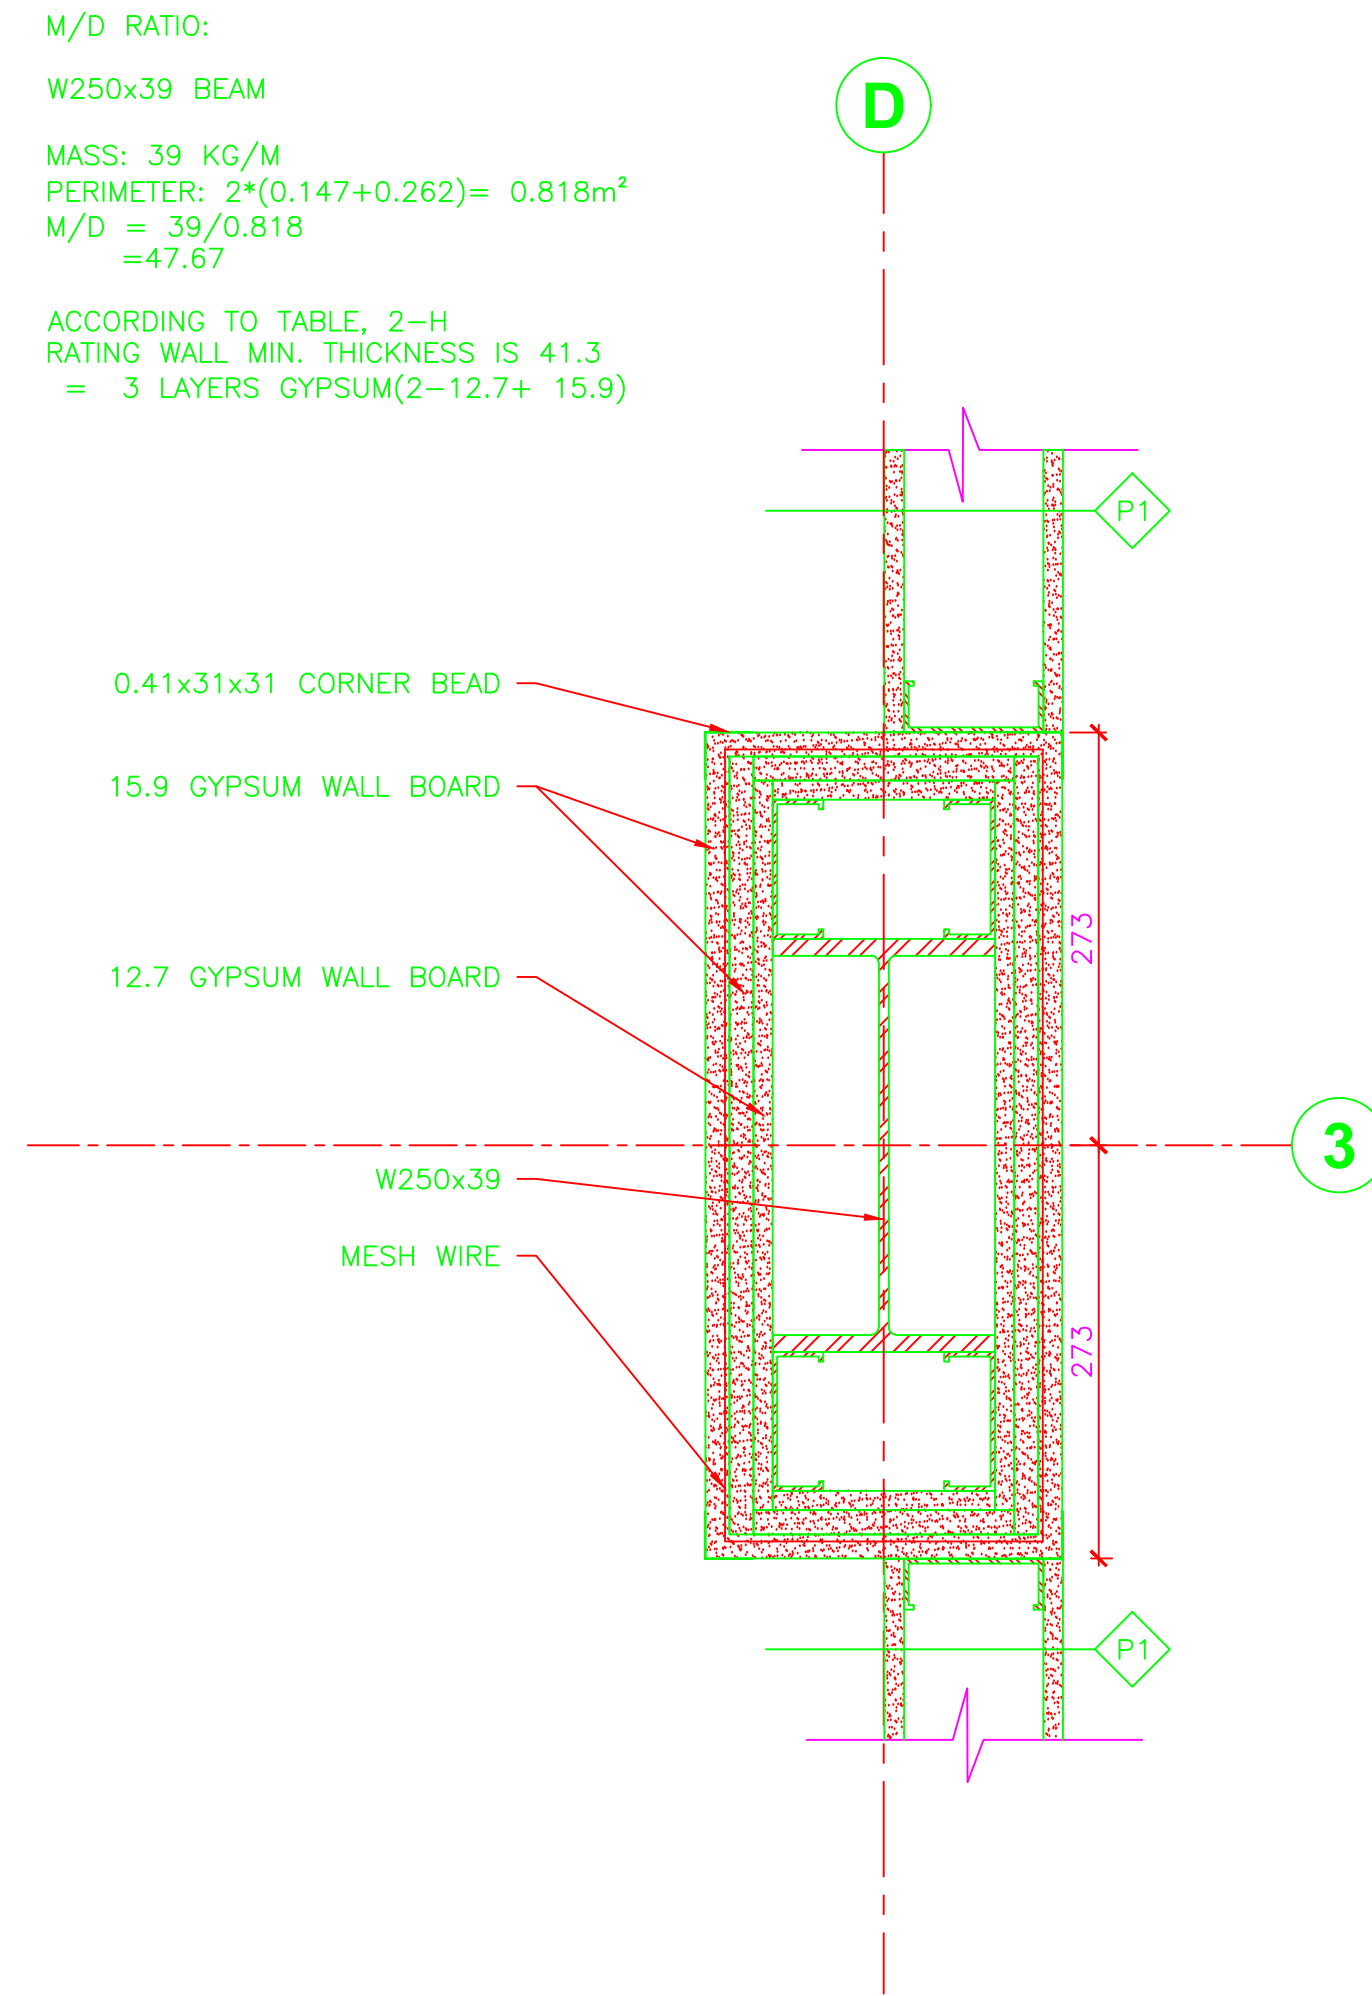

3 2-HR FIRE RATED COLUMN DETAIL
 A7 SCALE = 1:5

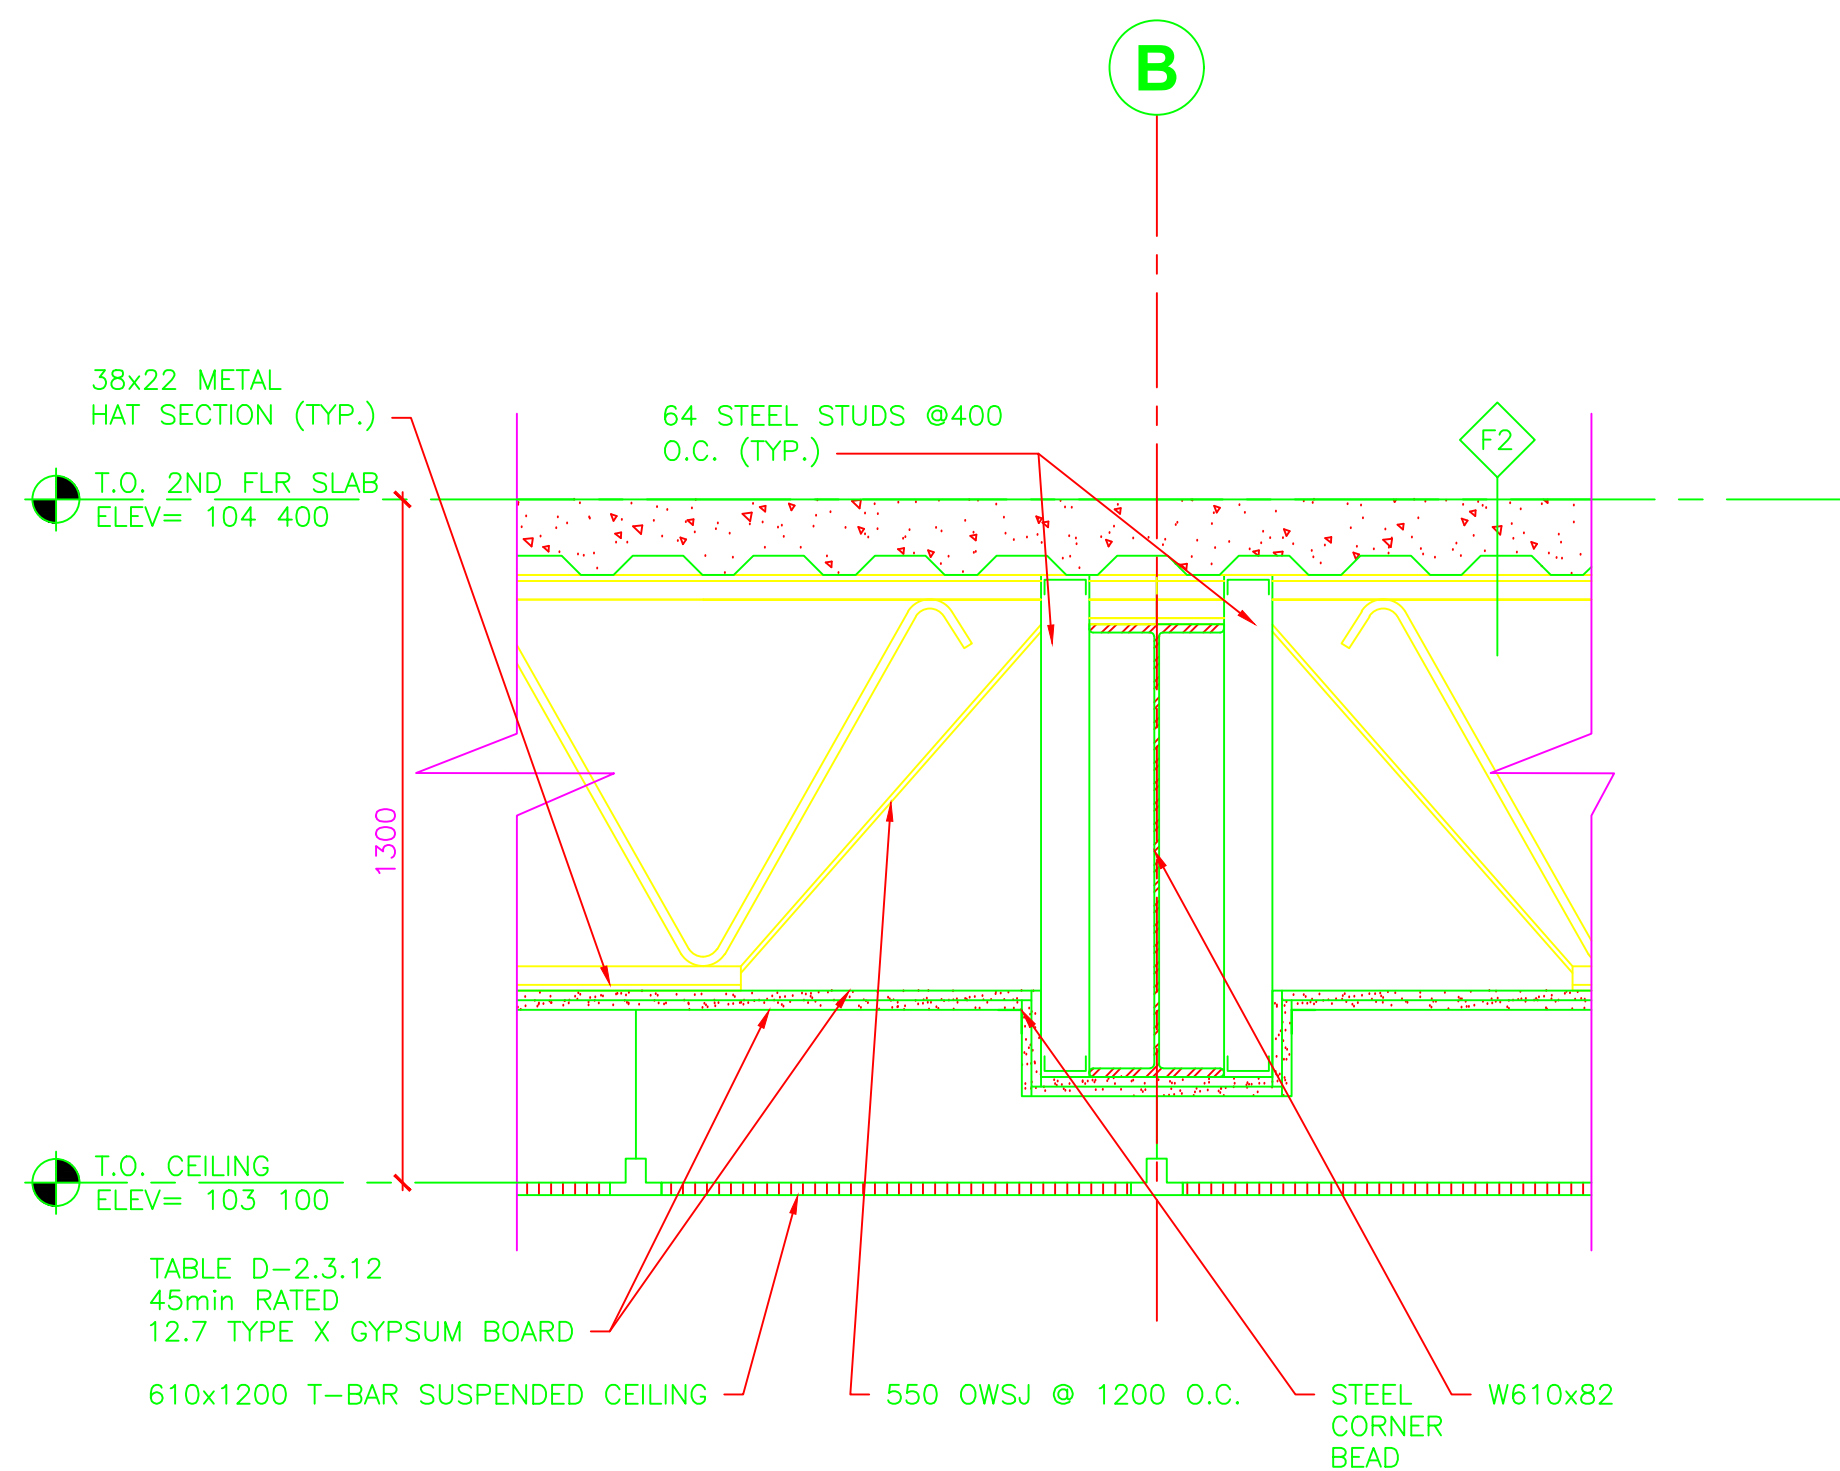

4 SECTION DETAIL @2ND FLOOR
 A7 SCALE = 1:10

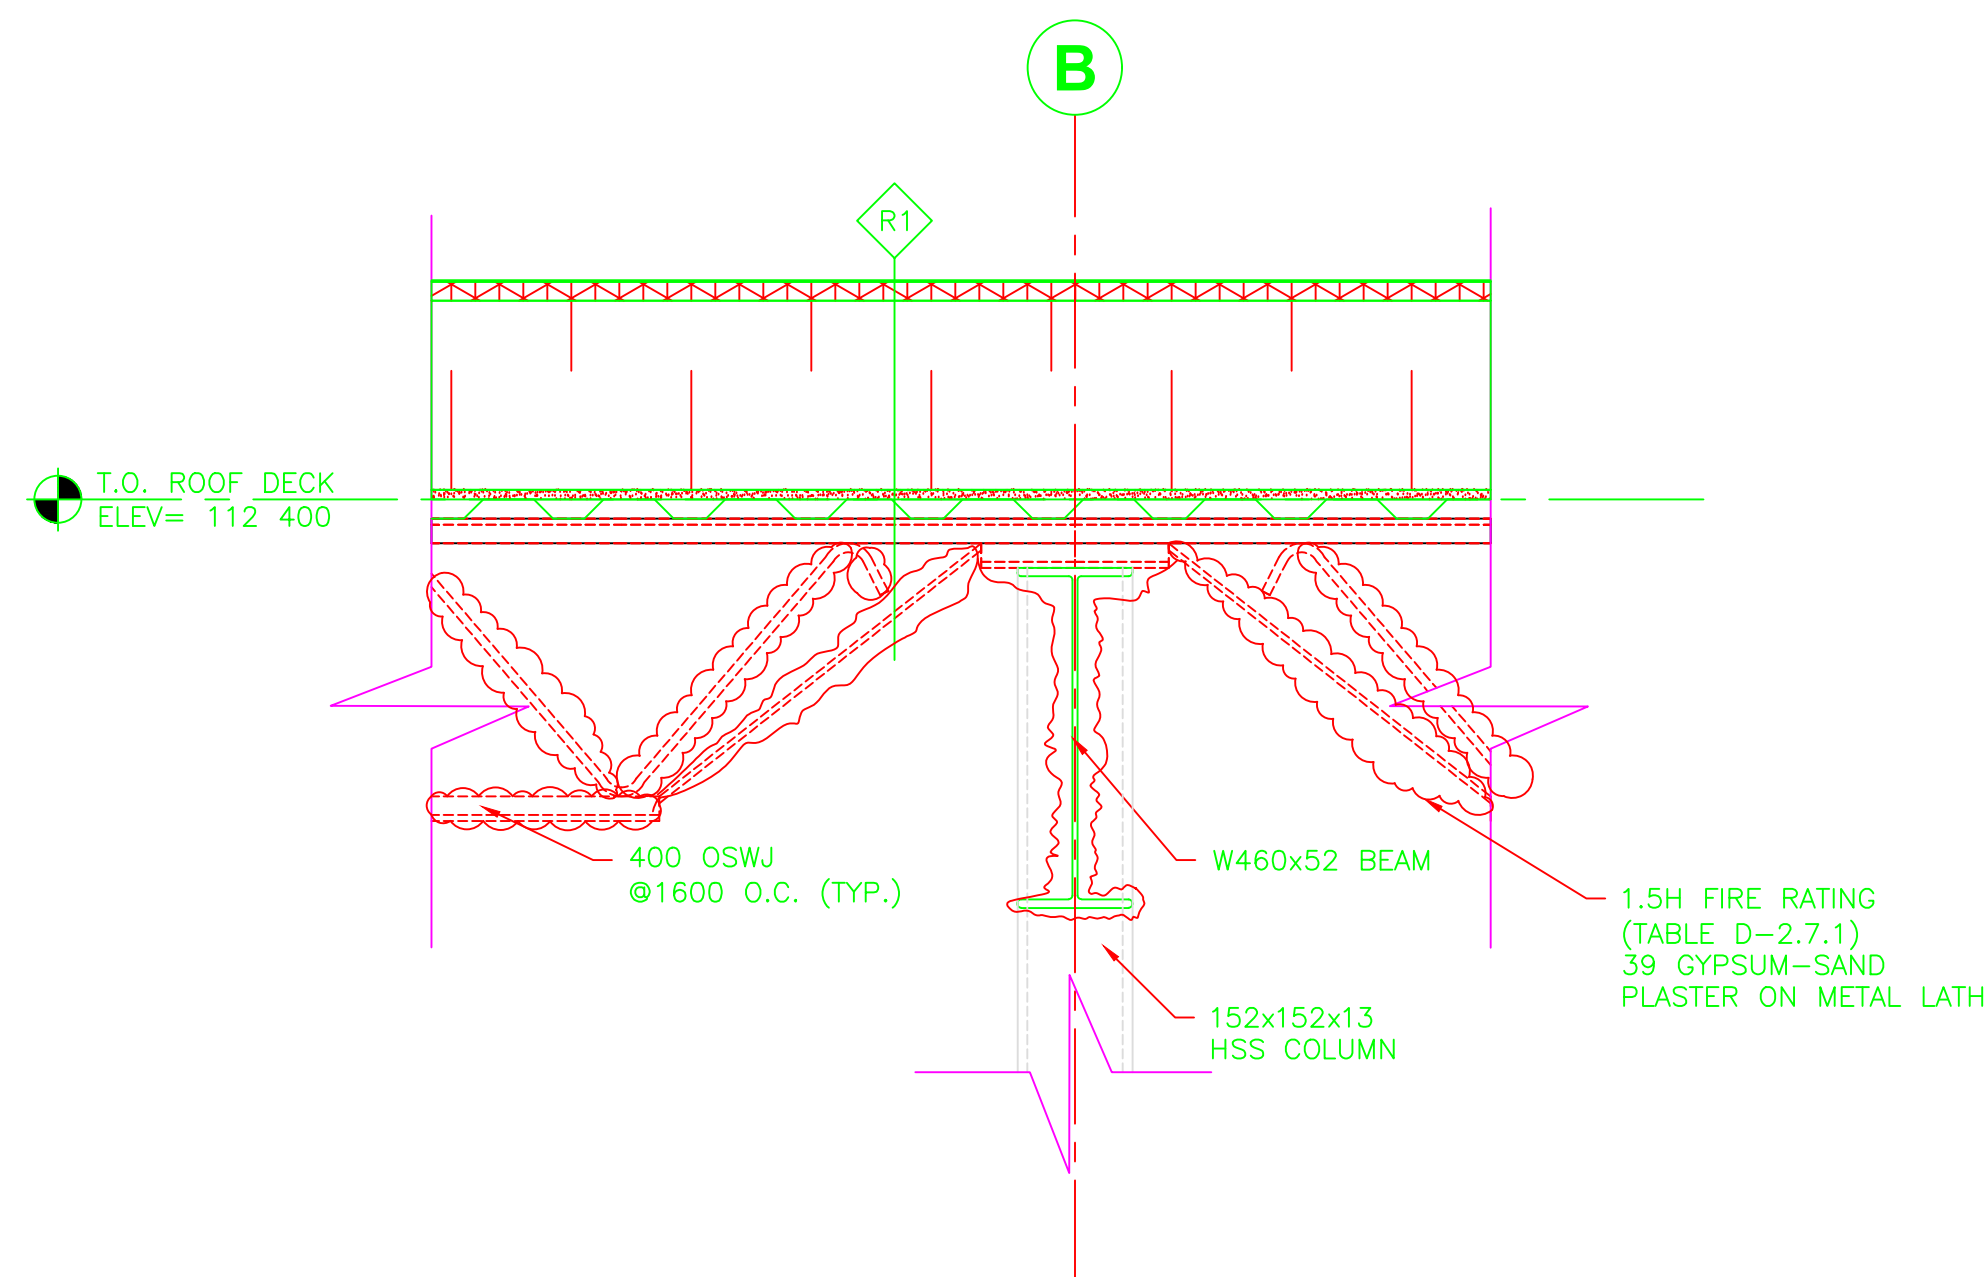

5 SECTION DETAIL @ROOF
 A7 SCALE = 1:10



**SCHOOL OF APPLIED
 SCIENCE AND TECHNOLOGY**
 ARCHITECTURAL TECHNOLOGY

CONSULTANTS

NOTES

REVISIONS

No. DATE DESCRIPTION

PROJECT

FINAL DETAIL SHEET

DRAWING

**CORRECTED DETAILS FOR
 EXERCISES 2, 9 & 10**

DESIGNED BY: NAIT

CHECKED BY: MELISSA PRICE

DRAWN BY: CHIDERA UZO

DATE: 23/04/2026

COURSE: CDOC 2611

CLASS: A03

INSTRUCTOR: MELISSA PRICE

SCALE: VARIES

SET: A7 / 5

PROJECT No:

PROJ. No.

CAD FILE:

SHEET No:

A7