DOOR SCHEDULE

CODE	DIMENSIONS			DOOR PANEL				DOOR FRAME		HARDWARE SET	FIRE RATING	COMMENTS
	WIDTH	HEIGHT	THICKNESS	PANEL TYPE	CORE TYPE	MATERIAL	FINISH	MATERIAL	FINISH			
T.O. MAIN FLOOR												
D102A	1736	2036	6	-	-	GL/AL	ANOD	AL	-	3	-	
D102B	1736	2036	6	-	-	GL/AL	ANOD	AL	-	3	-	
D104	900	2100	45	003	WD	WD	PT	PS	PT	5	45-min	
D105A	1200	2100	45	005	GL	GL/AL	ANOD	PS	PT	3	-	
D105B	900	2100	45	003	WD	WD	PT	PS	PT	4	45-min	
D107A	900	2100	45	006	HM	WD	PT	PS	PT	2	1 -h	
D107B	900	2100	45	001	IHM	PS	PT	PS	PT	1	-	
D108	900	2100	45	003	WD	WD	PT	PS	PT	4	45-min	
D109A	900	2100	45	006	HM	WD	PT	PS	PT	2	45-min	
D109B	900	2100	45	006	HM	WD	PT	PS	PT	2	45-min	
D111	900	2100	45	001	HM	WD	PT	PS	PT	9	45-min	
D113	900	2100	45	001	HM	WD	PT	PS	PT	9	45-min	
D114A	904	2036	6	-	-	GL/AL	ANOD	AL	-	3	-	
D114B	900	2100	45	005	HM	WD	PT	PS	PT	8	1.5-h	
D116	900	2100	45	001	HM	WD	PT	PS	PT	9	45-min	
D117	1800	2100	45	002	HM	WD	PT	PS	PT	9	1.5-h	
D118A	1800	2100	45	002	IHM	PS	PT	PS	PT	1	-	
D118B	1800	2100	45	002	HM	WD	PT	PS	PT	9	1.5-h	
D118C	2500	2500	40	004	INS	ST	PT	-	-	4	1 -h	
D119A	900	2100	45	001	IHM	PS	PT	PS	PT	1	-	
D119B	3200	4000	40	004	INS	ST	PT	-	-	4	-	
D119C	3200	4000	40	004	INS	ST	PT	-	-	4	-	
D119D	3200	4000	40	004	INS	ST	PT	-	-	4	-	
D119E	3200	4000	40	004	INS	ST	PT	-	-	4	-	
D119F	900	2100	45	003	WD	WD	PT	PS	PT	4	45-min	
D120A	1200	2100	45	005	GL	GL/AL	ANOD	AL	PT	3	-	
D120B	1800	2100	45	002	WD	WD	PT	PS	PT	10	1.5-h	

DOOR SCHEDULE

CODE	DIMENSIONS			DOOR PANEL				DOOR FRAME		HARDWARE SET	FIRE RATING	COMMENTS
	WIDTH	HEIGHT	THICKNESS	PANEL TYPE	CORE TYPE	MATERIAL	FINISH	MATERIAL	FINISH			
T.O. 2ND FLOOR												
D203	900	2100	45	006	HM	WD	PT	PS	PT	2	1 -h	
D204	900	2100	45	001	WD	WD	PT	PS	PT	11	30-min	
D205	900	2100	45	005	WD	WD	PT	PS	PT	5	30-min	
D206	900	2100	45	003	WD	WD	PT	PS	PT	5	30-min	
D207	900	2100	45	003	WD	WD	PT	PS	PT	5	30-min	
D208	900	2100	45	003	WD	WD	PT	PS	PT	5	30-min	
D209	900	2100	45	003	WD	WD	PT	PS	PT	5	30-min	
D210	900	2100	45	005	HM	WD	PT	PS	PT	8	1.5-h	
D212	1800	2100	45	002	HM	WD	PT	PS	PT	9	1.5-h	
D213	900	2100	45	001	HM	WD	PT	PS	PT	9	45-min	
D214	900	2100	45	001	HM	WD	PT	PS	PT	9	45-min	
D215	900	2100	45	001	HM	WD	PT	PS	PT	9	45-min	
D216	900	2100	45	001	HM	WD	PT	PS	PT	9	45-min	
T.O. 3RD FLOOR												
D302	900	2100	45	001	HM	WD	PT	PS	PT	9	45-min	
D303	900	2100	45	001	HM	WD	PT	PS	PT	9	45-min	
D304	900	2100	45	005	WD	WD	PT	PS	PT	5	30-min	
D305	900	2100	45	005	WD	WD	PT	PS	PT	5	30-min	
D306	900	2100	45	003	WD	WD	PT	PS	PT	5	30-min	
D307	900	2100	45	003	WD	WD	PT	PS	PT	5	30-min	
D308	900	2100	45	003	WD	WD	PT	PS	PT	5	30-min	
D309	900	2100	45	006	HM	WD	PT	PS	PT	2	1 -h	
D310	900	2100	45	001	WD	WD	PT	PS	PT	11	30-min	
D312A	900	2100	45	005	HM	WD	PT	PS	PT	8	1.5-h	
D312B	900	2100	45	001	IHM	PS	PT	PS	PT	1	-	
T.O. ROOF DECK												
D401	900	2100	45	001	IHM	PS	PT	PS	PT	1	-	

DOOR HARDWARE

HARDWARE GROUP	HARDWARE TYPE	OPERATION MECHANISM	HARDWARE LATCHING	HARDWARE CLOSER	HARDWARE OTHER
1	Swing Door	Butt Hinges	Lockset	Concealed Closer	Panic Hardware, Weatherstripping, Threshold
2	Swing Door	Butt Hinges	None	Concealed Closer	Panic Hardware
3	Swing Door	Butt Hinges	Lockset	Concealed Closer	Push/Pull, Weatherstripping, Threshold
4	-	-	-	-	As Per Manufacturer
5	Swing Door	Butt Hinges	Lockset	-	Kickplate
6	Swing Door	Butt Hinges	Lockset	-	Kickplate, Push/Pull
7	Swing Door	Butt Hinges	Privacy Set	Concealed Closer	Kickplate
8	Swing Door	Butt Hinges	Passage Set	Concealed Closer	Kickplate, Panic Hardware
9	Swing Door	Butt Hinges	Lockset	Concealed Closer	Kickplate, Panic Hardware
10	Swing Door	Butt Hinges	-	Concealed Closer	Kickplate, Push/Pull, Panic Hardware
11	Swing Door	Butt Hinges	Lockset	Concealed Closer	Kickplate
12	Swing Door	Butt Hinges	-	Concealed Closer	Kickplate, Push/Pull

WINDOW SCHEDULE

CODE	HEIGHT	WIDTH	SILL HEIGHT	COMMENTS
T.O. MAIN FLOOR				
G1	900	1000	1000	Sealed Unit Glazing With Aluminium Frame
T.O. 2ND FLOOR				
G1	900	1000	1000	Sealed Unit Glazing With Aluminium Frame
G2	900	7600	1920	Sealed Unit Glazing With Aluminium Frame
T.O. 3RD FLOOR				
G1	900	1000	1000	Sealed Unit Glazing With Aluminium Frame

DOOR PANEL LEGEND

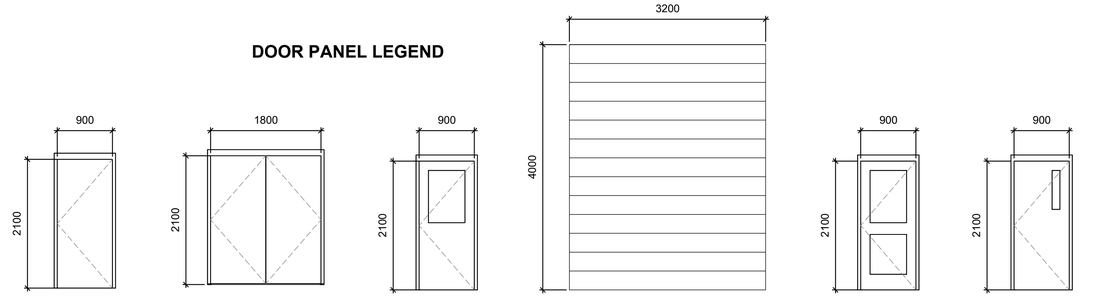

ABBREVIATIONS

AL	ALUMINUM
ALT	ALUMINUM, THERMAL BREAK
ANOD	ANODIZED
CLR	CLEAR
EX	EXISTING
GL	GLASS
HC	HOLLOW CORE
HM	HOLLOW METAL
INS	INSULATED
IHM	INSULATED HOLLOW METAL
O/H	OVERHEAD
PS	PRESSED METAL
PT	PAINT
S	SOLID CORE
ST	STEEL
WD	WOOD

NAIT

SCHOOL OF CONSTRUCTION AND APPLIED BUILDING SCIENCE

ARCHITECTURAL TECHNOLOGY

No.	Description	Date

NAIT AMBULANCE HEADQUARTERS

DOOR & WINDOW SCHEDULES

Class Number	A03
Date	23/03/2026
Drawn by	CHIDERA UZO
Instructor	ANDRE LUCENA

A9.1

Scale 1 : 50