LEGAL DESCRIPTION	MUNICIPAL ADDRESS
123456789-0	12306 111 Ave NW, Edmonton, AB

BUILDING CODE SYNOPSIS

PROJECT DESCRIPTION:
AMBULANCE STATION HEADQUARTERS
NEW BUILDING

GOVERNING CODE: NBC-AB-2023

AUTHORITY HAVING JURISDICTION: CITY OF EDMONTON

DEVELOPMENT PERMIT PROJECT NUMBER: 123456-0 ☐ EXISTING ☒ NEW

MAJOR OCCUPANCY (S): D

MINOR OCCUPANCY (S): F3

BUILDING CLASSIFICATION: BUSINESS & PERSONAL SERVICES

GROSS AREA (m²): NEW CONSTRUCTION / RENOVATION:
LEVEL 1 758.22 / 861.71 m²
LEVEL 2 529.91 / 857.65 m²
LEVEL 3 394.32 / 467.58 m²
TOTAL AREA: 1682.45 m²

NUMBER OF STOREYS: ABOVE GRADE: 4 BELOW GRADE: 0

HIGH BUILDING: ☒ NO ☐ YES

MEZZANINE(S): ☒ NO ☐ YES QUANTITY:

BUILDING HEIGHT: 16.75 m

NUMBER OF FACING STREETS / ACCESS ROUTES: 1 / 2

TYPE OF CONSTRUCTION: NEW CONSTRUCTION: COMBUSTIBLE / NON-COMBUSTIBLE
EXISTING CONSTRUCTION: N/A

SPRINKLER SYSTEM: ☒ YES ☐ NO

STANDPIPE REQUIRED: ☒ YES ☐ NO

FIRE ALARM REQUIRED: ☒ YES ☐ NO

BARRIER FREE PROVISIONS: ☒ YES ☐ NO

FIRE RESISTANCE RATING:

FIREWALLS:	2 HOUR
FLOORS:	N/A
MEZZANINE:	N/A
ROOF:	N/A
LOAD BEARING WALLS AND STRUCTURE:	2 HOUR
MECHANICAL ROOMS:	1.5 HOUR
ELECTRICAL ROOMS:	N/A
JANITOR ROOMS:	45 MIN
STORAGE ROOMS:	1.5 HOUR
<OTHER>:	N/A

FIRE SEPARATION:

OCCUPANCY:	N/A
SUITE:	N/A
PUBLIC CORRIDOR:	N/A
EXIT:	N/A
STORAGE GARAGE:	2 HOUR
REPAIR GARAGE:	1.5 HOUR

*ALL FIRE SEPARATIONS TO U/S OF STRUCTURE

EXTERIOR WALL CONSTRUCTION:

BUILDING ELEVATION	NORTH	EAST	SOUTH	WEST
TOTAL AREA OF UNPROTECTRED OPENINGS	136.58 m²	N/A	N/A	N/A
EXPOSED BUILDING FACE OF WALL AREA	547.18 m²	N/A	N/A	N/A
UNPROTECTED OPENINGS AS % OF WALL AREA	24.96 %	N/A	N/A	N/A
LIMITING DISTANCE OF NEW OR ALTERED WALL	4 m	N/A	N/A	N/A
MINIMUM REQUIRED WALL RATING	N/A	N/A	N/A	N/A
NON-COMBUSTIBLE CONSTRUCTION REQUIRED	☒ NO ☐ YES	☒ NO ☐ YES	☒ NO ☐ YES	☒ NO ☐ YES
NON-COMBUSTIBLE CLADDING REQUIRED	☒ NO ☐ YES	☒ NO ☐ YES	☒ NO ☐ YES	☒ NO ☐ YES

NOTES:

OCCUPANT LOAD

NUMBER	NAME	AREA	OCCUPANCY	LOAD FACTOR	OCCUPANT LOAD
T.O. MAIN FLOOR					
103	RECEPTION	14.88 m²	OFFICE	9.30 m²	2
104	SECURITY OFFICE	20.61 m²	OFFICE	9.30 m²	3
105	CLASSROOM	53.67 m²	CLASSROOM	1.85 m²	30
115	KITCHEN	75.00 m²	KITCHEN	9.30 m²	9
117	STORAGE	18.82 m²	STORAGE	46.00 m²	1
118	STORAGE	34.98 m²	STORAGE	46.00 m²	1
119	VEHICLE BAY	214.05 m²	GARAGE	46.00 m²	5
120	STAFF LOUNGE	72.64 m²	ASSEMBLY SPACE WITH NON-FIXED SEATS AND TABLES	0.95 m²	77
					128
T.O. 2ND FLOOR					
202	WORSTATIONS	193.79 m²	OFFICE	9.30 m²	21
205	MEETING ROOM	19.79 m²	OFFICE	9.30 m²	3
206	DISPATCH OFFICE	12.21 m²	OFFICE	9.30 m²	2
207	DISPATCH OFFICE	8.85 m²	OFFICE	9.30 m²	1
208	DISPATCH OFFICE	12.15 m²	OFFICE	9.30 m²	2
209	DISPATCH OFFICE	10.23 m²	OFFICE	9.30 m²	2
211	STAFF LOUNGE	110.04 m²	ASSEMBLY SPACE WITH NON-FIXED SEATS AND TABLES	0.95 m²	116
					147
T.O. 3RD FLOOR					
304	MEETING ROOM	41.77 m²	OFFICE	9.30 m²	5
305	DISPATCH OFFICE	14.64 m²	OFFICE	9.30 m²	2
306	DISPATCH OFFICE	10.72 m²	OFFICE	9.30 m²	2
307	DISPATCH OFFICE	12.58 m²	OFFICE	9.30 m²	2
308	DISPATCH OFFICE	12.52 m²	OFFICE	9.30 m²	2
311	WORKSTATIONS	200.93 m²	OFFICE	9.30 m²	22
					35
					310

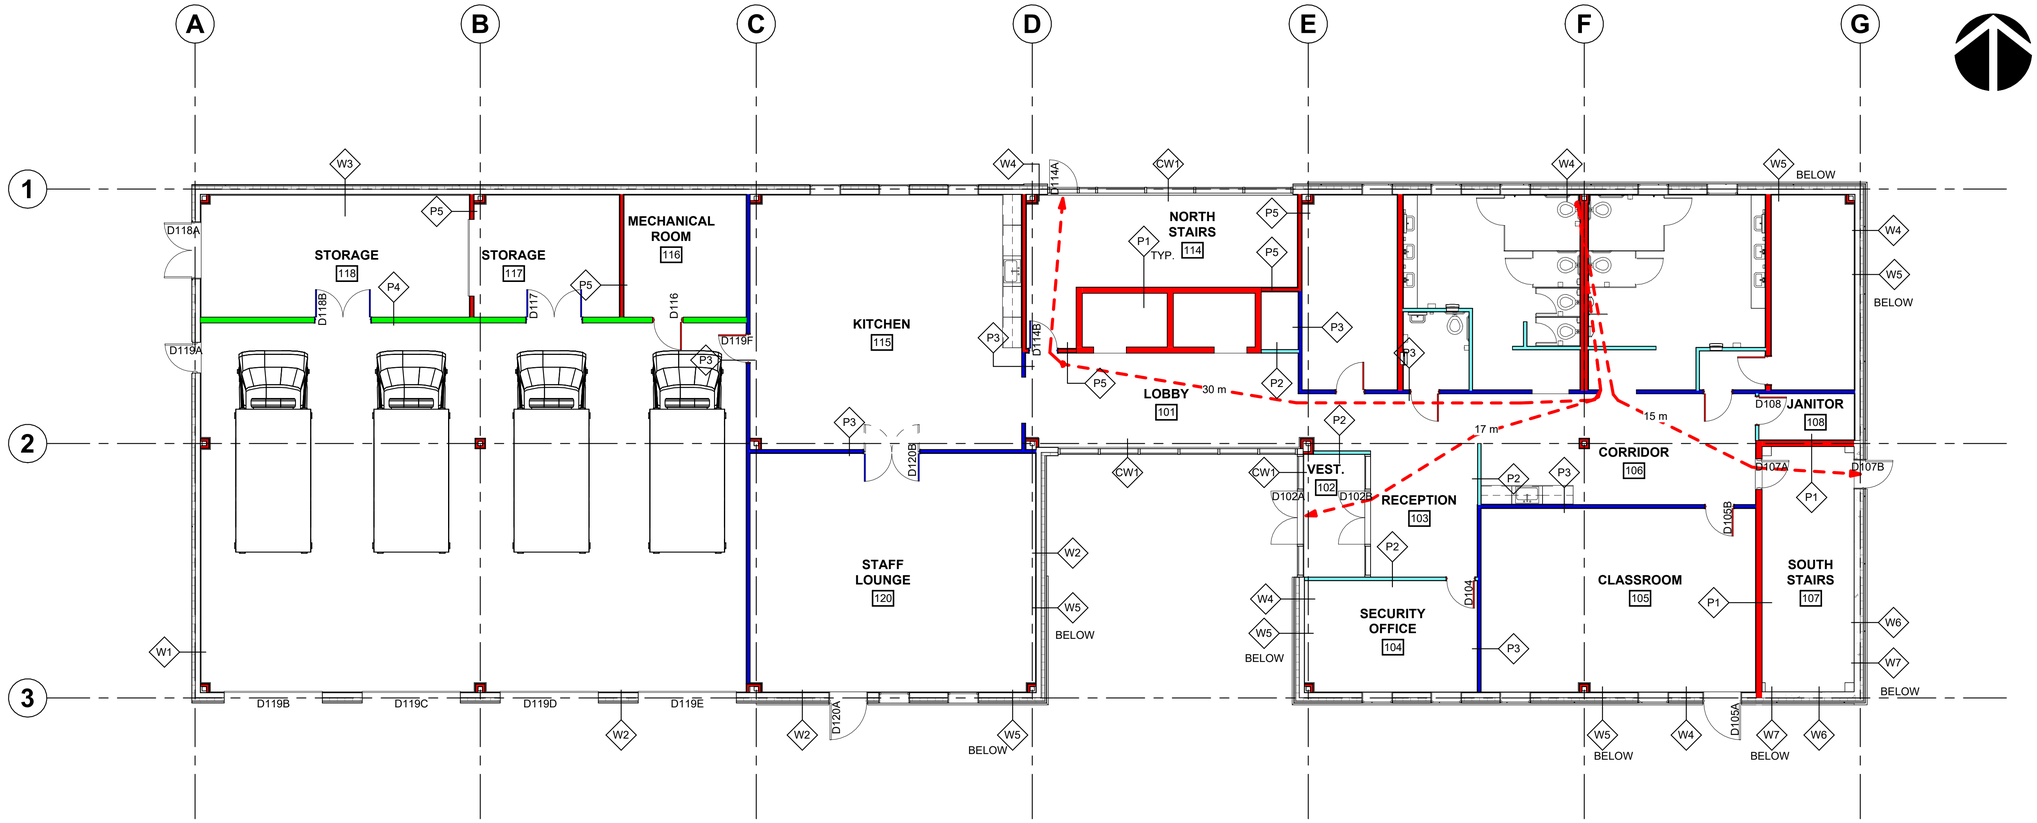

1 A2.6 **MAIN FLOOR LIFE SAFETY PLAN**
SCALE = 1 : 100

DOOR FIRE RATINGS
- 30-min FIRE SEPARATION
- 45-min FIRE SEPARATION
- 1-h FIRE SEPARATION
- 1.5-h FIRE SEPARATION

WALL FIRE RATINGS
- 45-min FIRE SEPARATION
- 1-h FIRE SEPARATION
- 1.5-h FIRE SEPARATION
- 2-h FIRE SEPARATION

No.	Description	Date

NAIT
SCHOOL OF CONSTRUCTION AND APPLIED BUILDING SCIENCE
ARCHITECTURAL TECHNOLOGY

NAIT AMBULANCE HEADQUARTERS

MAIN FLOOR LIFE SAFETY PLAN

Class Number	A03
Date	23/03/2026
Drawn by	CHIDERA UZO
Instructor	ANDRE LUCENA

A2.6

Scale: As indicated

C:\SCHOOL\PORTFOLIO\PORTFOLIO AMBULANCE STATION (2).rvt