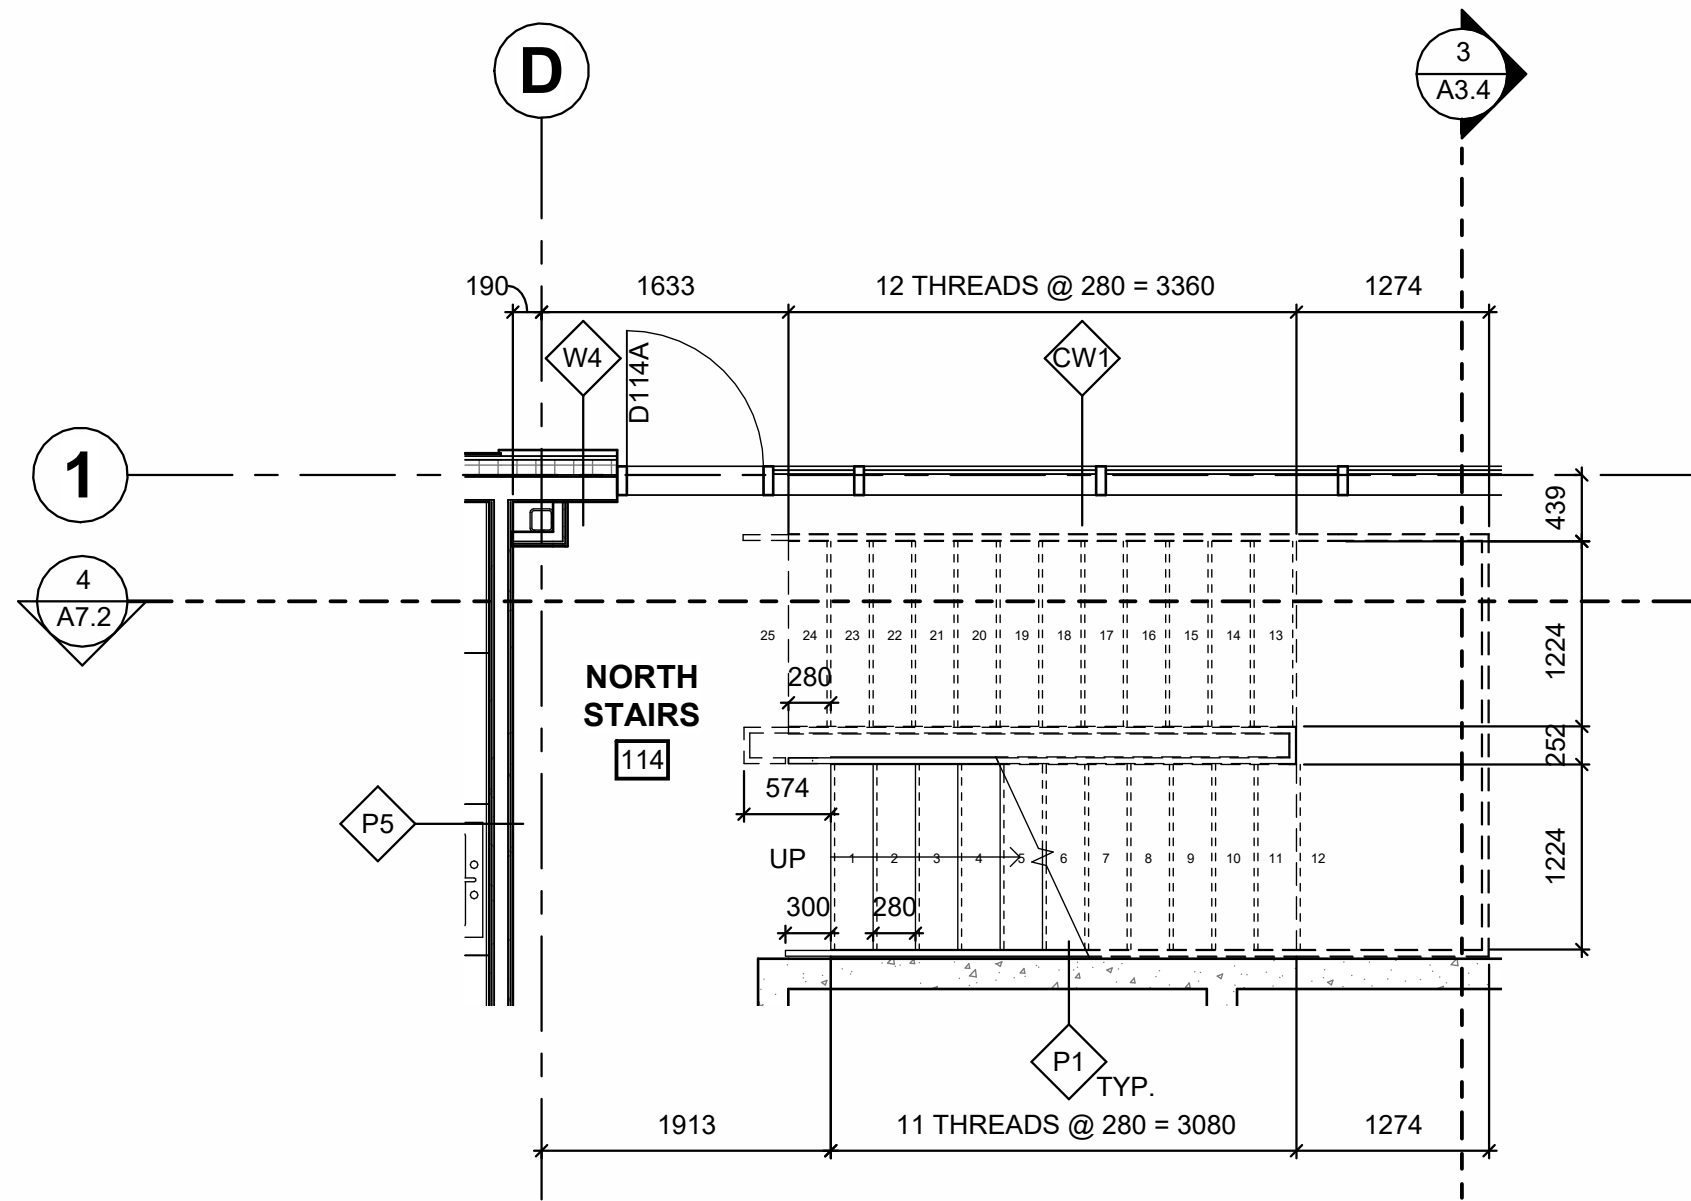


[illegible][illegible]

Architectural section drawing of a building showing three floors: T.O. MAIN FLOOR (ELEV = 100000), T.O. 2ND FLOOR (ELEV = 104400), and T.O. 3RD FLOOR (ELEV = 108400). The drawing includes a roof deck (T.O. ROOF DECK ELEV = 112400) and a section line D-D. The drawing shows a staircase with 11 runs @ 280 = 3080 and 12 runs @ 280 = 3360. The total height of the building is 4000 units. The drawing includes various dimensions and labels: R1, PT3, W3, F2, P5, F1, and F2. The drawing also includes a section line D-D and a section line F1-F2.

4 NORTH STAIRS SECTION
A2.1 SCALE = 1 : 50

NAIT
AMBULANCE
HEADQUARTERS

NORTH STAIRS PLANS AND SECTIONS

Class Number	A03
--------------	-----

Date 23/03/2026

Drawn by **CHIDERA UZO**

Instructor **ANDRE LUCENA**

A7.2

Scale 1 : 50