


[illegible]


NAIT
AMBULANCE
HEADQUARTERS

SOUTH STAIRS PLANS AND SECTIONS


Class Number	A03
Date	23/03/2026
Drawn by	CHIDERA UZO
Instructor	ANDRE LUCENA
A7.1	
Scale	1 : 50

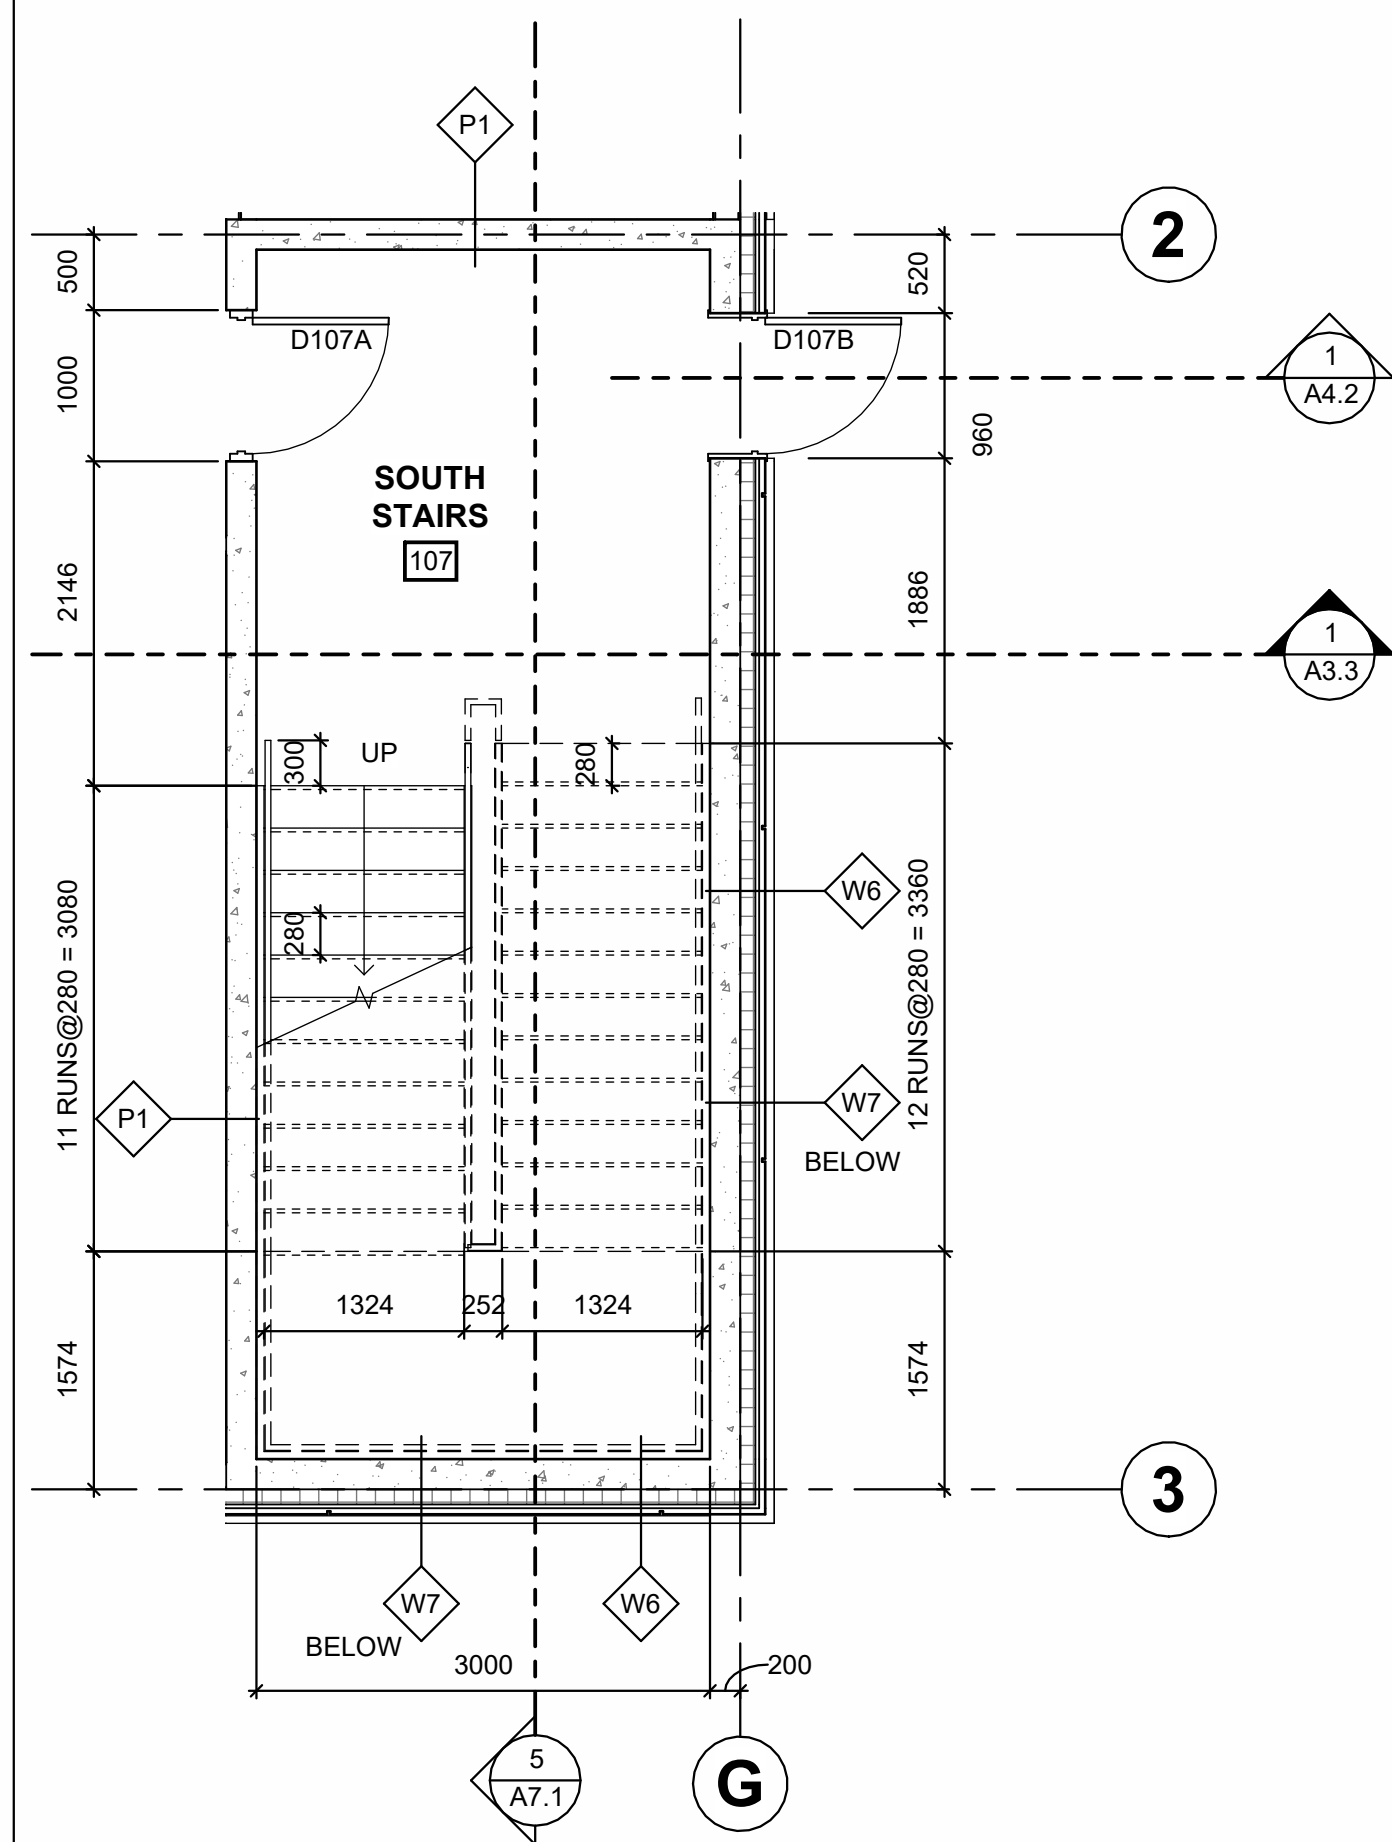


1 SOUTH STAIRS MAIN FLOOR PLAN
A7.1 SCALE = 1 : 50

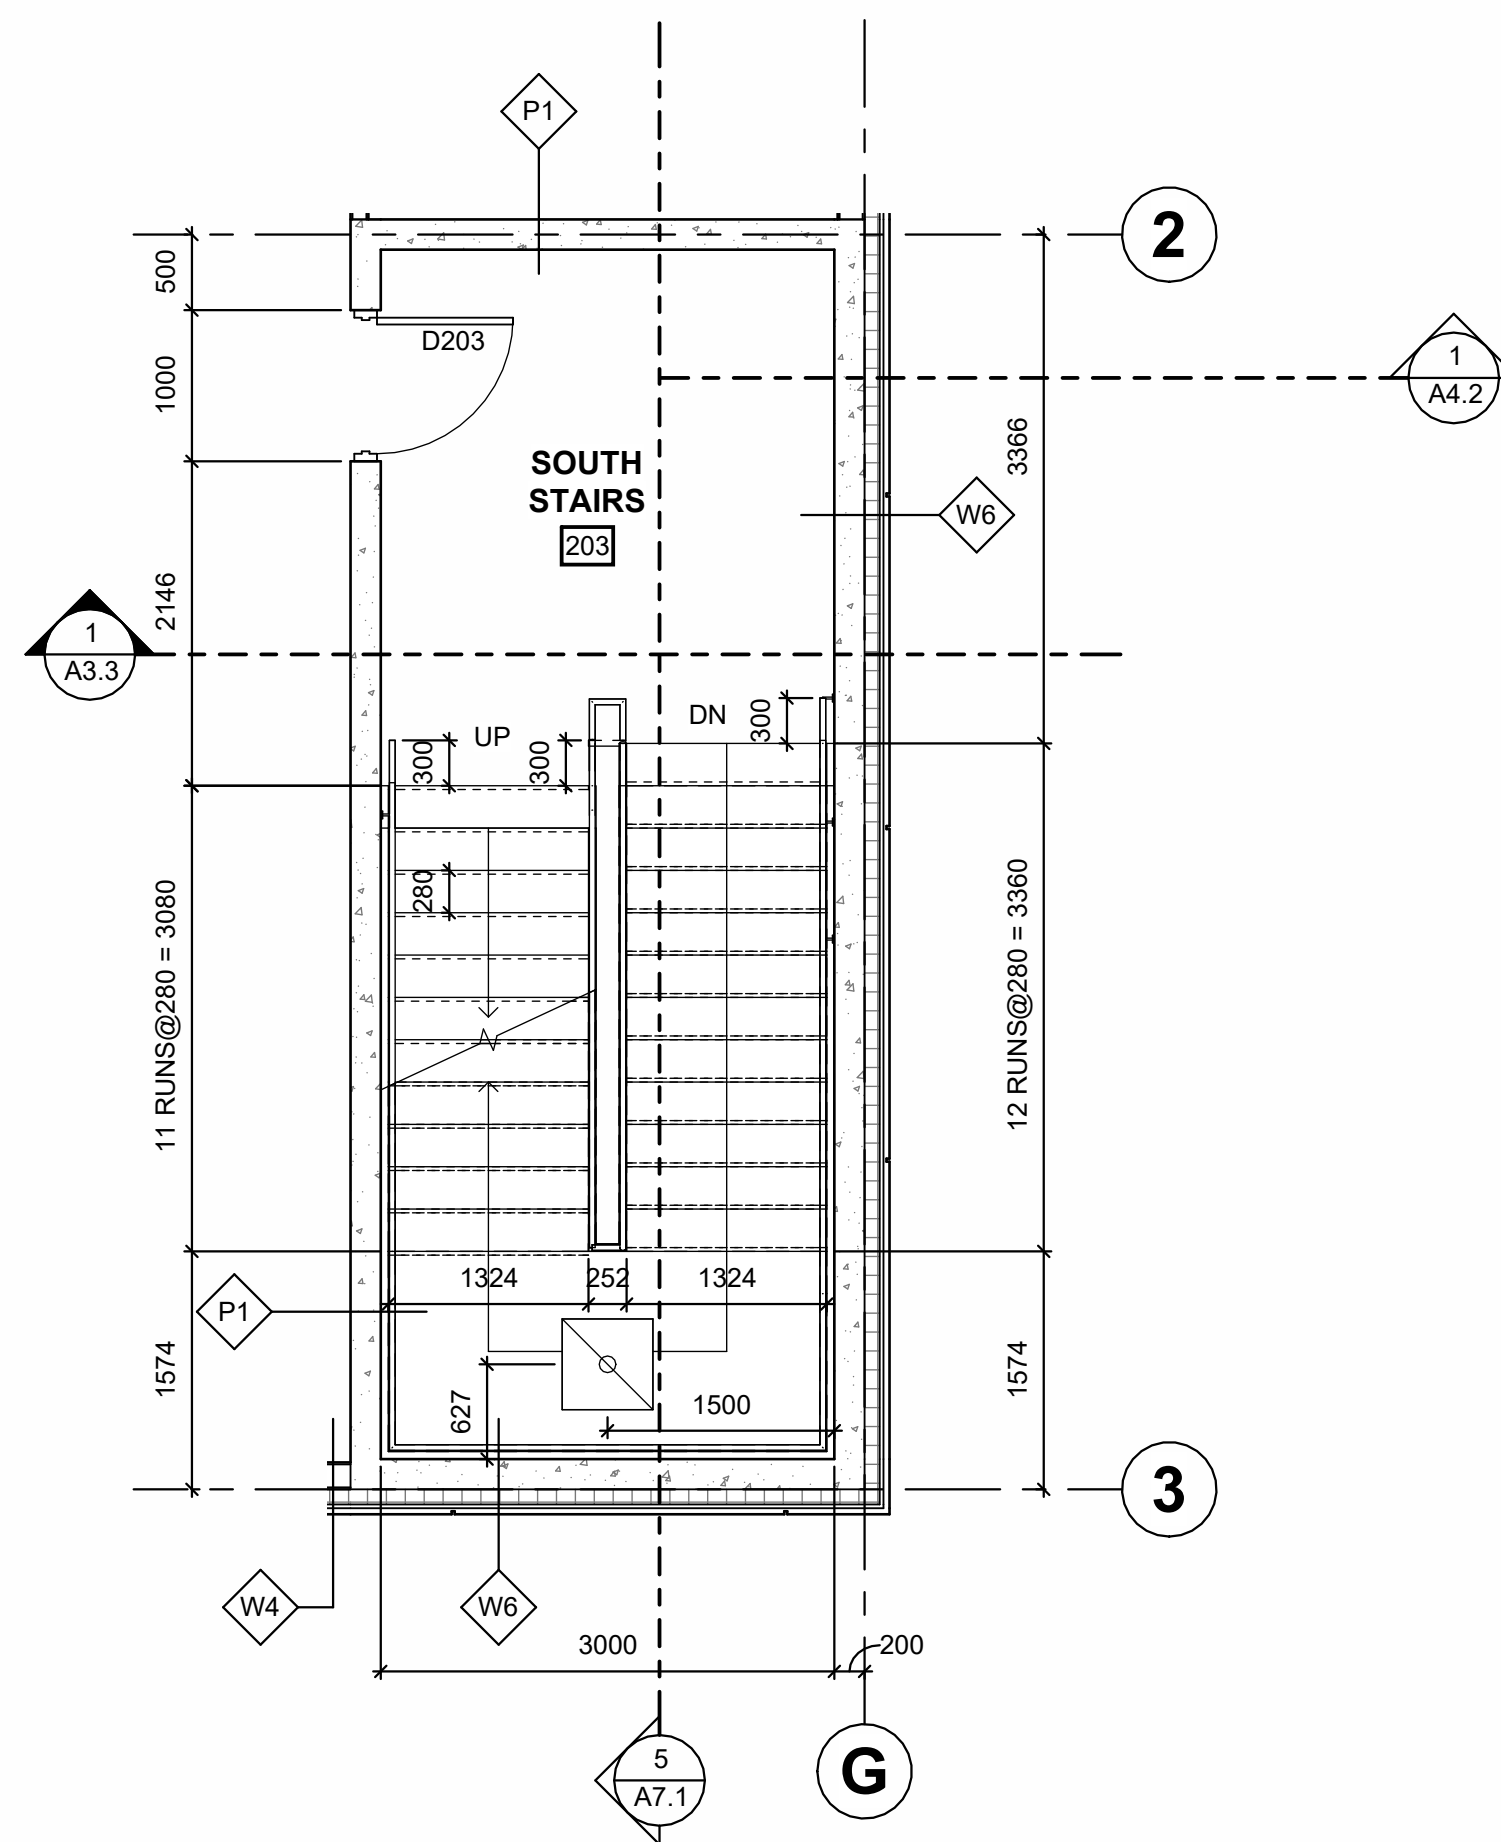


2 SOUTH STAIRS SECOND FLOOR PLAN
A7.1 SCALE = 1 : 50

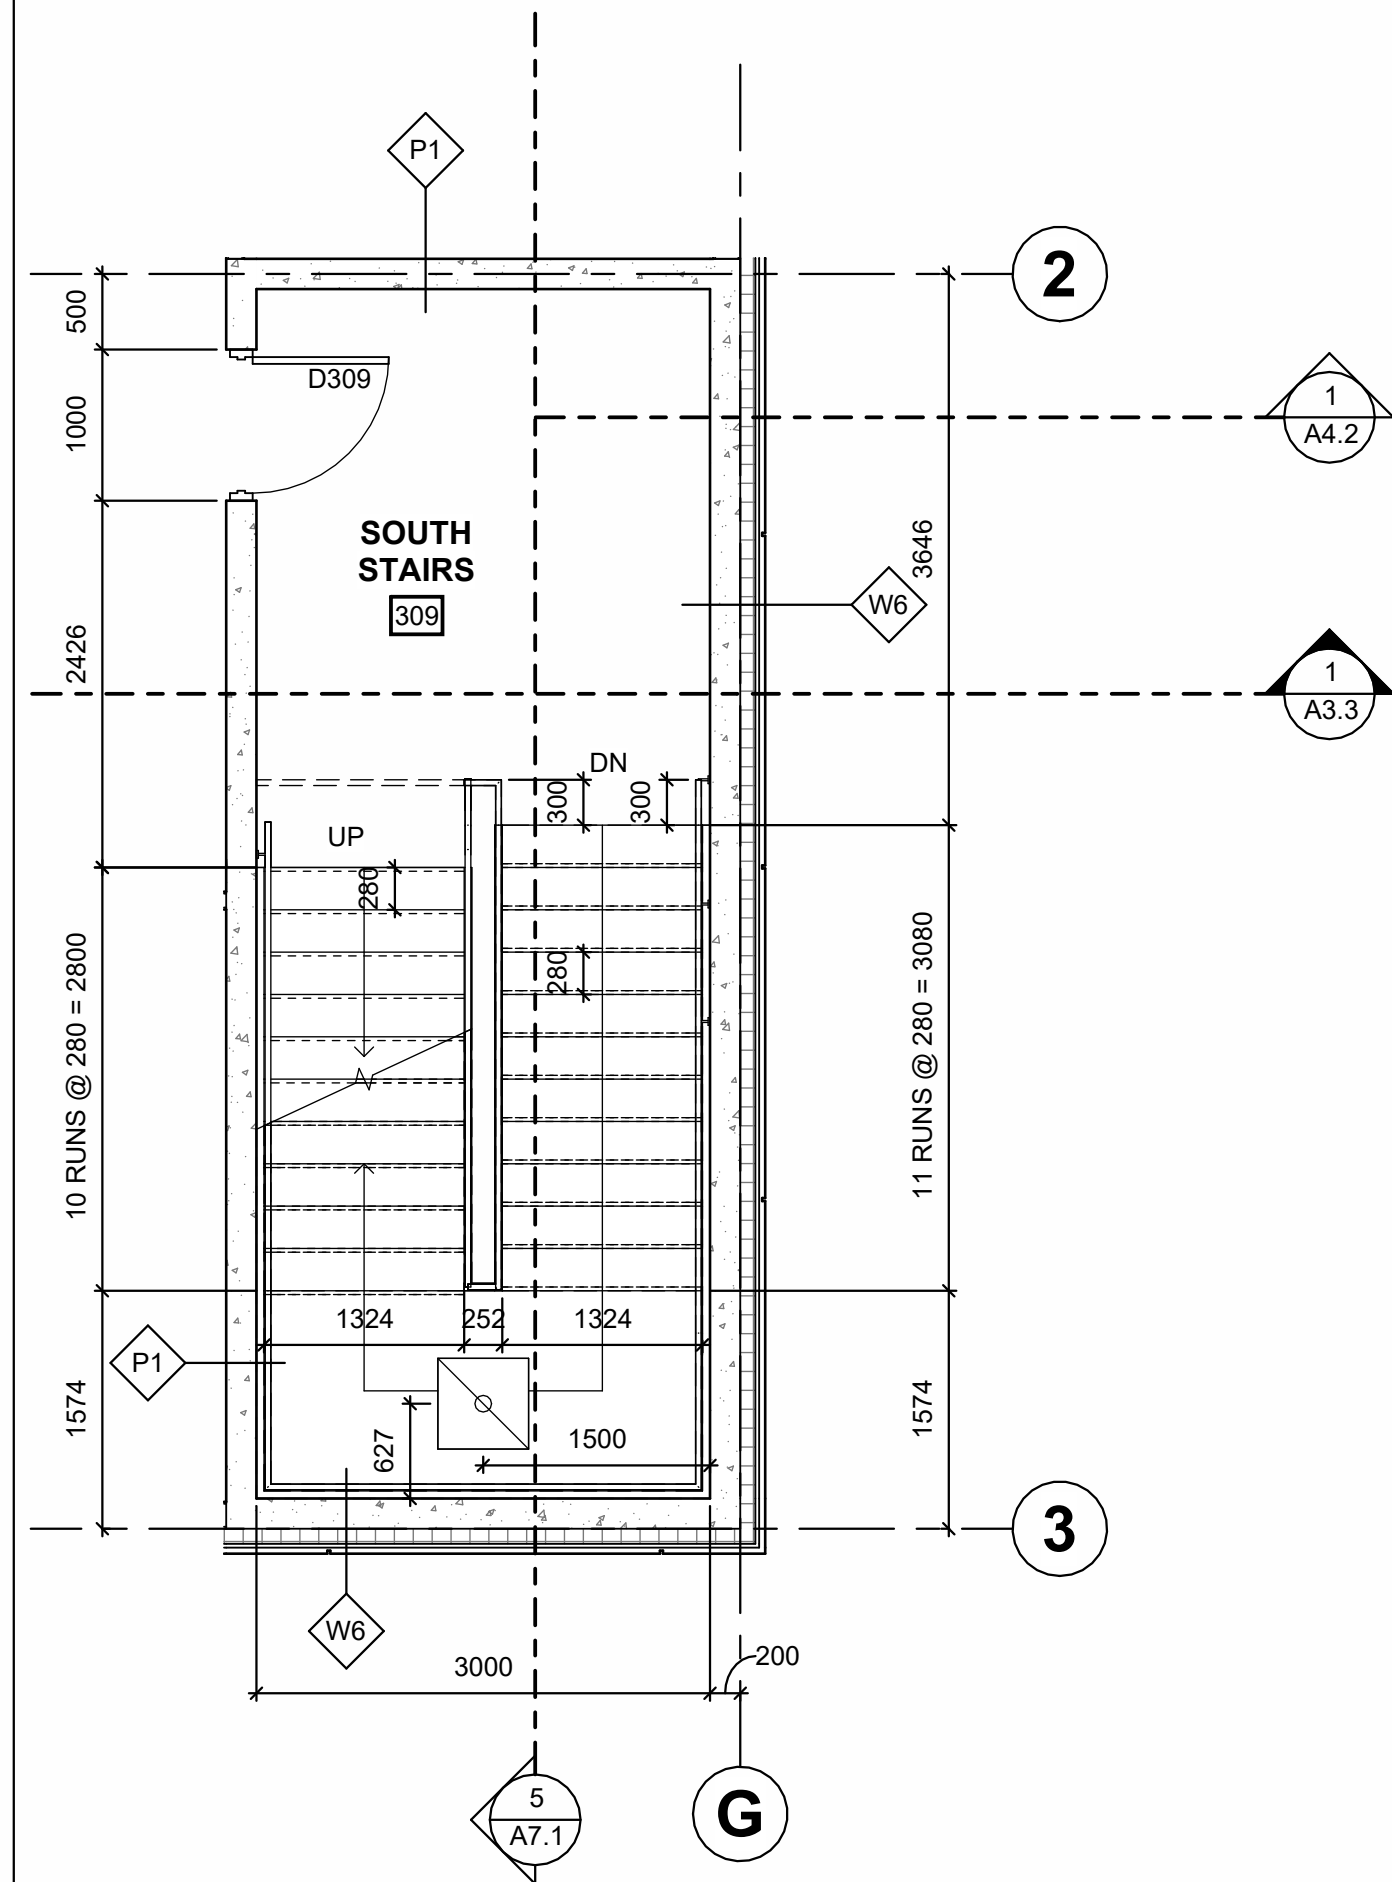

3 SOUTH STAIRS THIRD FLOOR PLAN
A7.1 SCALE = 1 : 50

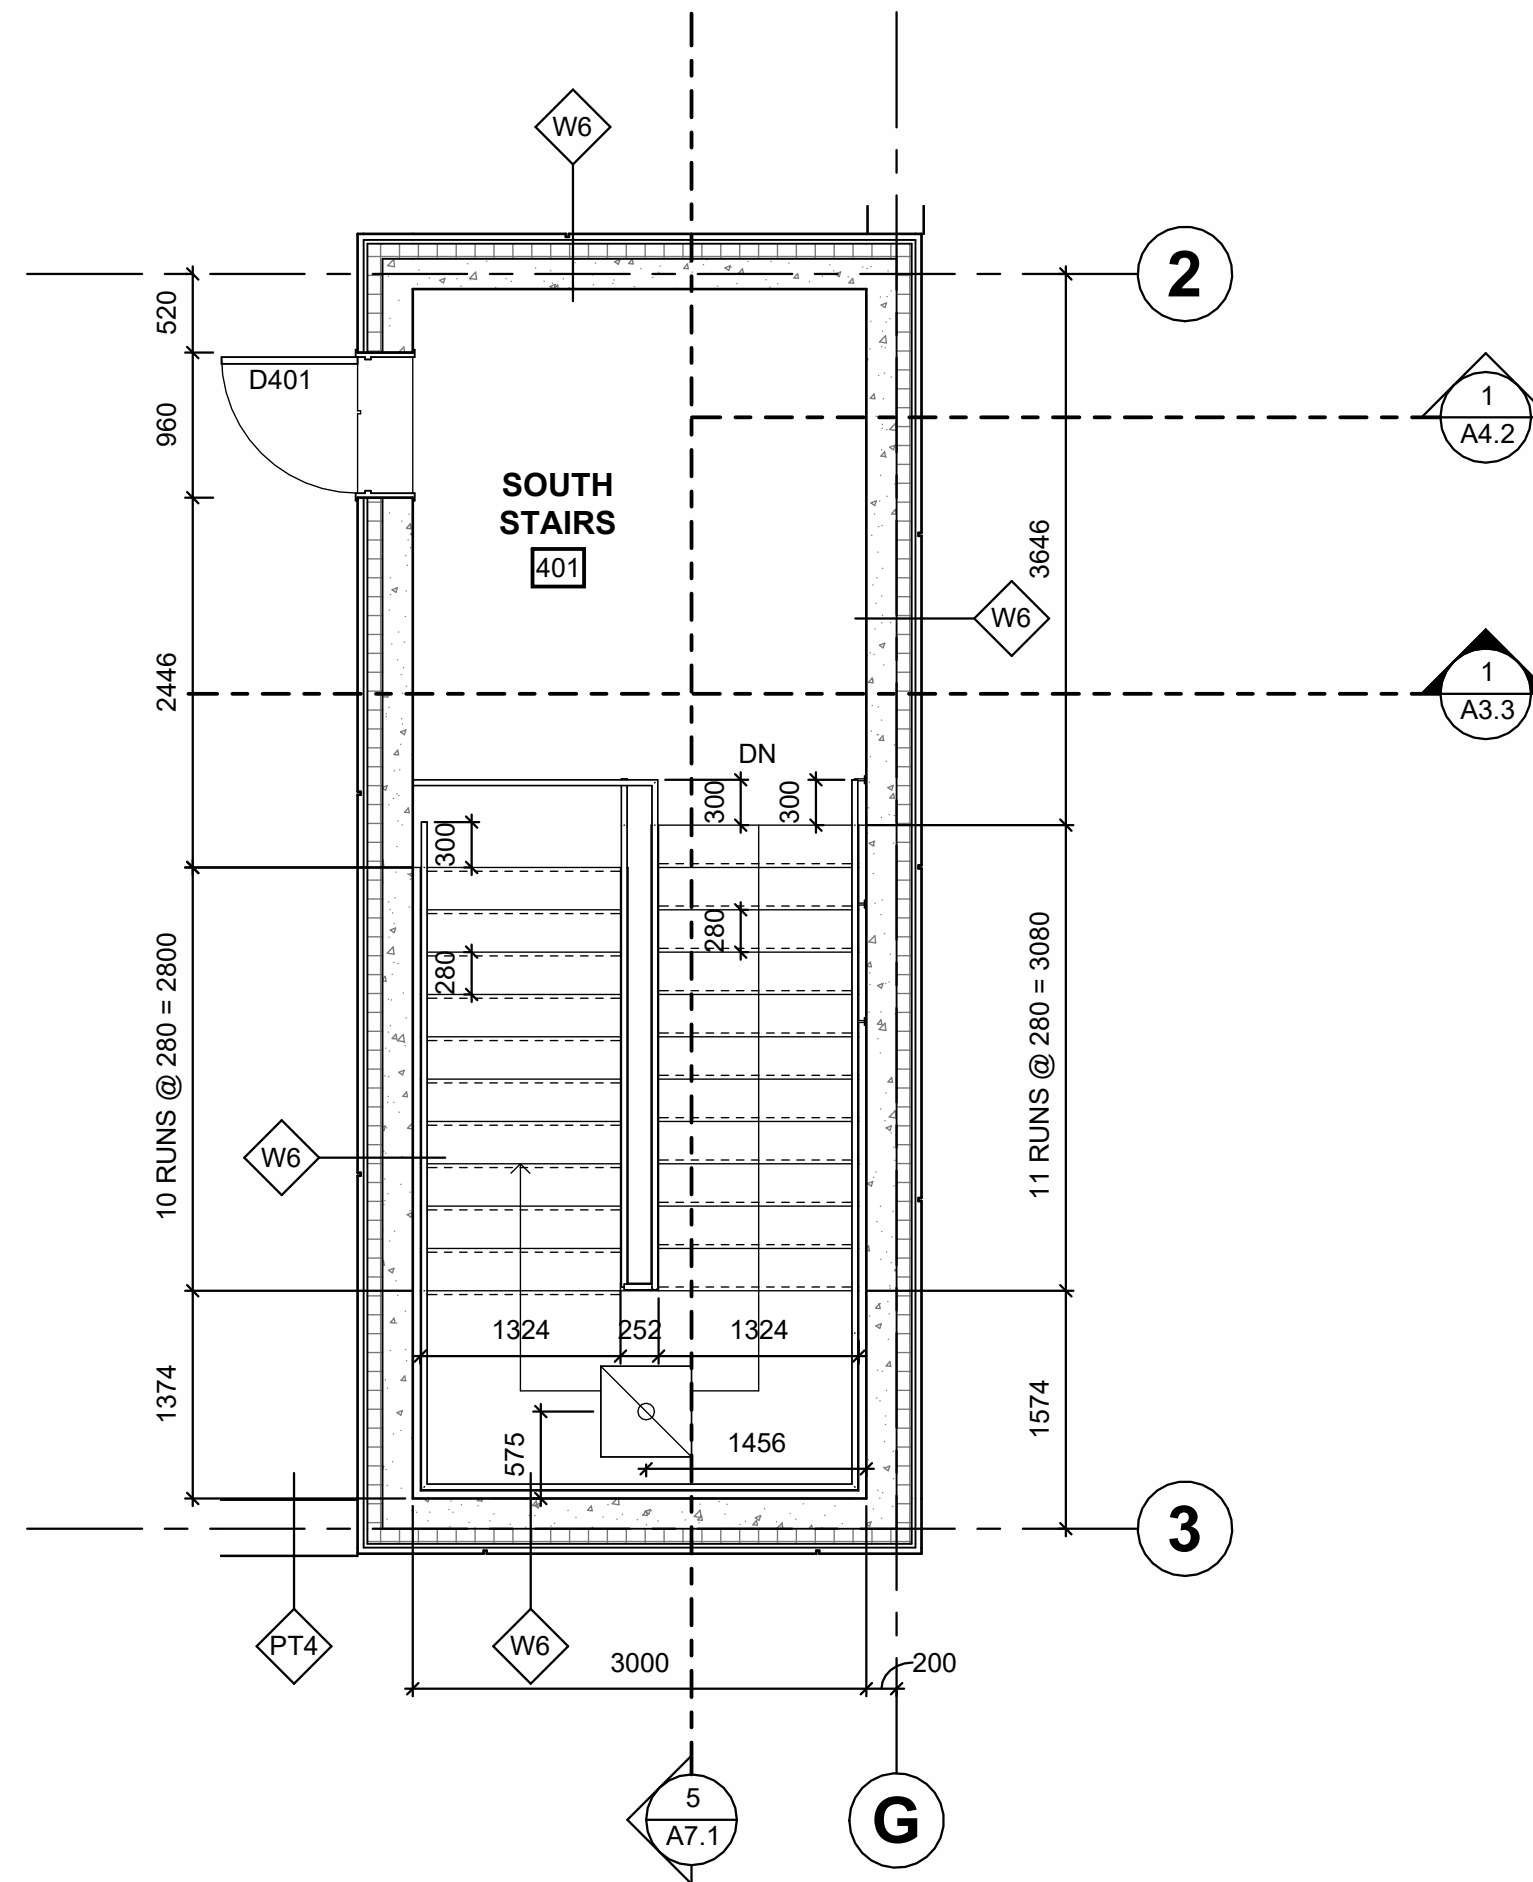

4 SOUTH STAIRS FOURTH FLOOR PLAN
A7.1 SCALE = 1 : 50

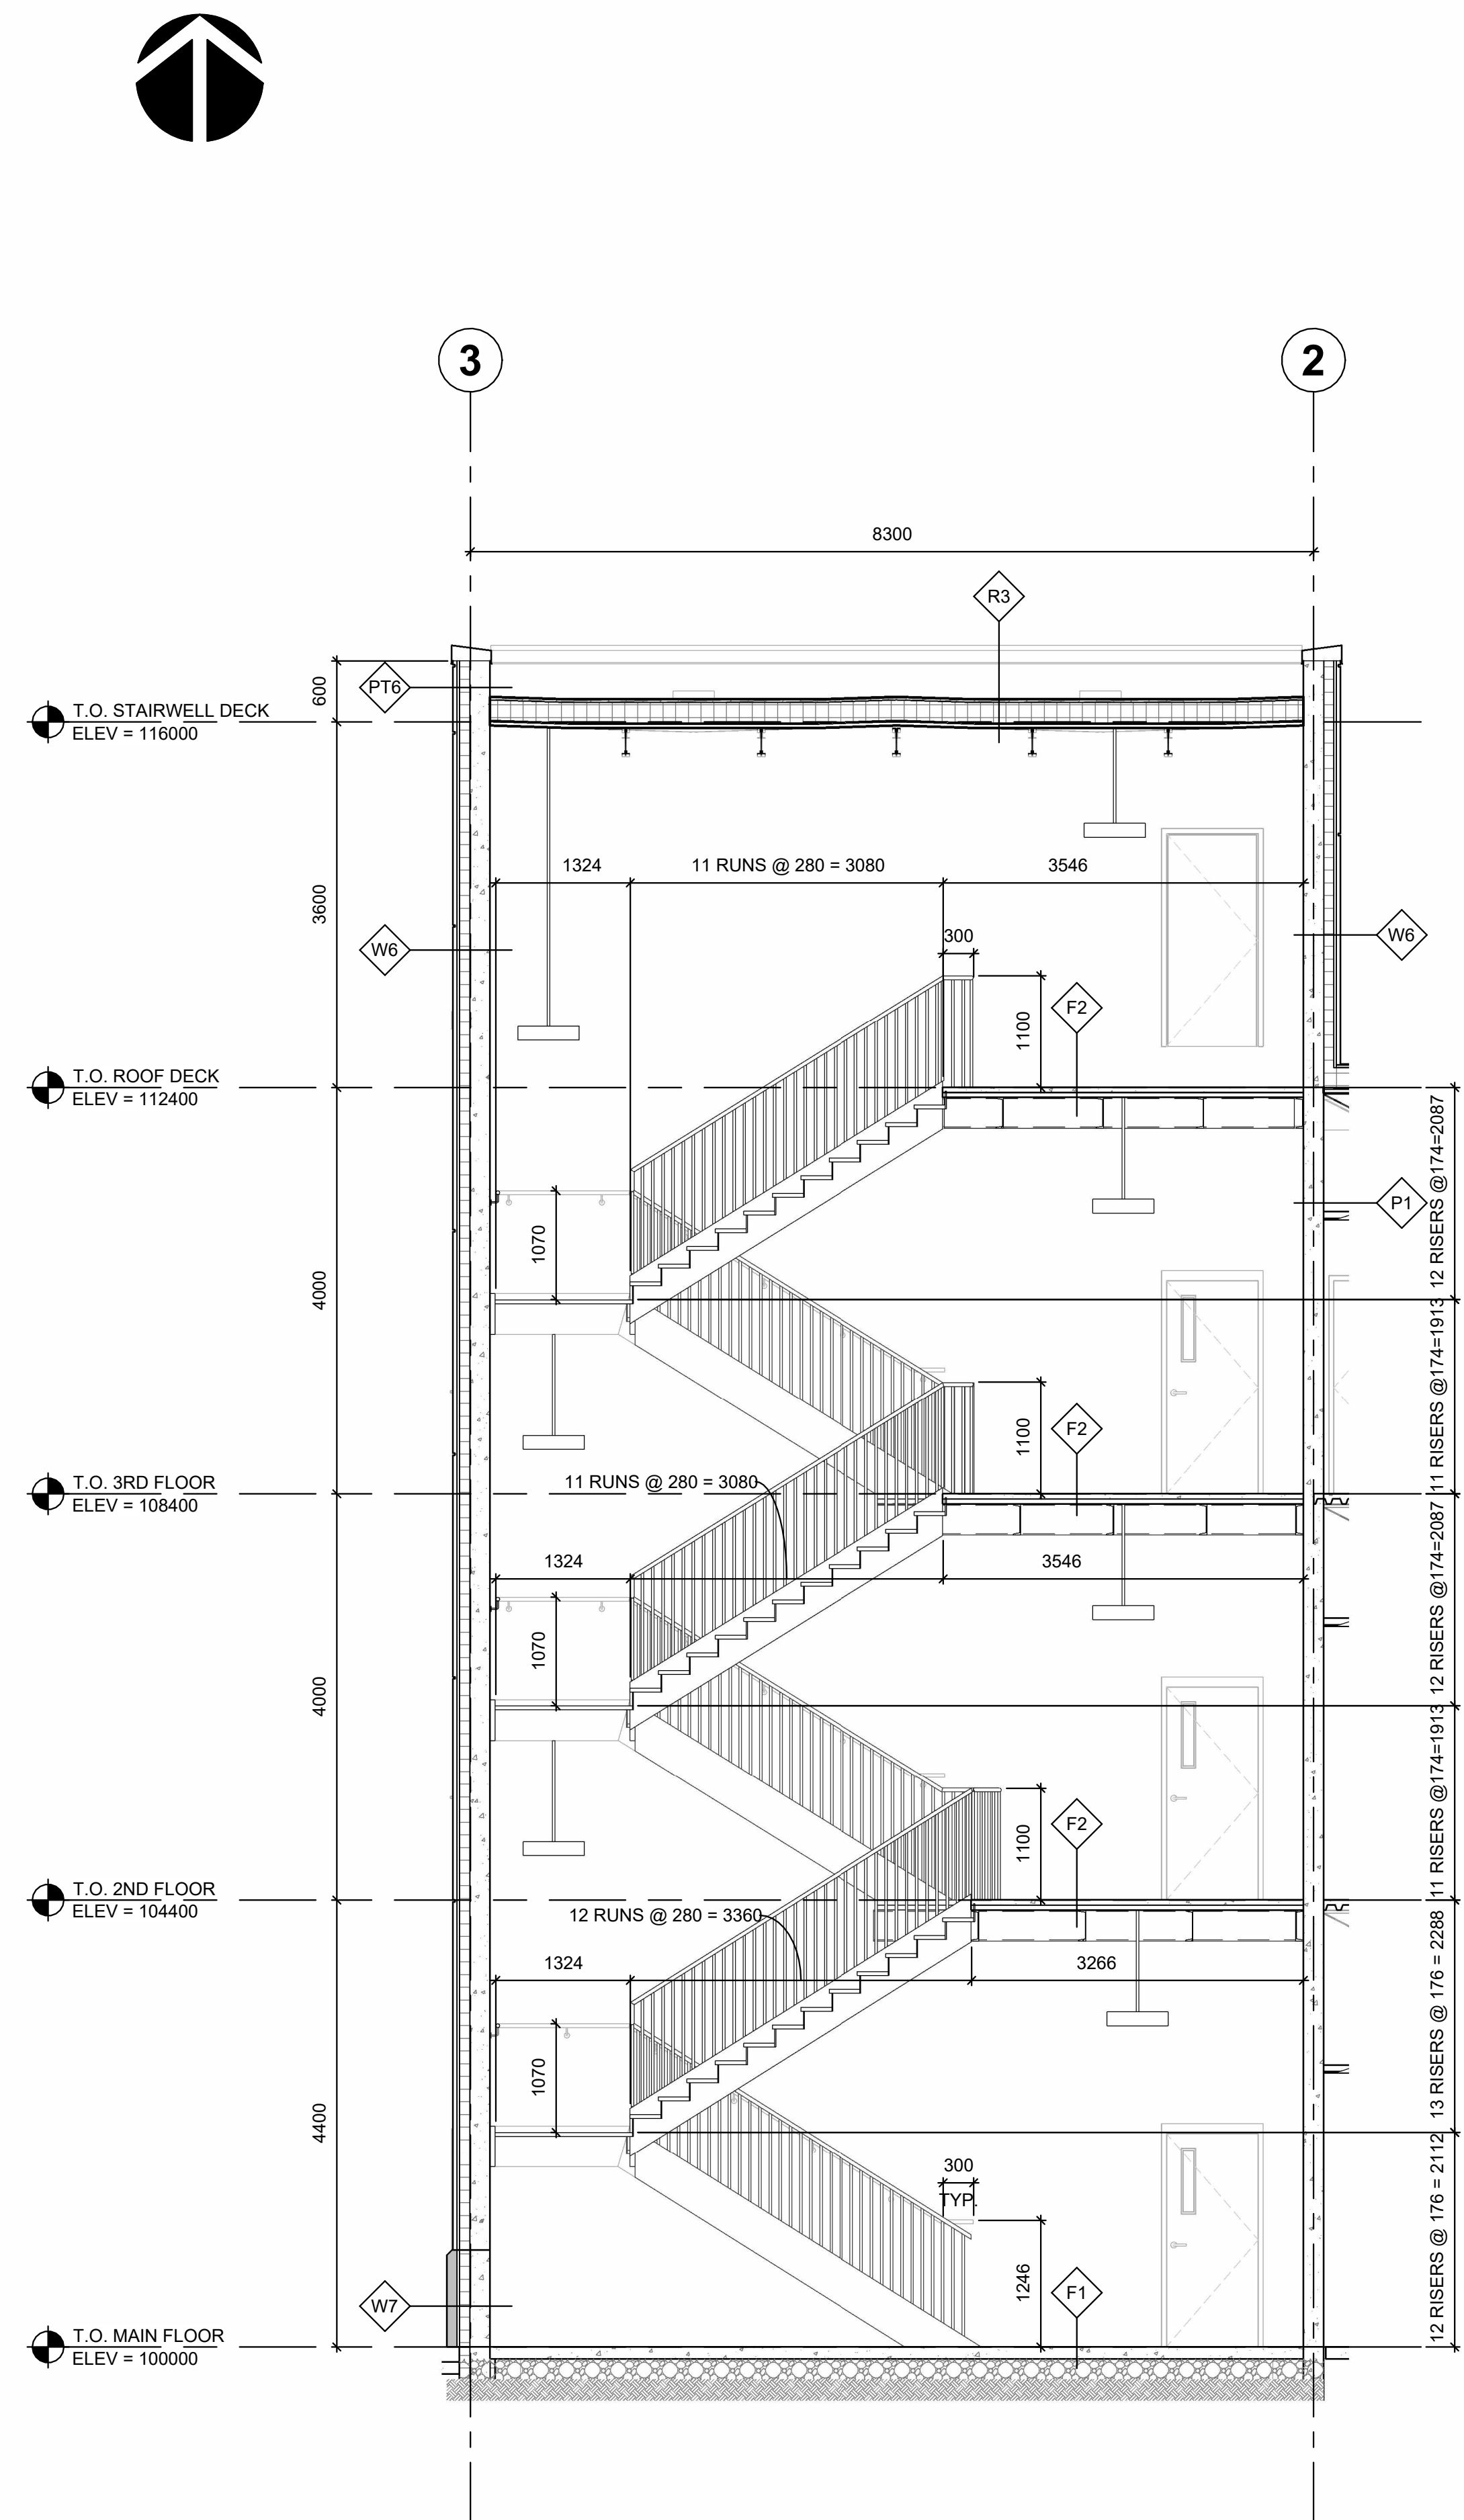

5 SOUTH STAIRS SECTION
A2.1 SCALE = 1 : 50