

[illegible]

NAIT
AMBULANCE
HEADQUARTERS

WALL SECTIONS

Class Number	A03
--------------	-----


Date 23/03/2026

Drawn by **CHIDERA UZO**


Instructor **ANDRE LUCENA**

A4.2


Scale 1 : 50

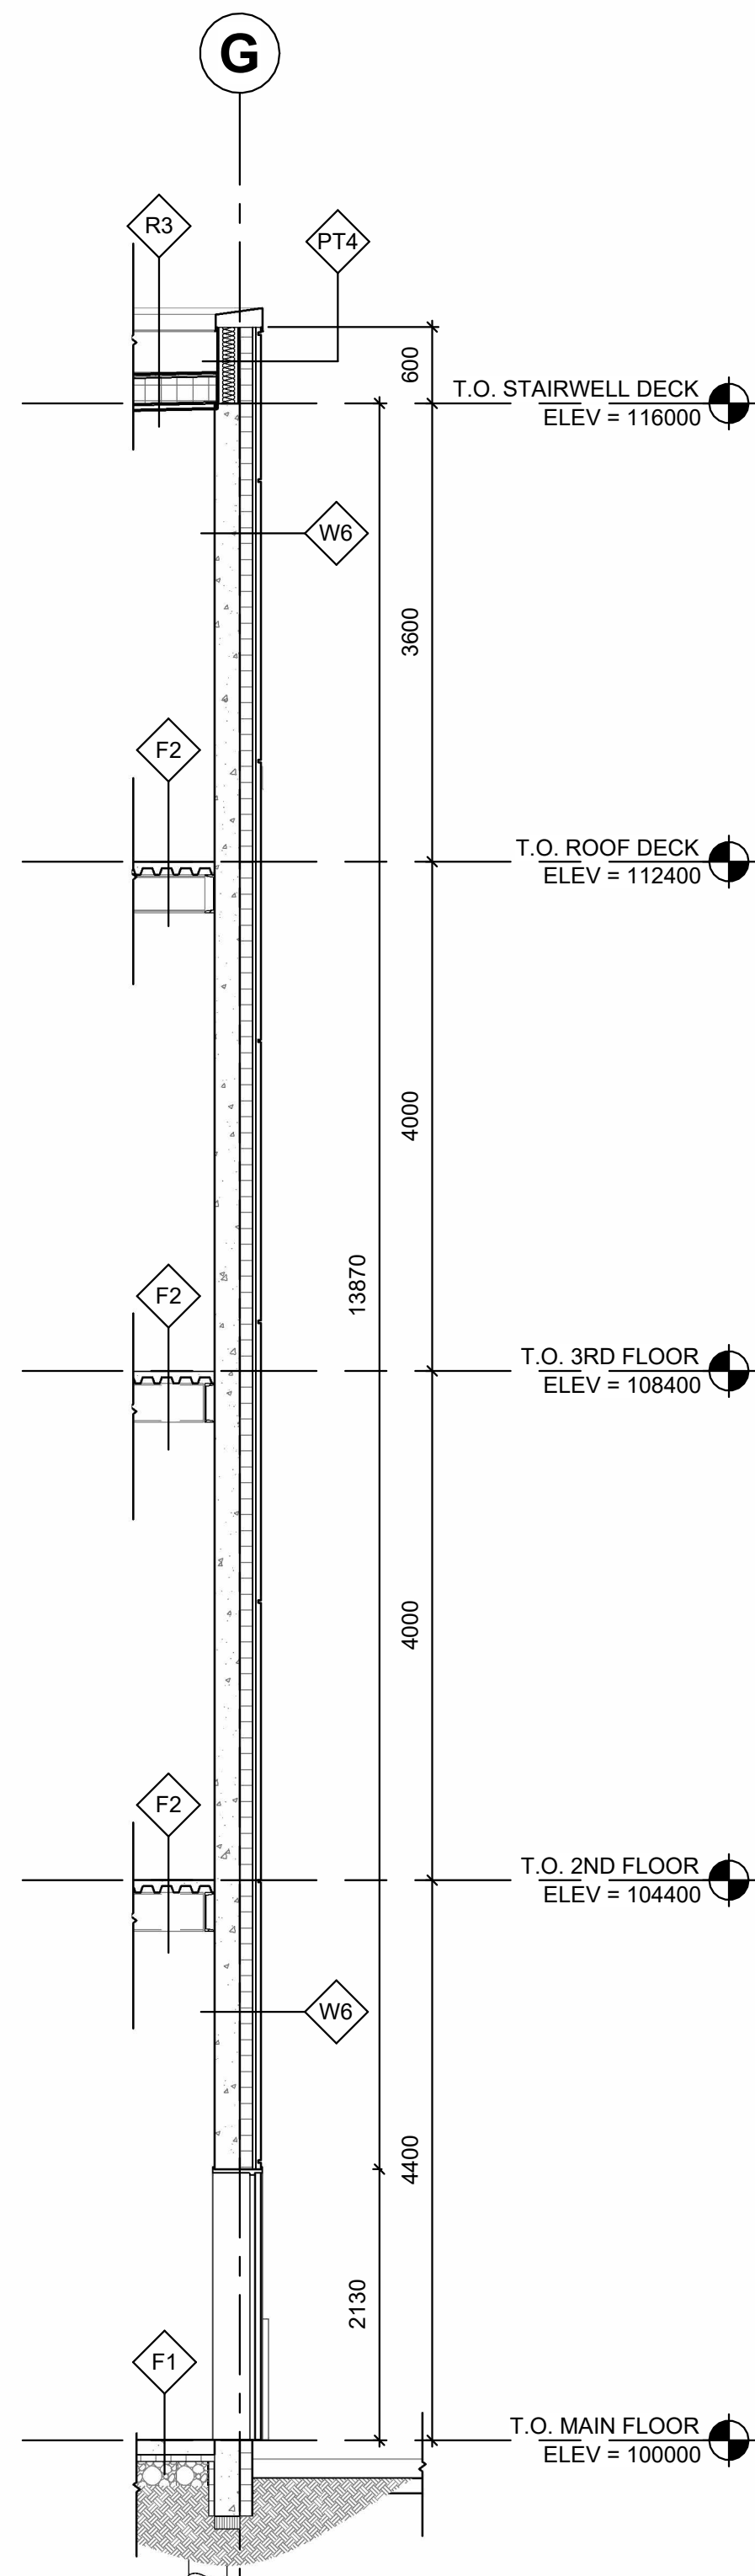


1 WALL SECTION
A2.1 SCALE = 1 : 50

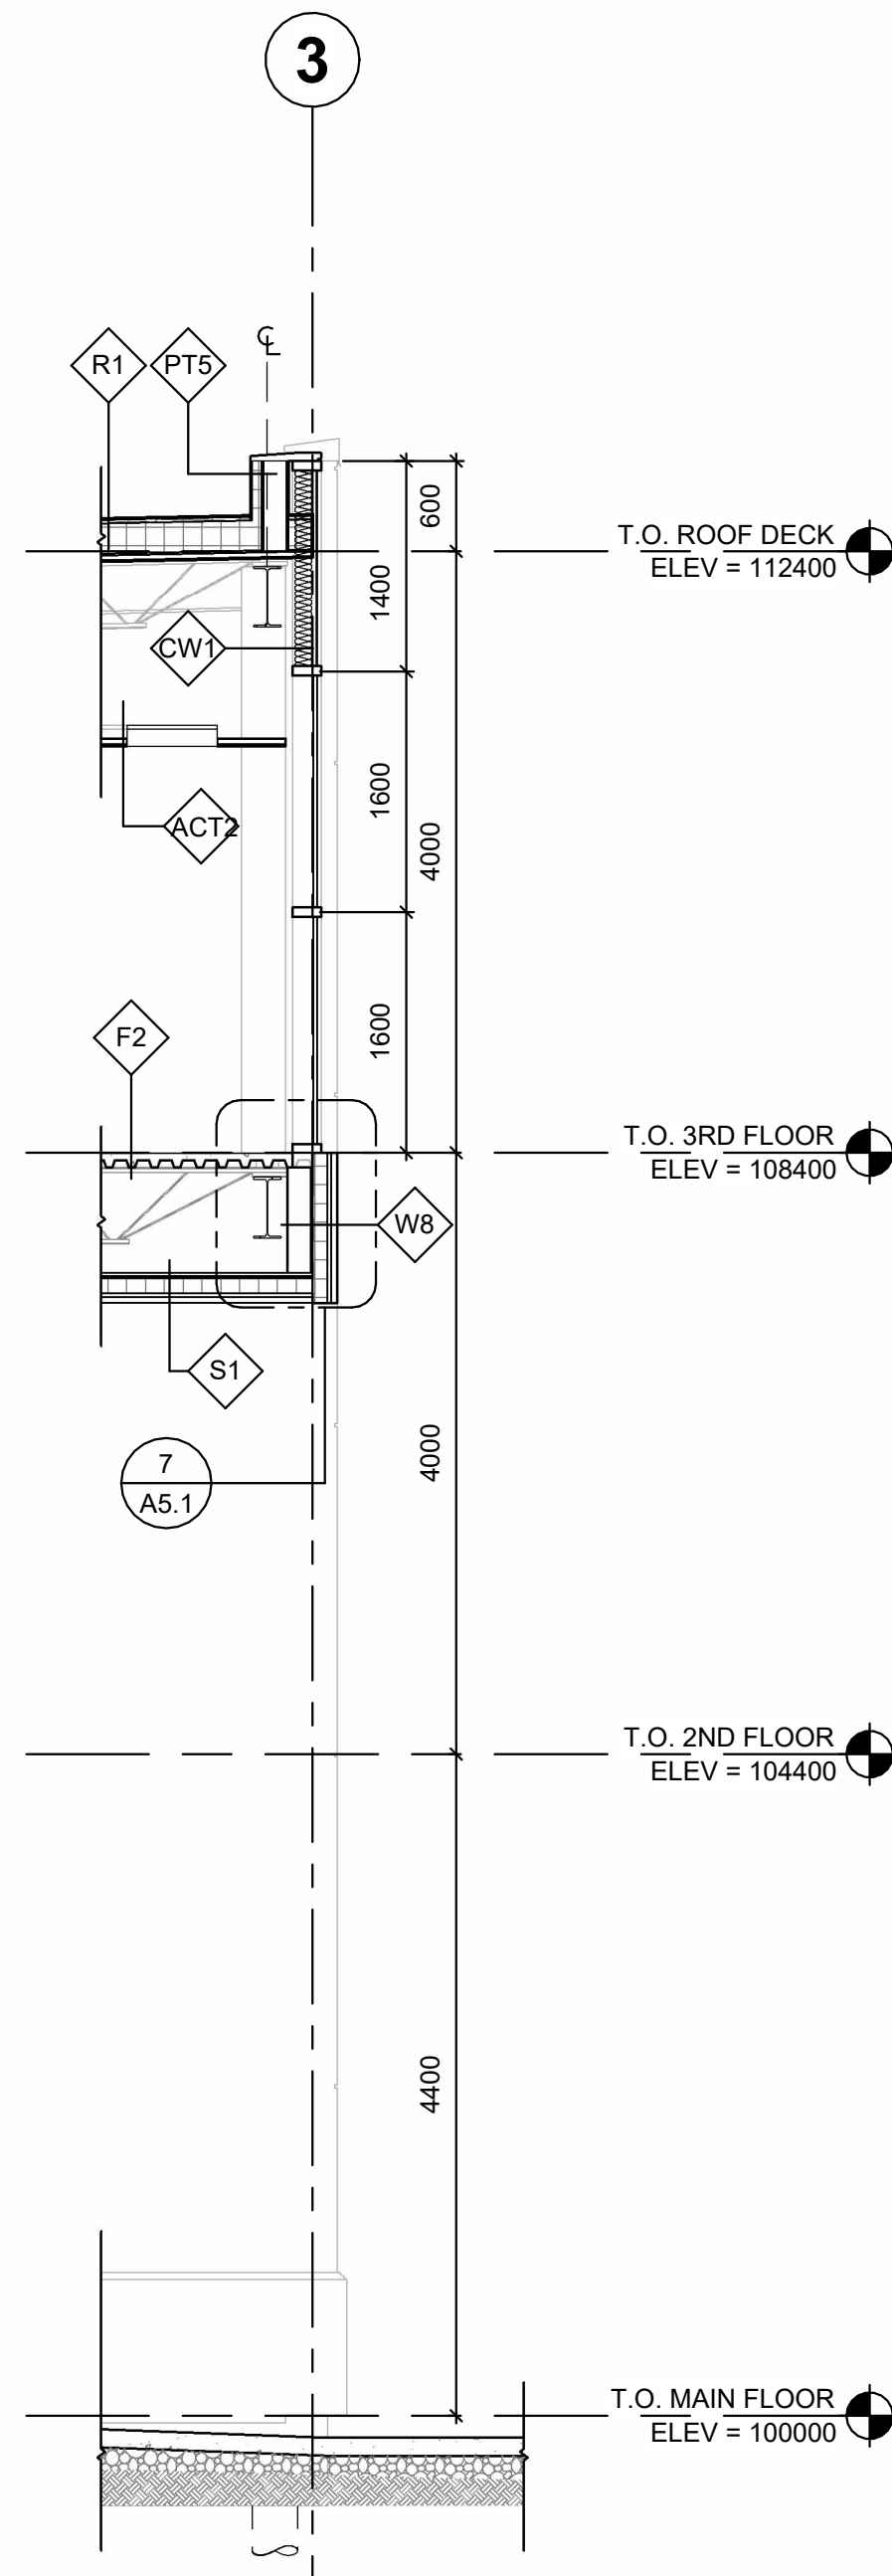


2 WALL SECTION
A3.4 SCALE = 1 : 50

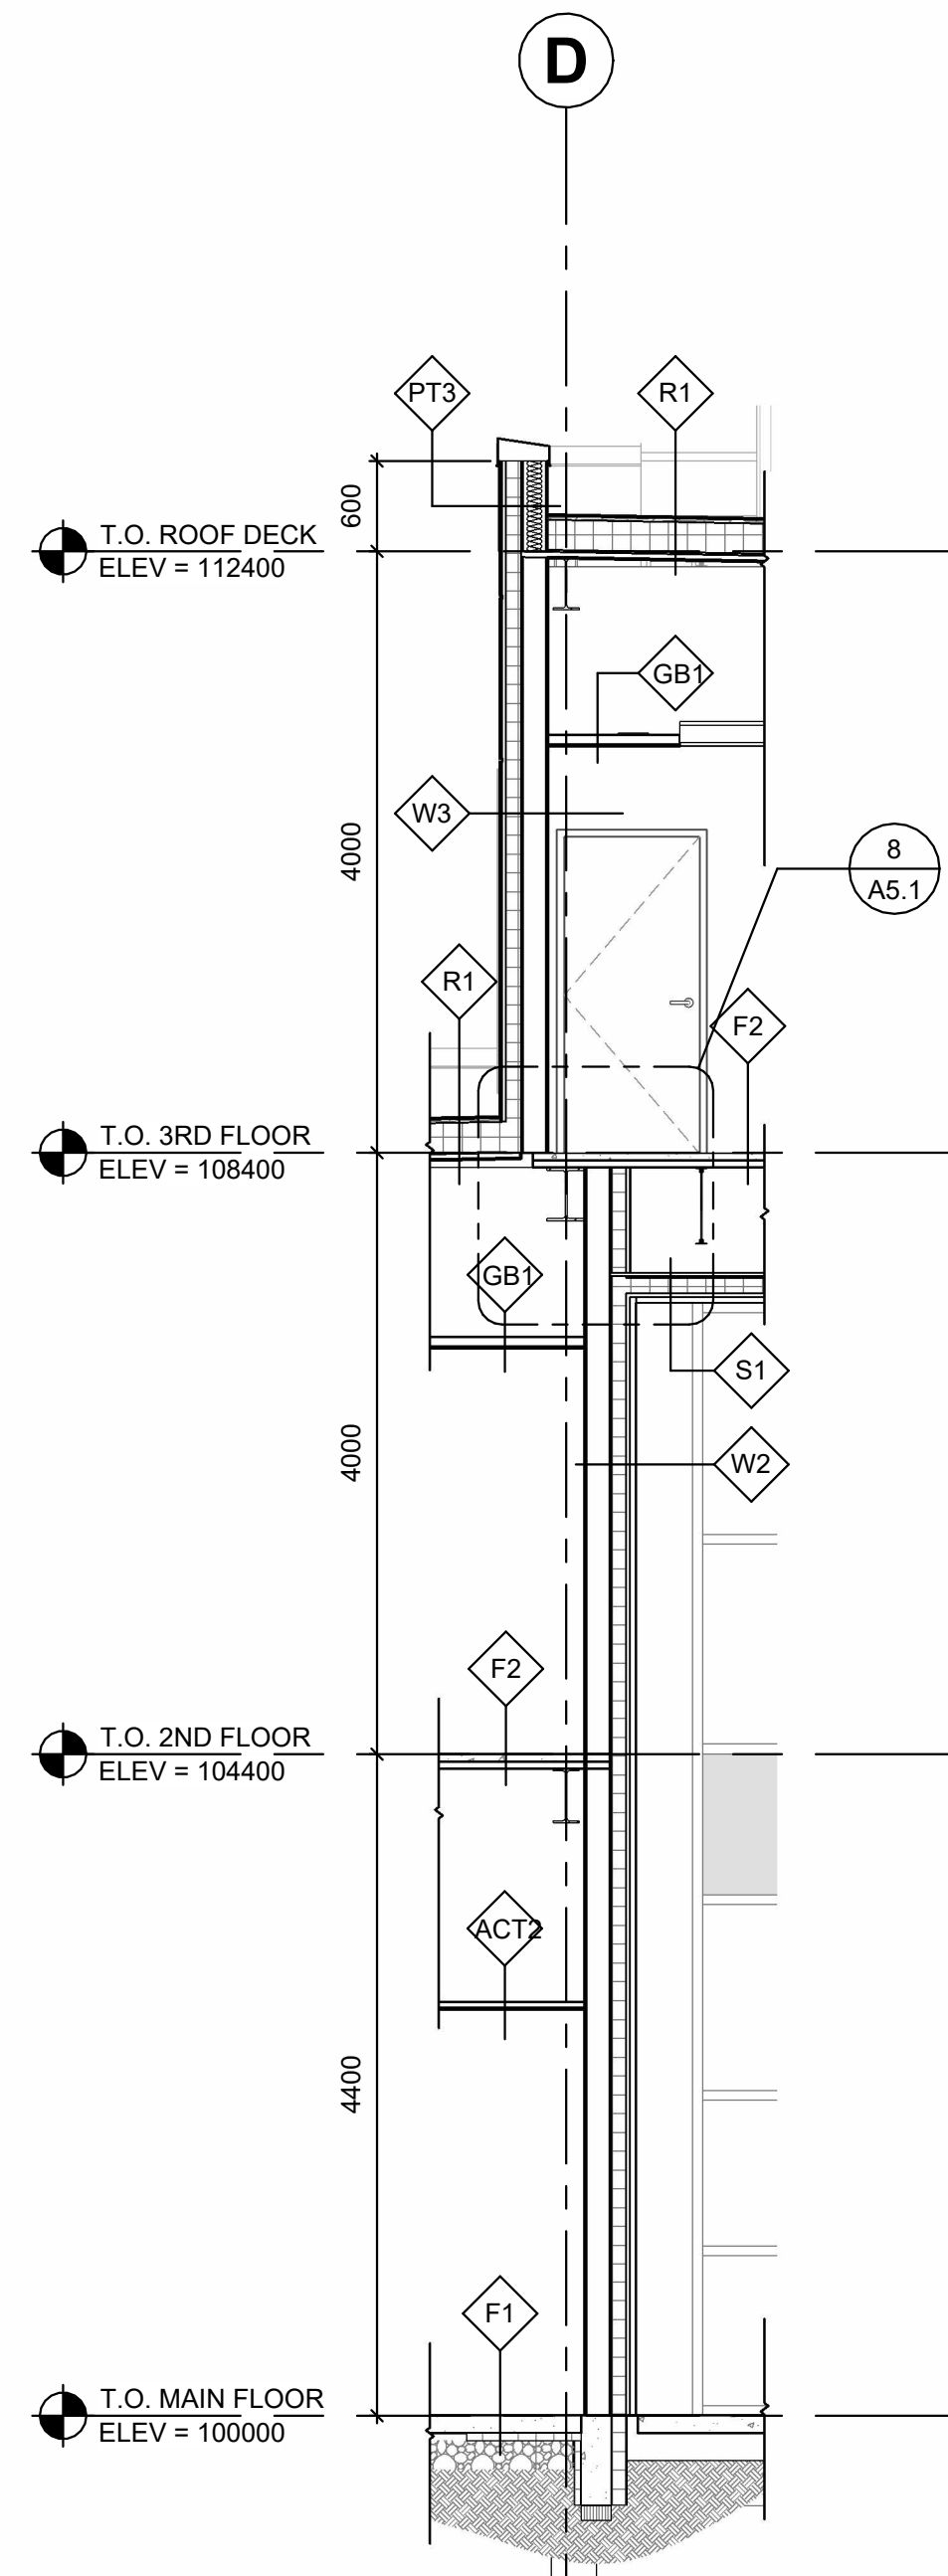

3 WALL SECTION
A3.3 SCALE = 1 : 50

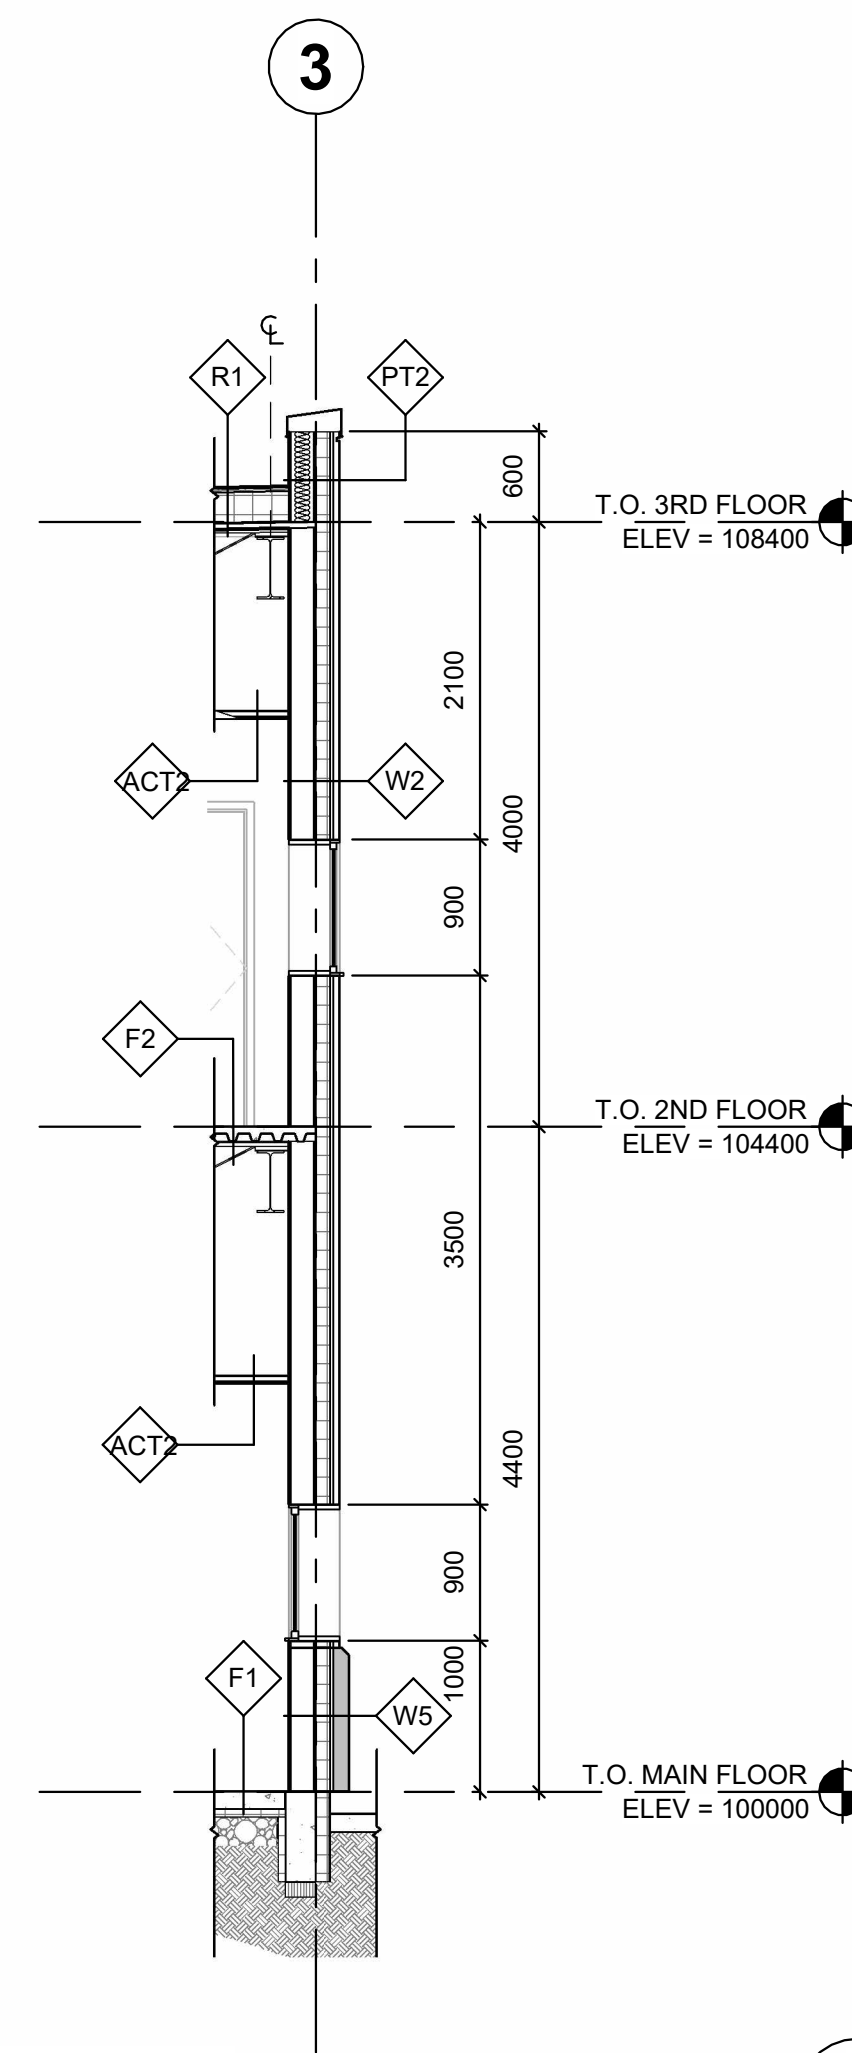

4 WALL SECTION
A3.4 SCALE = 1 : 50

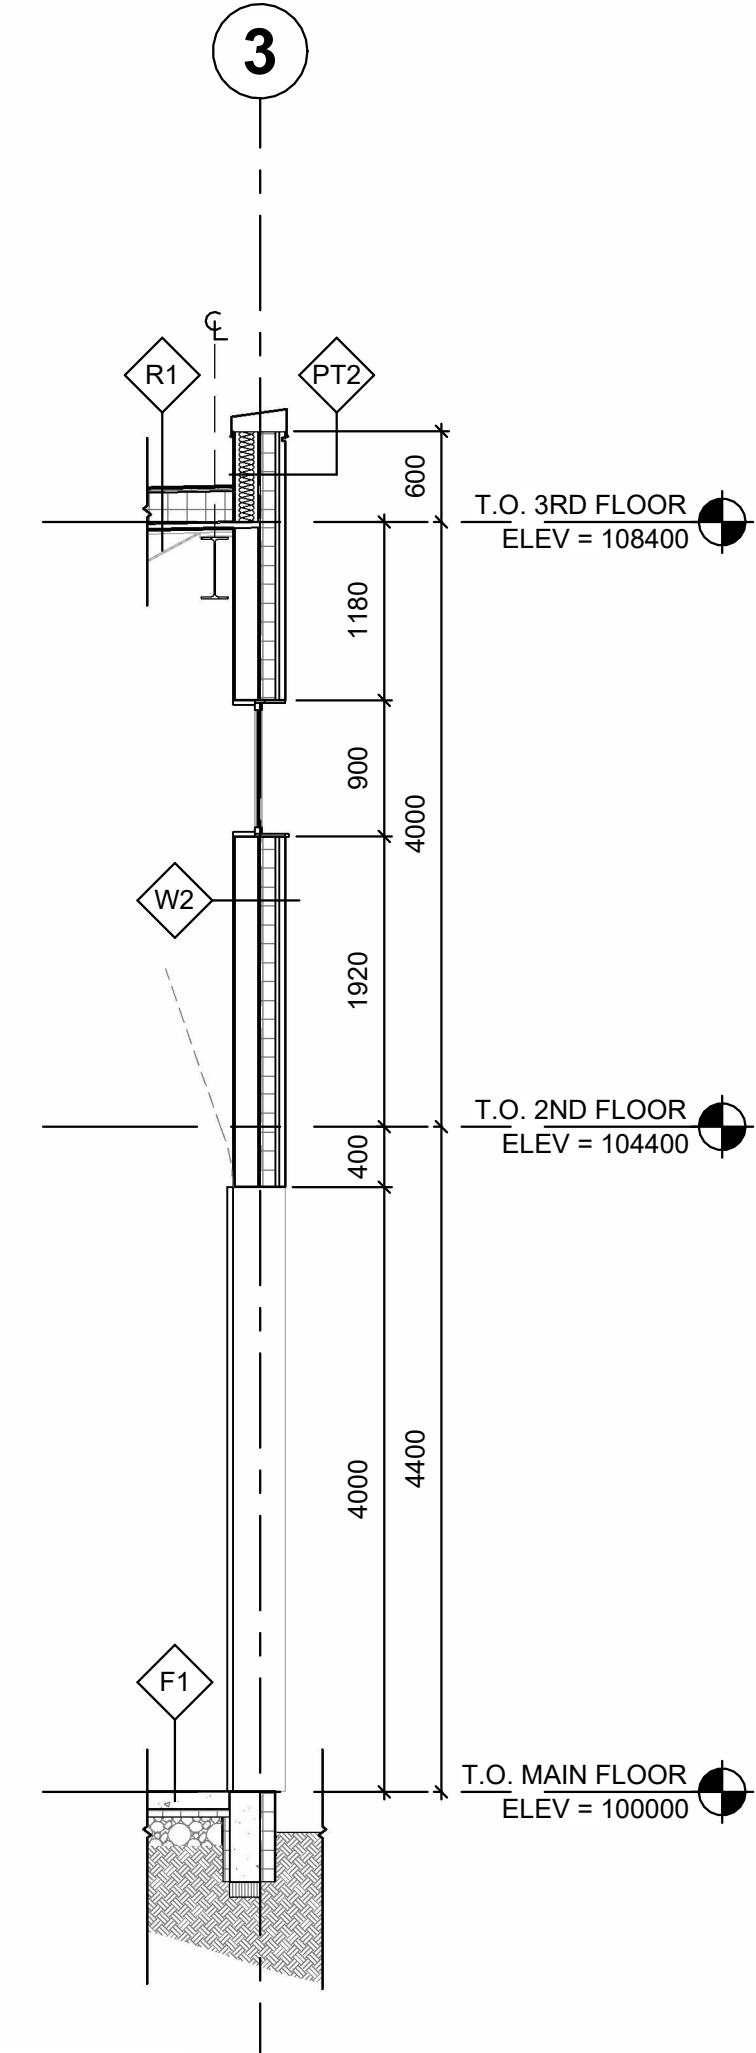

5 WALL SECTION